


D4-2-2

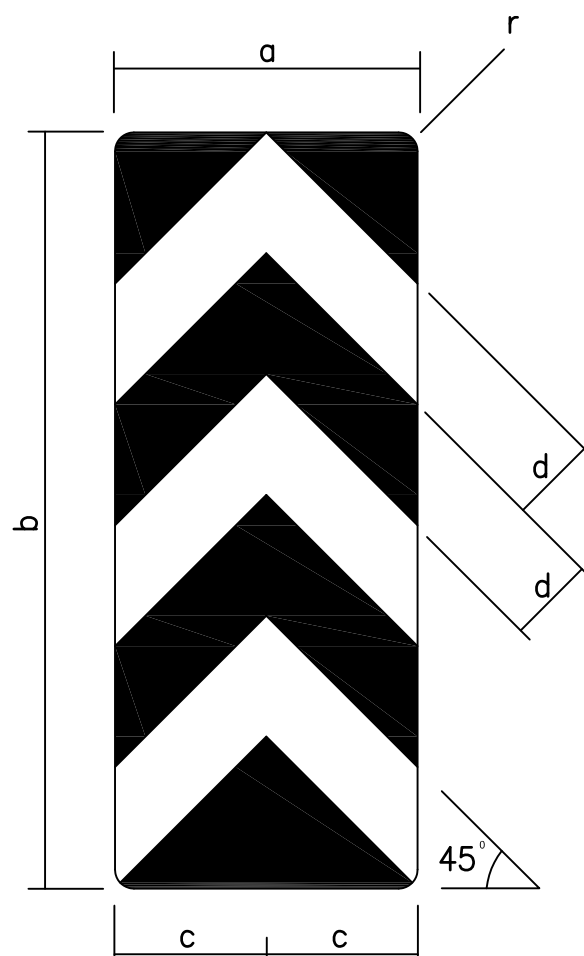

White reflectorised chevrons on Black ground

	a	b	c	d	r
D4-2-2A	300	750	150	85	19
D4-2-2B	400	1000	200	113	25

SCALE 1:10

TITLE

HAZARD MARKER
D4-2-2

Drawn: MD

6-4-18

CHKED: CHECKED

CHECKED_DATE



Transport
Roads & Maritime
Services

GUIDANCE AND DELINEATION UNIT
27-31 ARGYLE ST, PARRAMATTA 2150

H:\SIGNS\TTT\DRAWINGS\LOT\WARNING\D4-2-2

Revision: X