


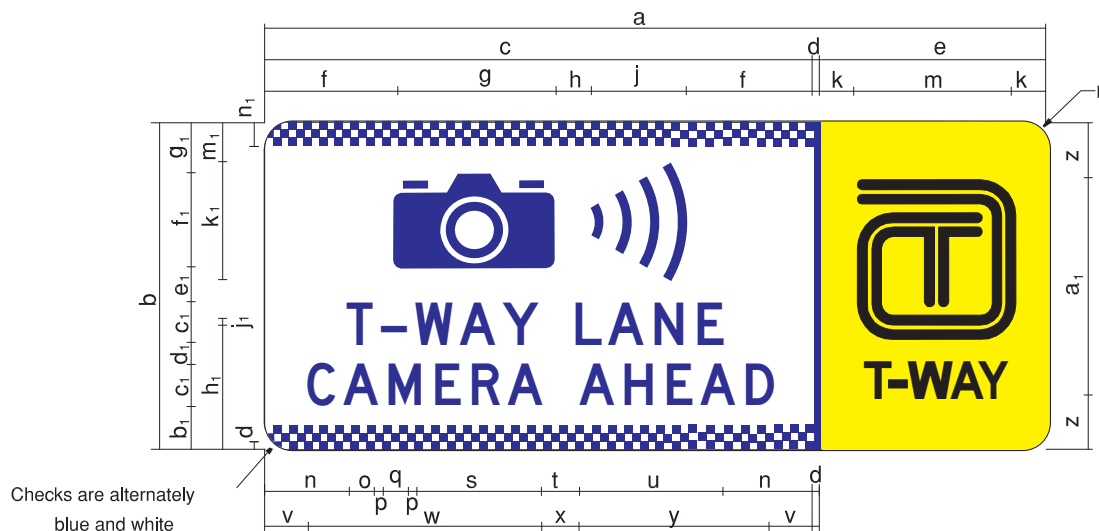


Left Panel: Cl.1 blue ref legend on Cl.1 white ref ground.

Dividing line: Cl.1 blue ref.

Right Panel: Black legend and symbol on Cl.1 yellow ref ground.

	a	b	c	d	e	f	g	h	j	k	m	n	o	p	q	r	s	t	u
G6-342A	2240	940	1568	22	650	369	454	101	275	100	450	251	73	20	60	80	347	112	429
G6-342B	3730	1560	2614	36	1080	617	756	168	456	380	320	430	122	33	100	130	580	185	697

v	w	x	y	z	a ₁	b ₁	c ₁	d ₁	e ₁	f ₁	g ₁	h ₁	j ₁	k ₁	m ₁	n ₁	o ₁
112	679	102	562	158	624	126	120DM	60	101	270	143	356	19	336	109	66	24
188	1130	169	935	260	1040	208	200DM	100	166	448	238	593	31	560	182	108	40

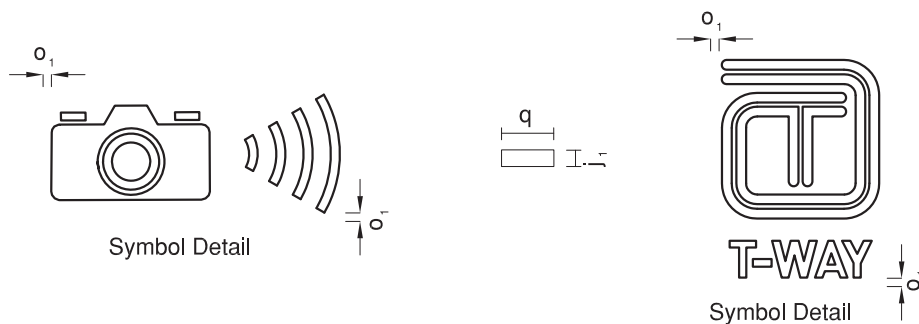

REVISIONS: 1.- Title block revised 5/07/16.

SCALE:1:18

TITLE

GUIDE SIGN

G6-342

Drawn: PG/FR

13-12-07

CHKED: FR

7-07-2016



GUIDANCE AND DELINEATION UNIT
27-31 ARGYLE ST, PARRAMATTA 2150

H:\SIGNS\TTT\DRAWINGS\PLOT\guide\ G6-342.DWG

Revision: 1