


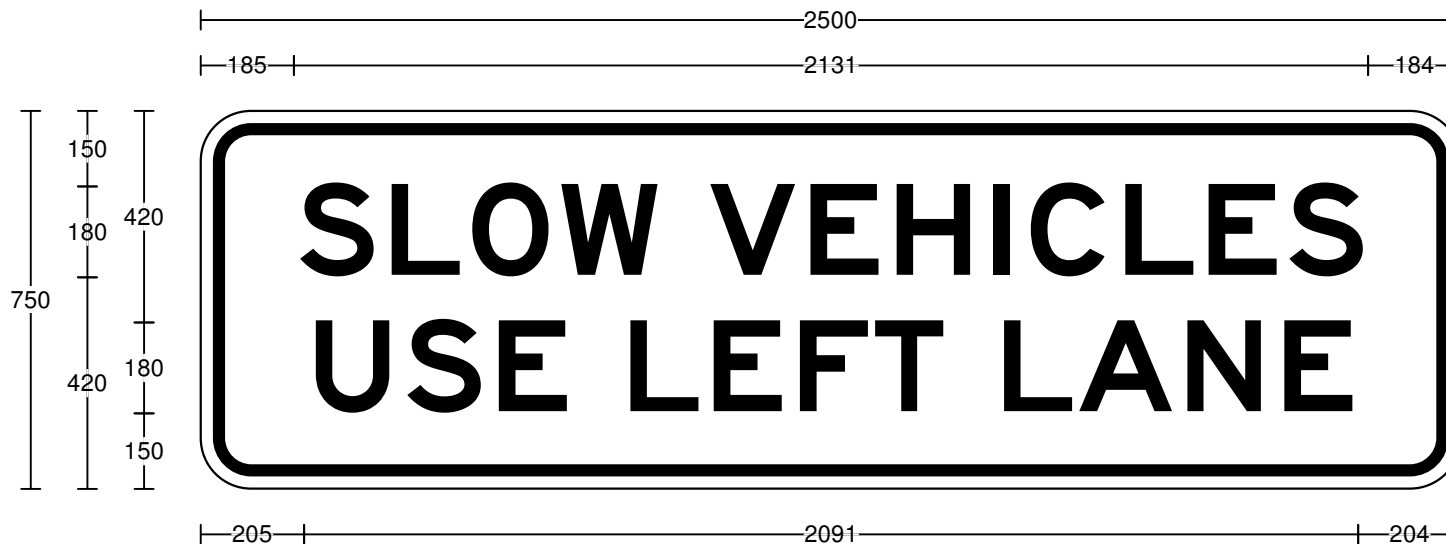

<u>Legend</u>	<u>Font Type</u>	<u>Font Size</u>
SLOW VEHICLES	FHWA Series E2000EX	180
USE LEFT LANE	FHWA Series E2000EX	180

Specifications:
 BACKLIT SIGN
 Black lgd
 White grd

Size:	750 x 2500	Date:	30/9/19
Area:	1.88 sq.m	Scale:	1:15
Border:	24 x 24	Drawn:	RozosJ
Cnr Rad:	100	Checked:	
Patch CR:	NA	File:	G9--12-1n
 Transport Roads & Maritime Services		Path:	H:\Signs\Standard_Signs & Symbols\Tunnel Signs\New Tunnel Signs
Prepared using TraSICAD Product of QMR		Guidance & Delineation Team Traffic Engineering Services Technical & Project Services 99 Phillip St Parramatta NSW 2150	G9-12-1n