
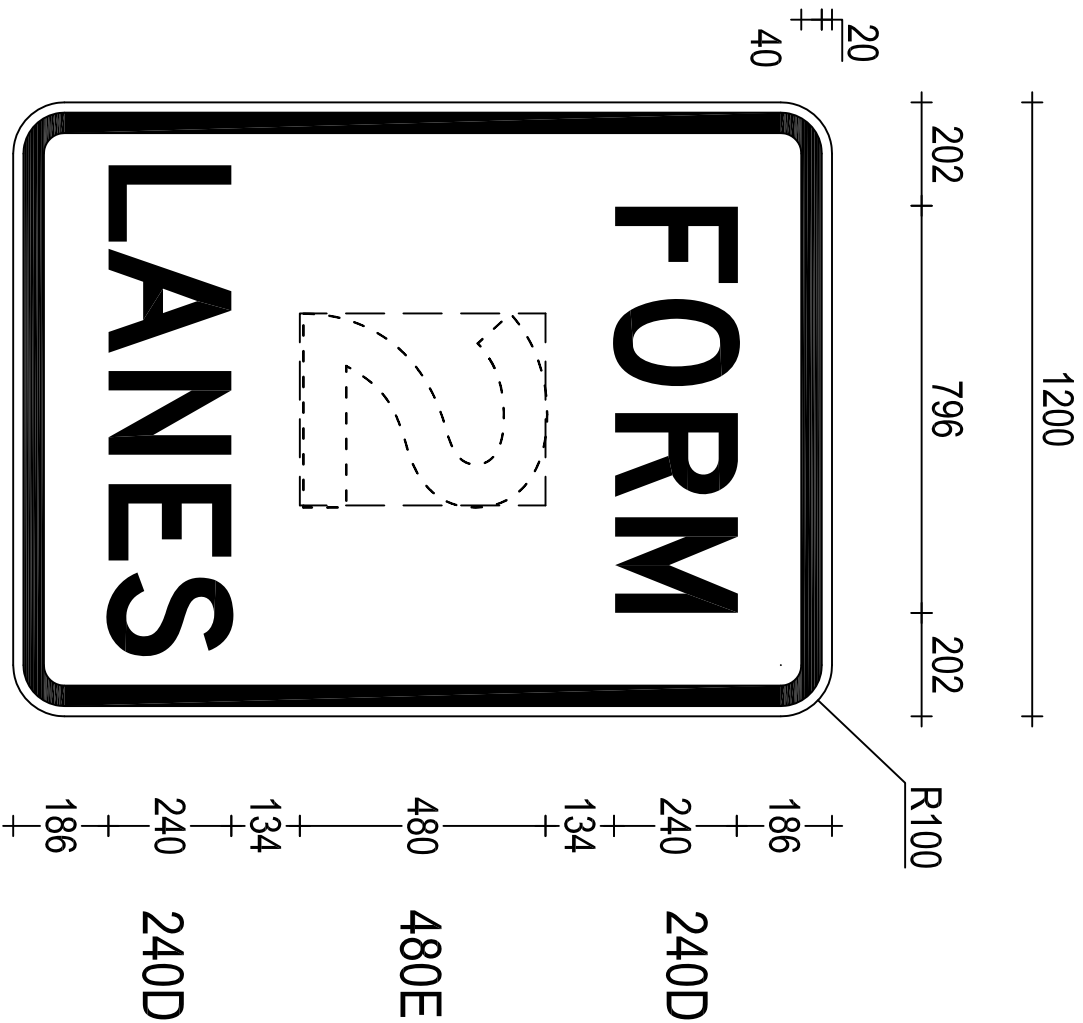
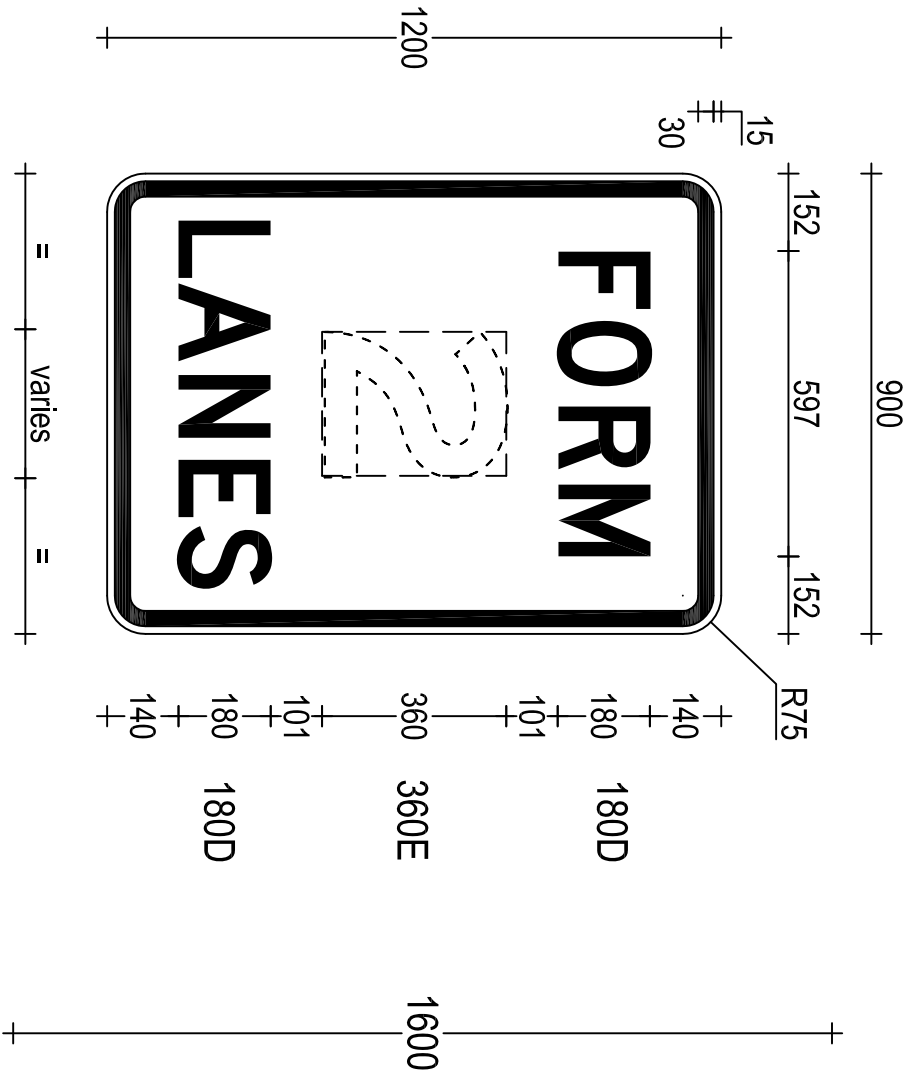


OR CODE Scan to Check Document Version		REV 01	DATE 23-03-18	AMENDMENT / REVISION DESCRIPTION AS Forms & material classification revised	APPROVAL P. Oliver	DRAWING FILE LOCATION / NAME: H:\SIGN\TTT\DRAWINGS\PLOT\GUIDE\G9-16.DWG	DESIGNED NAME: M. Davis DATE: 24-3-21	VERIFIED NAME: P. Oliver TITLE: Manager Guidance & Delineation DATE: 24-03-21	 NSW GOVERNMENT Transport Roads & Maritime Services		GUIDE SIGN G9-16 FORM (☐) LANES			SHEET 1 OF 1		A3	
ALL DIMENSIONS ARE IN MILLIMETRES UNLESS OTHERWISE SPECIFIED						SIGN TO BE MANUFACTURED IN ACCORDANCE WITH RMS QA SPECIFICATION 3400	REVIEWED NAME: J. Rozos DATE: 24-03-21	PREPARED BY GUIDANCE AND DELINEATION UNIT ADVANCED TECHNICAL SERVICES INFRASTRUCTURE AND PLACE		SCALE: 1:15		EDMS No. XXXXXXXXXX	SHEET No. 1	ISSUE 01			

ACCEPTED FOR CONSTRUCTION

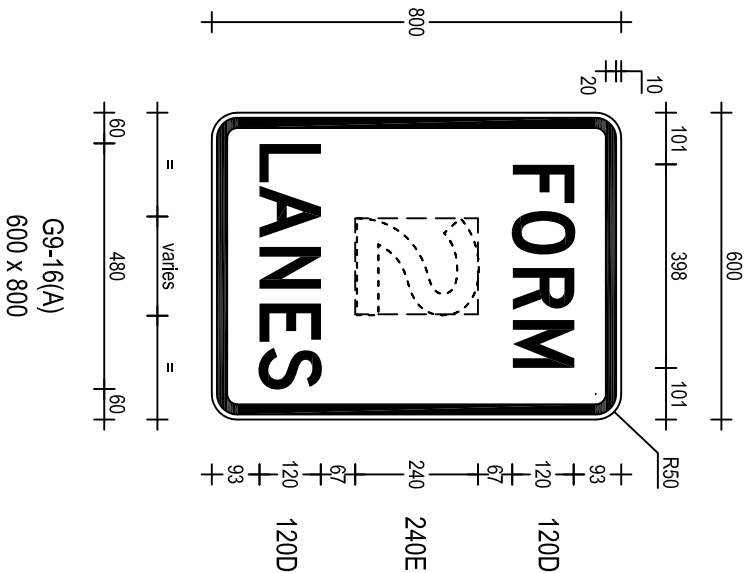

G9-16(C)
1200 x 1600