


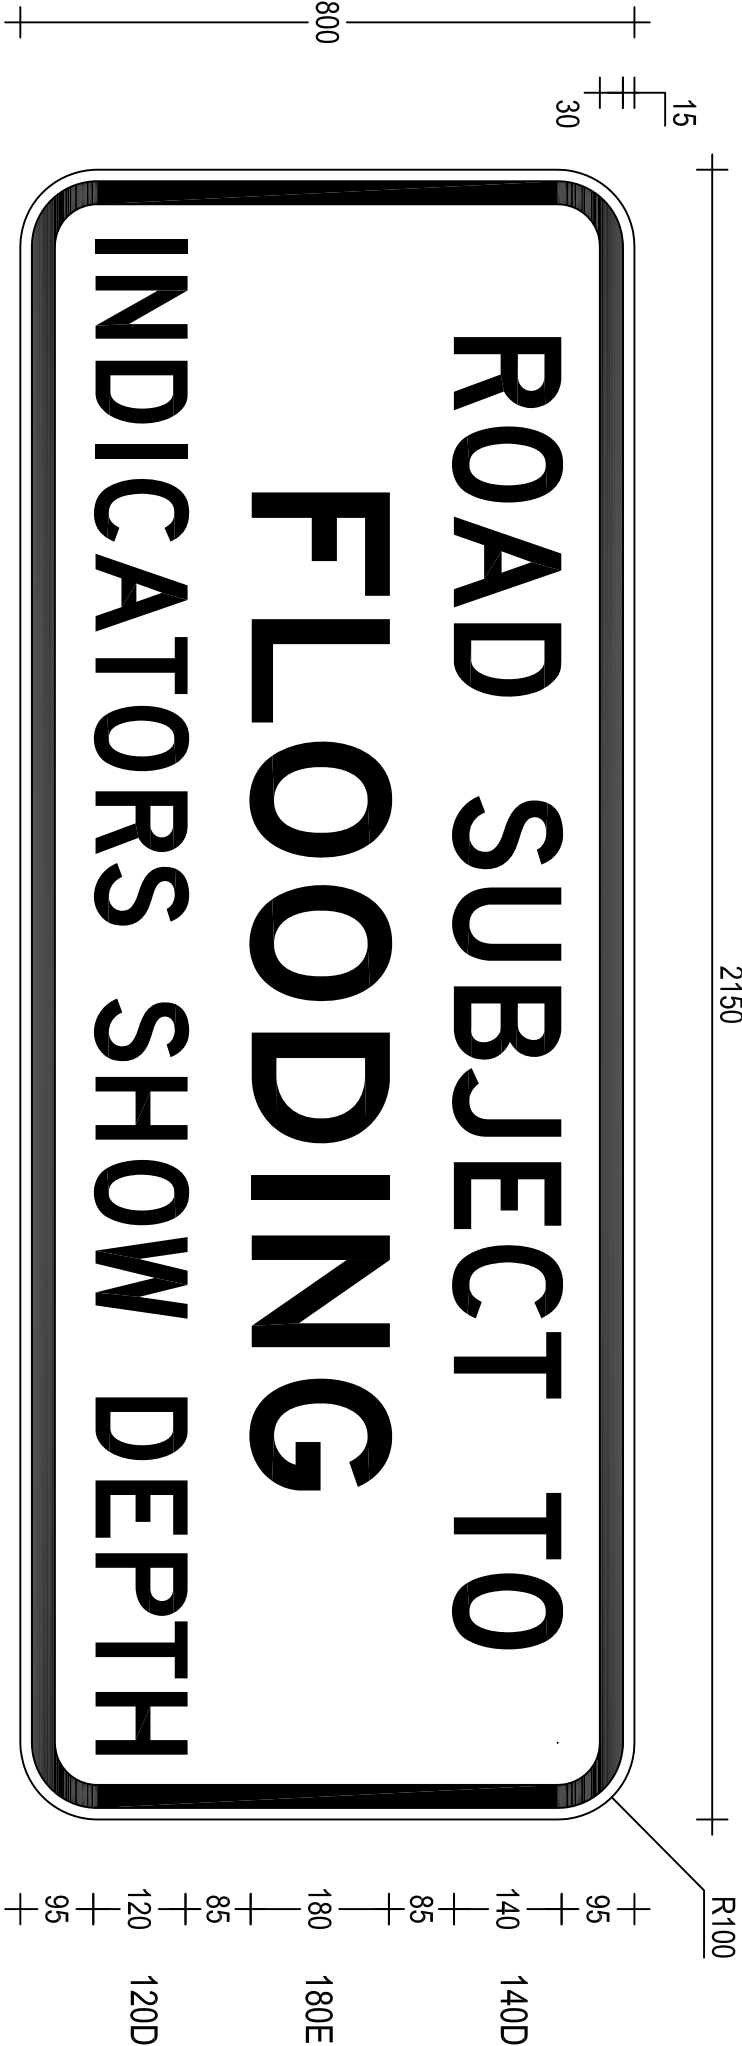

G9-21-1
2150 x 800

ACCEPTED FOR CONSTRUCTION

THIS DRAWING MAY BE PREPARED IN COLOUR AND MAY BE INCOMPLETE IF COPIED

50mm ON A3 SIZE ORIGINAL

OR CODE		Scan to Check Document Version		REV	DATE	AMENDMENT / REVISION DESCRIPTION	APPROVAL	DRAWING FILE LOCATION / NAME: H:\SIGN\TTT\DRAWINGS\PLOT\GUIDE\G9-21.DWG		DESIGNED		VERIFIED		GUIDE SIGN			
				01	23-03-18	AS Forms & material classification revised	P. Oliver			NAME: M. Davies DATE: 23-3-21		NAME: P. Oliver TITLE: Manager Guidance & Delineation DATE: 24-03-21		Transport Roads & Maritime Services			
								MATERIALS: ALUMINIUM SIGN BLACK LEGEND AND BORDER ON AS1906.1 CL.400 WHITE REFLECTORISED GROUND		REVIEWED				G9-21-1 2150 x 800			
								SIGN TO BE MANUFACTURED IN ACCORDANCE WITH RMS QA SPECIFICATION 3400		NAME: J. Rozos DATE: 24-03-21				SHEET 1 OF 1			
ALL DIMENSIONS ARE IN MILLIMETRES UNLESS OTHERWISE SPECIFIED														SCALE: 1:10		EDMS No. XXXXXXXXXX	
																SHEET No. 1	
																ISSUE 01	
																A3	