


OR CODE Scan to Check Document Version		REV 01	DATE 23-03-18	AMENDMENT / REVISION DESCRIPTION AS Forms & material classification revised	APPROVAL P. Oliver	DRAWING FILE LOCATION / NAME: H:\SIGN\TTT\DRAWINGS\PLOT\GUIDE\G9-237n.DWG	DESIGNED NAME: M. Davies DATE: 24-3-21	VERIFIED NAME: P. Oliver TITLE: Manager Guidance & Delineation DATE: 24-03-21	 NSW GOVERNMENT Transport Roads & Maritime Services		GUIDE SIGN G9-237n DO NOT QUEUE ACROSS INTERSECTION SHEET 1 OF 1				EDMS No. XXXXXXXXXX		SHEET No. 1	ISSUE 01	A3
ALL DIMENSIONS ARE IN MILLIMETRES UNLESS OTHERWISE SPECIFIED						SIGN TO BE MANUFACTURED IN ACCORDANCE WITH RMS QA SPECIFICATION 3400	MATERIALS: ALUMINIUM SIGN BLACK LEGEND AND BORDER ON AS1906.1 CL.400 WHITE REFLECTORISED GROUND	REVIEWED NAME: J. Rozos DATE: 24-03-21	PREPARED BY GUIDANCE AND DELINEATION UNIT ADVANCED TECHNICAL SERVICES INFRASTRUCTURE AND PLACE		SCALE: 1:10								

G9-237n
750 X 900

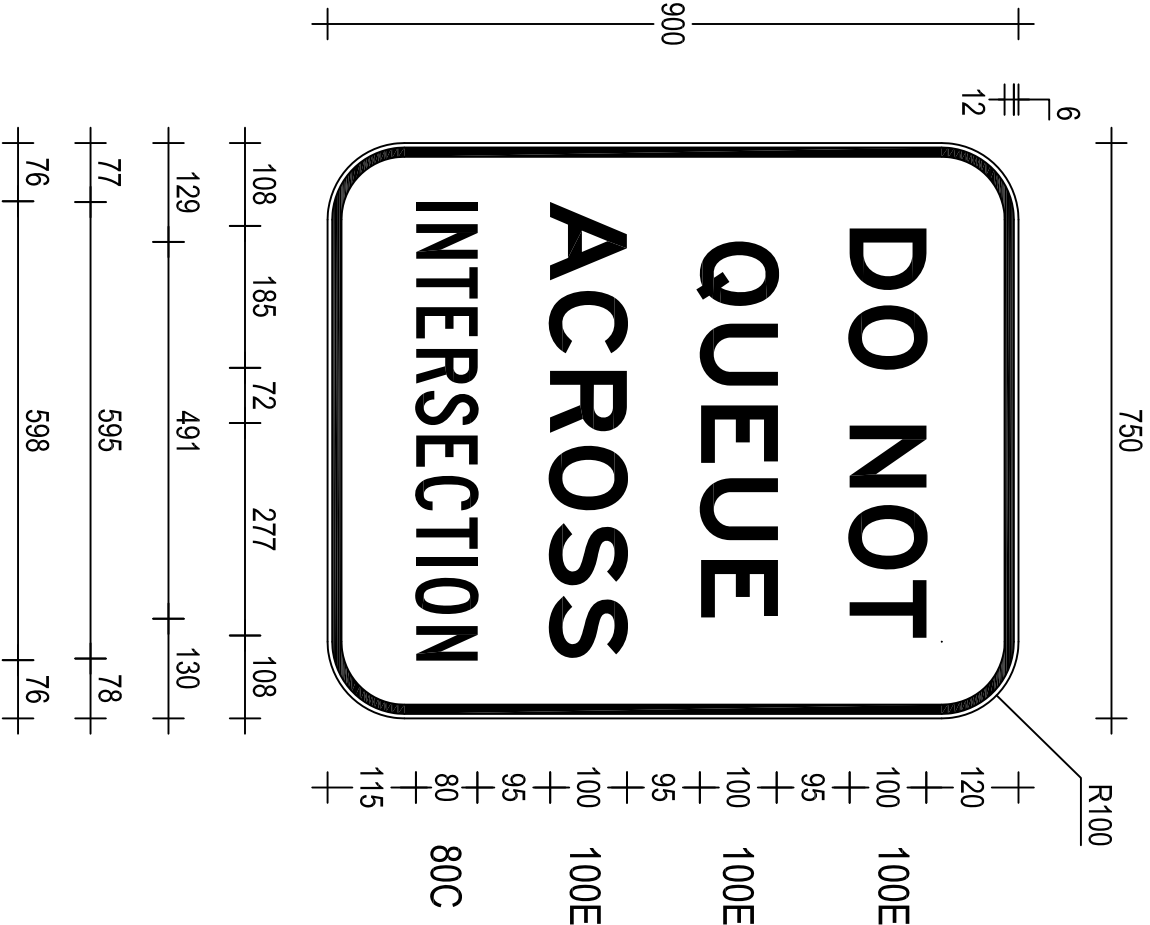

ACCEPTED FOR CONSTRUCTION