
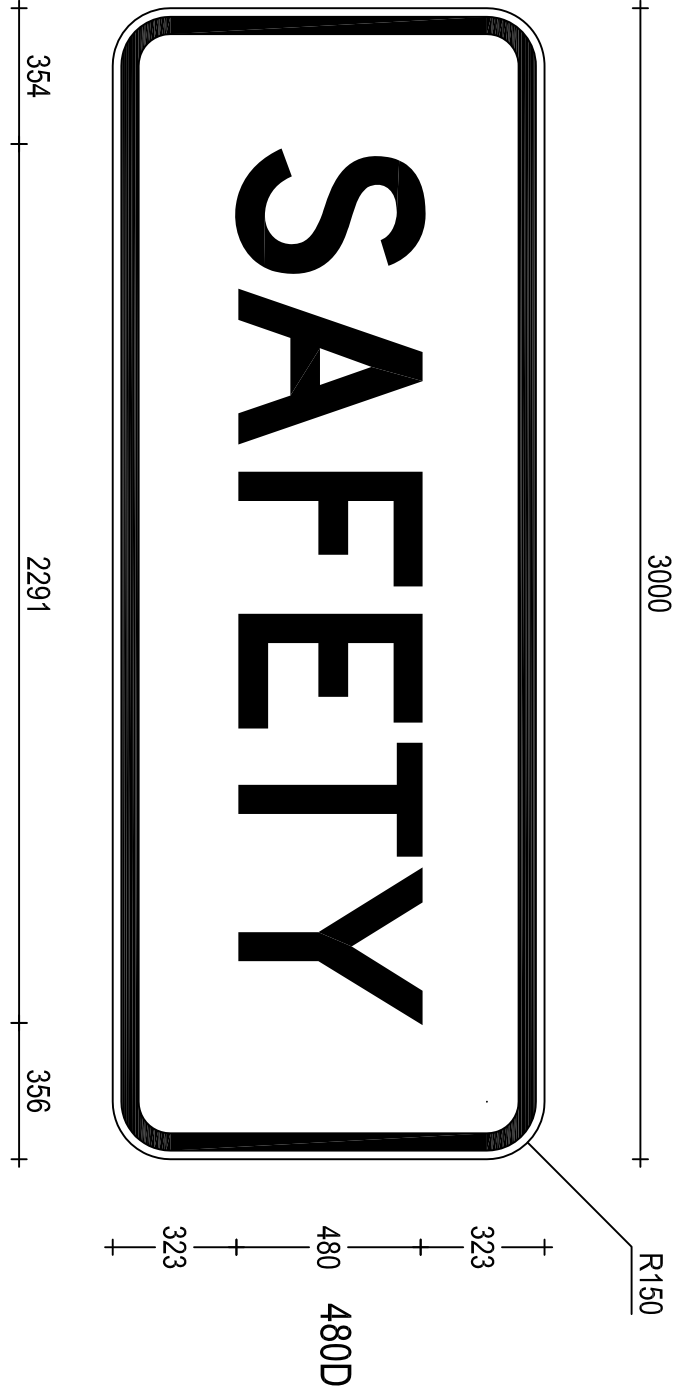


OR CODE	Scan to Check Document Version	REV	DATE	AMENDMENT / REVISION DESCRIPTION	APPROVAL	DRAWING FILE LOCATION / NAME: H:\SIGN\TTT\DRAWINGS\PLOT\GUIDE\G9-27.DWG
		01	23-03-18	AS Forms & material classification revised	P. Oliver	
ALL DIMENSIONS ARE IN MILLIMETRES UNLESS OTHERWISE SPECIFIED						MATERIALS: ALUMINIUM SIGN BLACK LEGEND AND BORDER ON AS1906.1 CL.400 WHITE REFLECTORISED GROUND
SIGN TO BE MANUFACTURED IN ACCORDANCE WITH RMS QA SPECIFICATION 3400						DESIGNED NAME: M. Davies DATE: 24-3-21 REVIEWED NAME: J. Rozos DATE: 24-03-21
						VERIFIED NAME: P. Oliver TITLE: Manager, Guidance & Delineation DATE: 24-03-21
PREPARED BY GUIDANCE AND DELINEATION UNIT ADVANCED TECHNICAL SERVICES INFRASTRUCTURE AND PLACE						NSW GOVERNMENT Transport Roads & Maritime Services
GUIDE SIGN G9-27 SAFETY						A3
SCALE: 1:20						EDMS No. XXXXXXXXXX
						SHEET No. 1
						ISSUE 01
SHEET 1 OF 1						

ACCEPTED FOR CONSTRUCTION

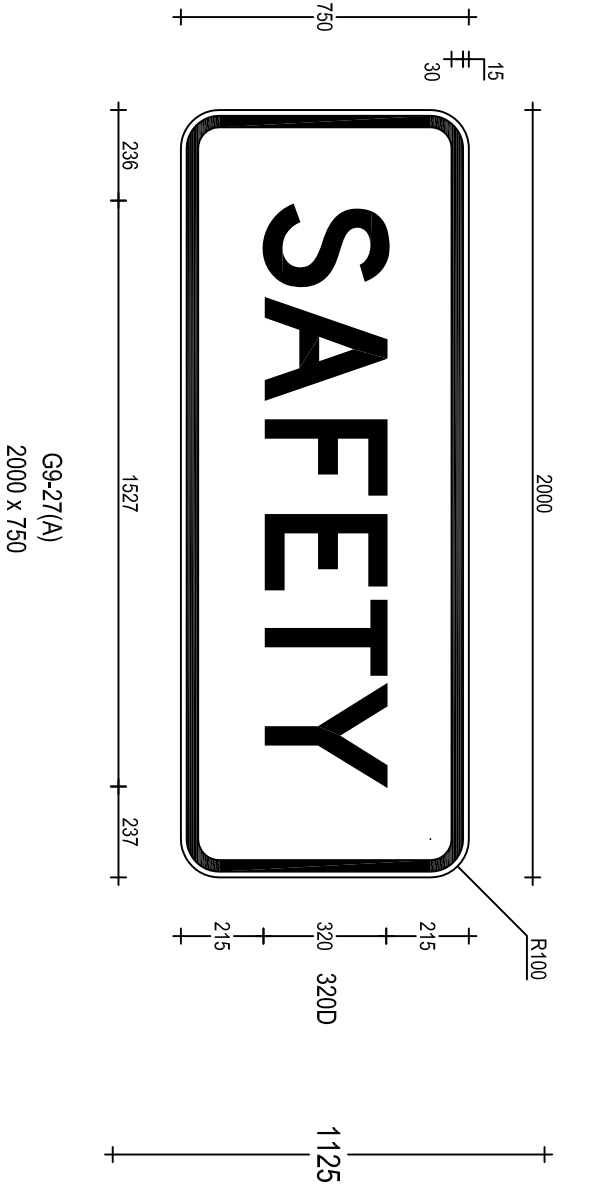

G9-27(B)
3000 x 1125