



OR CODE Scan to Check Document Version		REV 01	DATE 23-03-18	AMENDMENT / REVISION DESCRIPTION AS Forms & material classification revised	APPROVAL P. Oliver	DRAWING FILE LOCATION / NAME: H:\SIGN\TTT\DRAWINGS\PLOT\GUIDE\G9-36-1_R.DWG	DESIGNED NAME: M. Davies DATE: 24-3-21	VERIFIED NAME: P. Oliver TITLE: Manager, Guidance & Delineation DATE: 24-03-21	 NSW GOVERNMENT Transport Roads & Maritime Services PREPARED BY GUIDANCE AND DELINEATION UNIT ADVANCED TECHNICAL SERVICES INFRASTRUCTURE AND PLACE				GUIDE SIGN G9-36-1(R) SAFETY RAMP (ARROW ANGLED RIGHT)			A3	
ALL DIMENSIONS ARE IN MILLIMETRES UNLESS OTHERWISE SPECIFIED							SIGN TO BE MANUFACTURED IN ACCORDANCE WITH RMS QA SPECIFICATION 3400	REVIEWED NAME: J. Rozos DATE: 24-03-21	SHEET 1 OF 1			EDMS No. XXXXXXXXXX	SHEET No. 1	ISSUE 01			

ACCEPTED FOR CONSTRUCTION

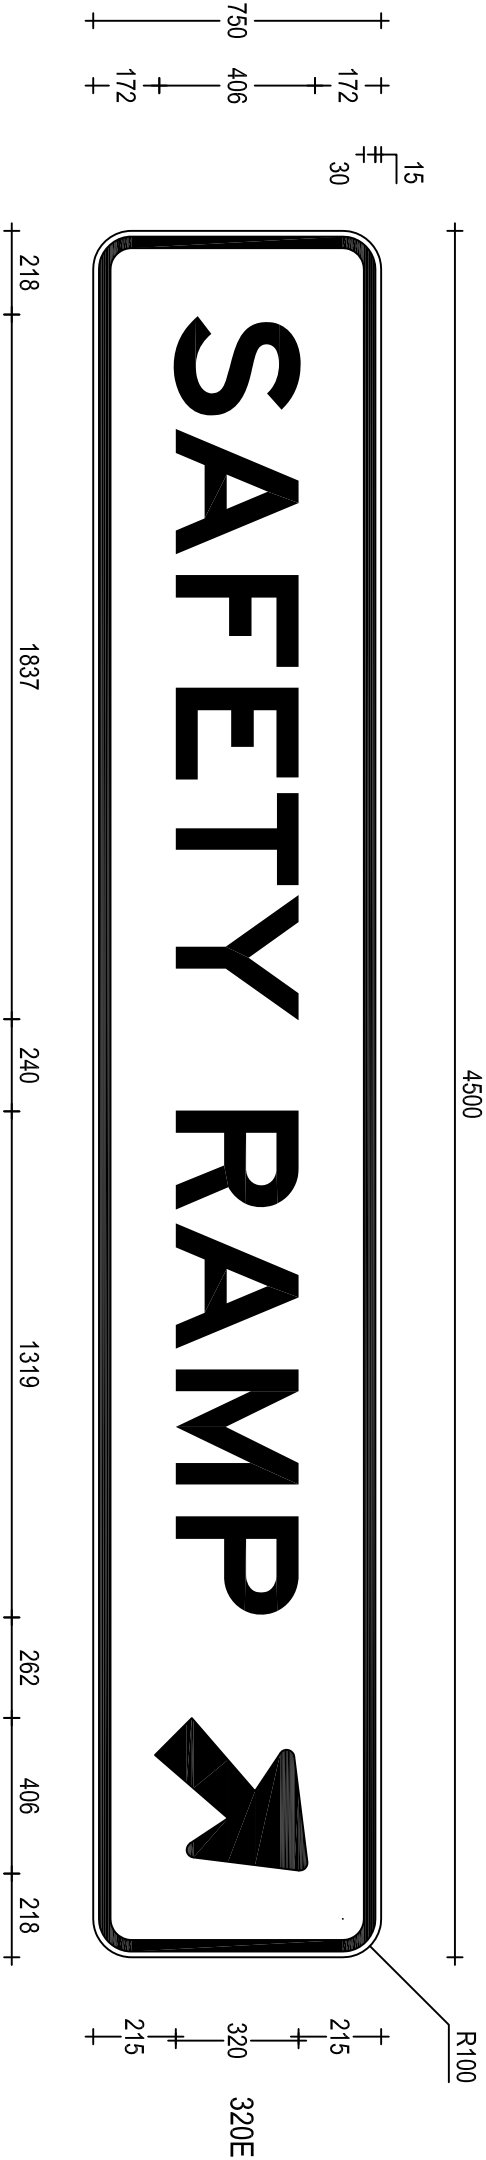

G9-36_1(R)
4500 x 750

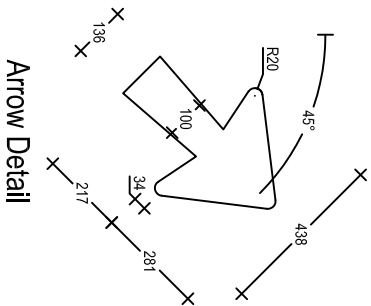

Arrow Detail