


OR CODE		Scan to Check Document Version	REV	DATE	AMENDMENT / REVISION DESCRIPTION	APPROVAL	DRAWING FILE LOCATION / NAME: H:\SIGN\TTP\DRAWINGS\PLOT\GUIDE\G9-36-2_LDWG	DESIGNED	VERIFIED	GUIDE SIGN G9-36-2(R) SAFETY RAMP (ARROW ANGLED RIGHT)			A3
			01	22-03-18	AS Forms & material classification revised	P. Oliver		NAME: M. Davies DATE: 24-3-21 REVIEWED NAME: J. Rozos DATE: 24-03-21	NAME: P. Oliver TITLE: Manager, Guidance & Delineation DATE: 24-03-21	NSW GOVERNMENT Transport Roads & Maritime Services			
								PREPARED BY GUIDANCE AND DELINEATION UNIT ADVANCED TECHNICAL SERVICES INFRASTRUCTURE AND PLACE		SHEET 1 OF 1			
										SCALE: 1:20			
										EDMS No. XXXXXXXXXX			
										SHEET No. 1			
										ISSUE 01			
										© Roads and Maritime Services			

G9-36_2(R)
2200 x 2000

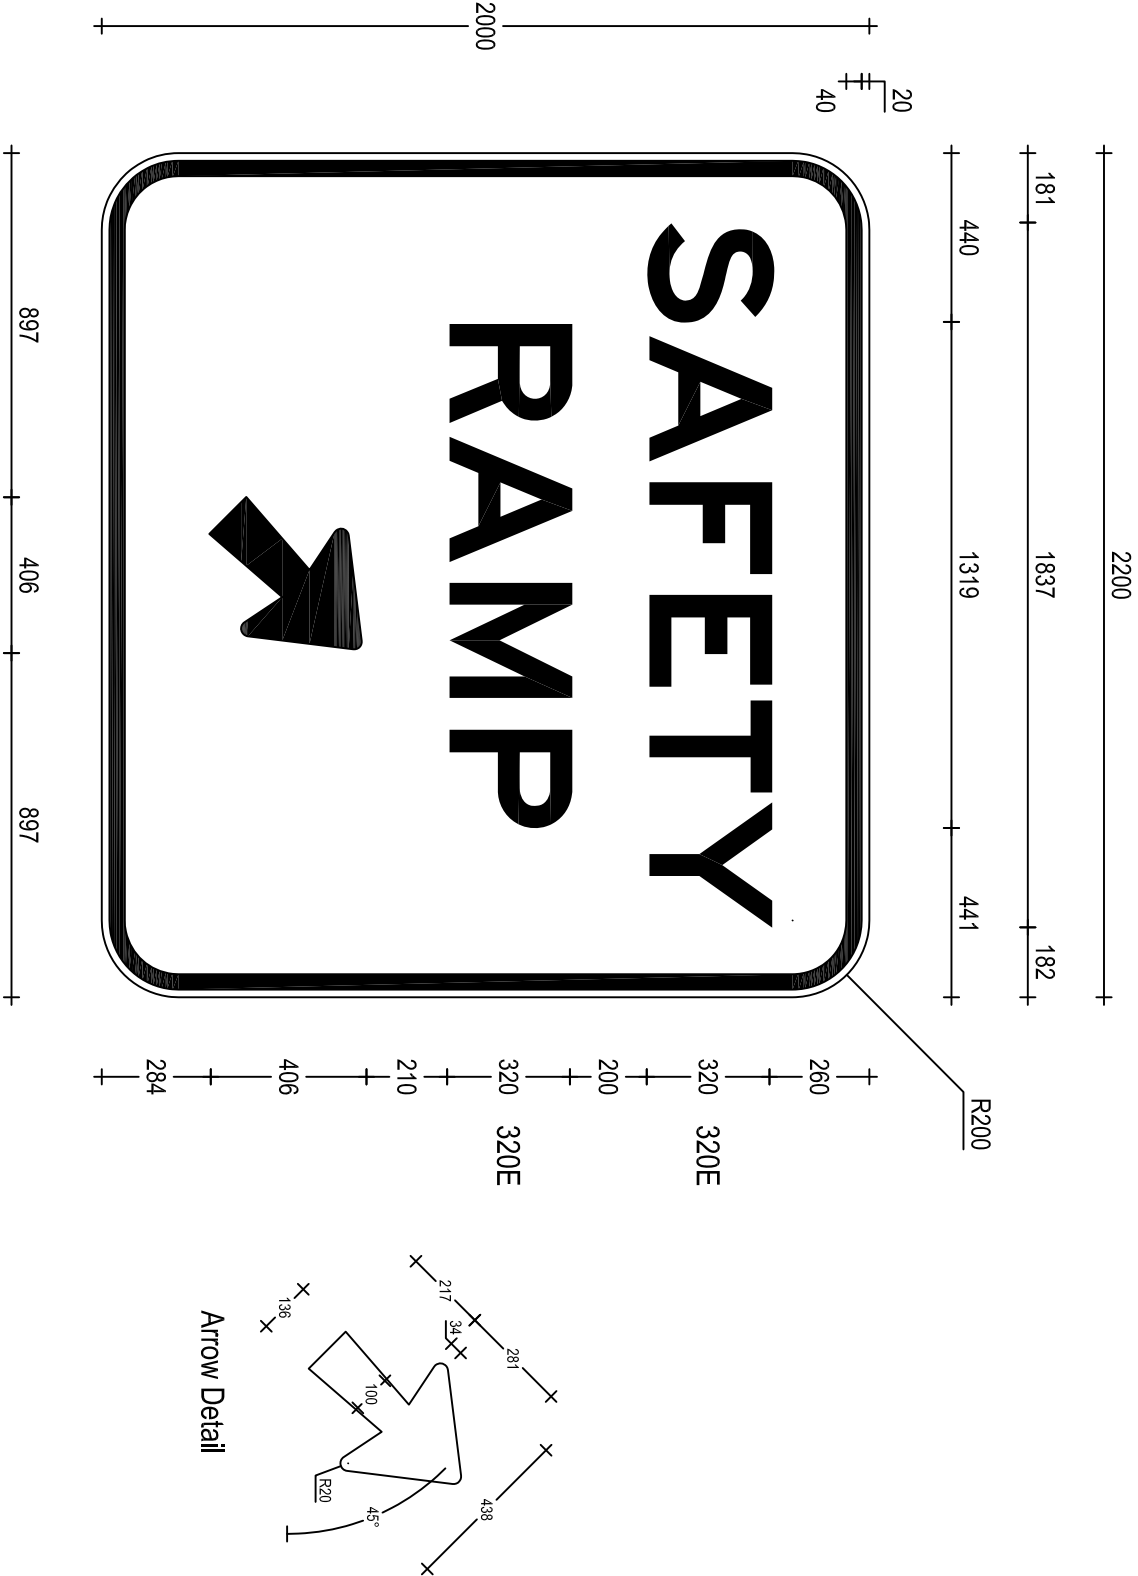

ACCEPTED FOR CONSTRUCTION