


OR CODE	Scan to Check Document Version	REV	DATE	AMENDMENT / REVISION DESCRIPTION	APPROVAL	DRAWING FILE LOCATION / NAME: H:\SIGN\TTT\DRAWINGS\PLOT\GUIDE\G9-37.DWG	DESIGNED	VERIFIED	PREPARED BY	GUIDE SIGN	A3
		01	23-03-18	AS Forms & material classification revised	P. Oliver		NAME: M. Davies DATE: 24-3-21	NAME: P. Oliver TITLE: Manager Guidance & Delineation DATE: 24-03-21	NSW GOVERNMENT Transport Roads & Maritime Services	G9-38 OVERTAKING LANE (x)km AHEAD	
						MATERIALS: ALUMINIUM SIGN BLACK LEGEND NUMERALS AND BORDER ON AS1906.1 CL.400 WHITE REFLECTORISED GROUND	REVIEWED NAME: J. Rozos DATE: 24-03-21		GUIDANCE AND DELINEATION UNIT ADVANCED TECHNICAL SERVICES INFRASTRUCTURE AND PLACE	SCALE: 1:15	EDMS No. XXXXXXXXXX
						SIGN TO BE MANUFACTURED IN ACCORDANCE WITH RMS QA SPECIFICATION 3400					SHEET 1 OF 1 ISSUE 01

ALL DIMENSIONS ARE IN MILLIMETRES UNLESS OTHERWISE SPECIFIED

SIGN TO BE MANUFACTURED IN ACCORDANCE WITH RMS QA SPECIFICATION 3400

G9-38
2600 x 1300
* varies

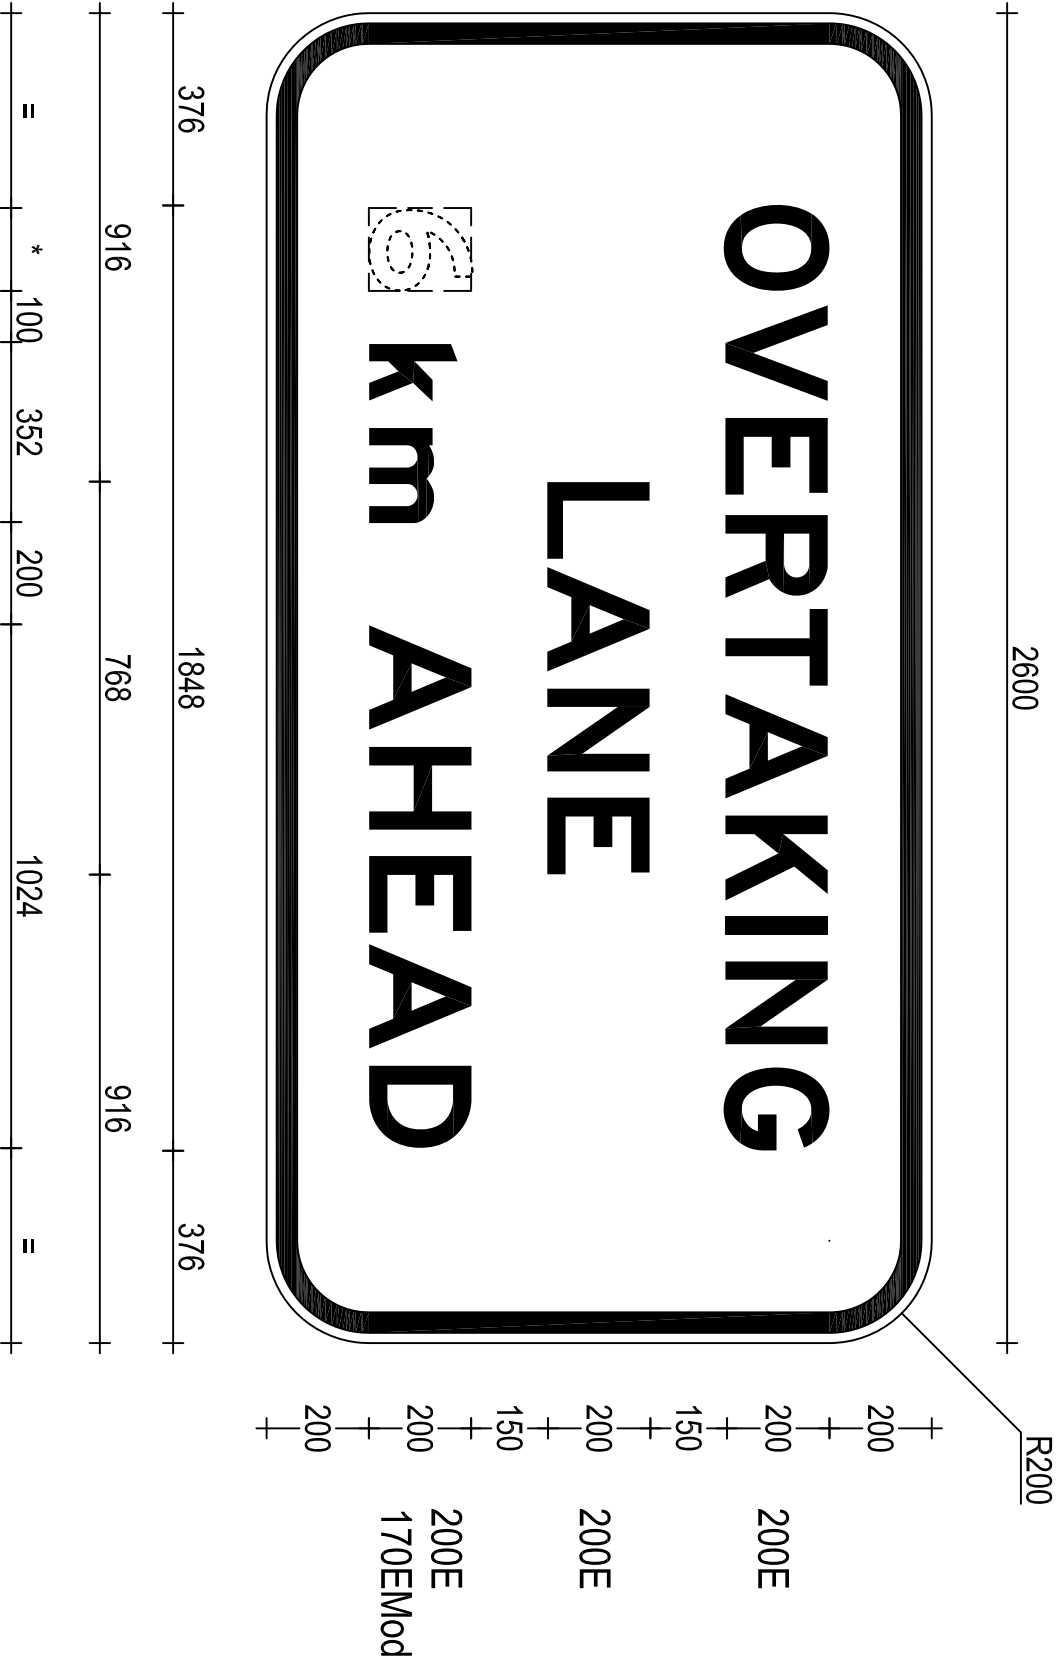

ACCEPTED FOR CONSTRUCTION