



OR CODE		Scan to Check Document Version		REV	DATE	AMENDMENT / REVISION DESCRIPTION	APPROVAL	DRAWING FILE LOCATION / NAME: H:\SIGN\ITTDRAWINGS\PLOT\GUIDE\G9-391n_L.DWG	DESIGNED	VERIFIED	GUIDE SIGN G9-391N_(L) U TURN BAY (LEFT ARROW)				A3			
				01	23-03-18	AS Forms & material classification revised	P. Oliver		NAME: M. Davies DATE: 24-3-21	NAME: P. Oliver TITLE: Manager, Guidance & Delineation DATE: 24-03-21	 NSW GOVERNMENT Transport Roads & Maritime Services				SHEET 1 OF 1			
							REVIEWED	NAME: J. Rozos DATE: 24-03-21										
ALL DIMENSIONS ARE IN MILLIMETRES UNLESS OTHERWISE SPECIFIED									SIGN TO BE MANUFACTURED IN ACCORDANCE WITH RMS QA SPECIFICATION 3400	PREPARED BY GUIDANCE AND DELINEATION UNIT ADVANCED TECHNICAL SERVICES INFRASTRUCTURE AND PLACE				SCALE: 1:10		EDMS No. XXXXXXXXXX	SHEET No. 1	ISSUE 01

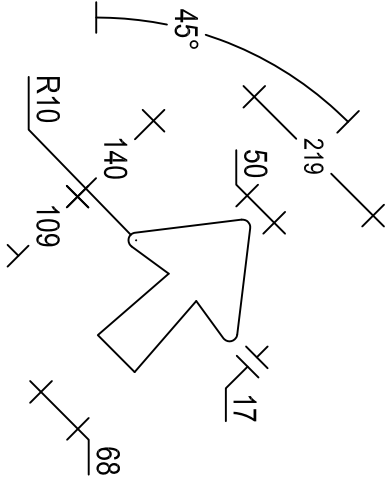

G9-391n_(L)
1700 x 720

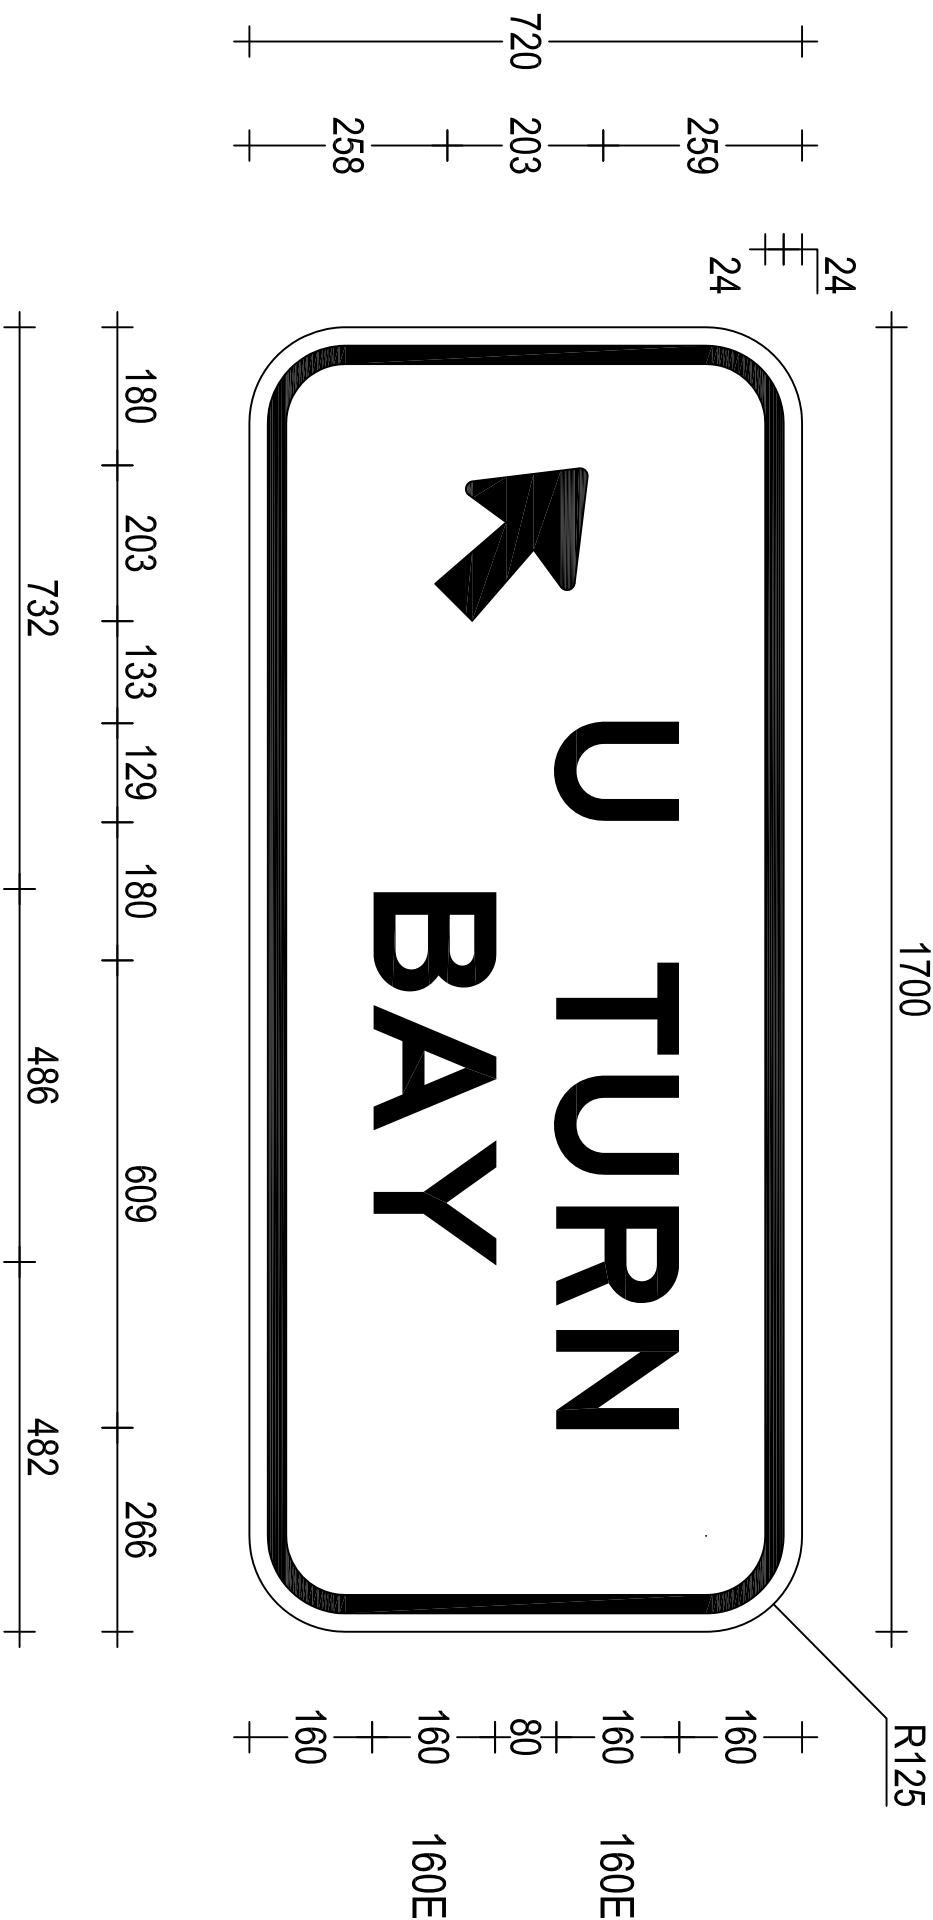

ACCEPTED FOR CONSTRUCTION