



|                                                              |                                   |          |                                            |                                  |          |   |                                              |                                                                             |                                                                |                          |                             |
|--------------------------------------------------------------|-----------------------------------|----------|--------------------------------------------|----------------------------------|----------|---|----------------------------------------------|-----------------------------------------------------------------------------|----------------------------------------------------------------|--------------------------|-----------------------------|
| OR CODE                                                      | Scan to Check<br>Document Version | REV      | DATE                                       | AMENDMENT / REVISION DESCRIPTION | APPROVAL | DRAWING FILE LOCATION / NAME: H:\SIGN\TTP\DRAWINGS\PLOT\GUIDE\G9-391n_A.DWG                                 | DESIGNED                                     | VERIFIED                                                                    | PREPARED BY                                                    | GUIDE SIGN               | A3                          |
|                                                              | 01                                | 23-03-18 | AS Forms & material classification revised | P. Oliver                        |          | MATERIALS: ALUMINIUM SIGN<br>BLACK LEGEND ARROW AND BORDER<br>ON AS1906.1 CL.400 WHITE REFLECTORISED GROUND | NAME: M. Davies<br>DATE: 24-3-21             | NAME: P. Oliver<br>TITLE: Manager, Guidance & Delineation<br>DATE: 24-03-21 | GOVERNMENT<br>NSW<br>Transport<br>Roads & Maritime<br>Services | G9-391N_(R)              |                             |
| ALL DIMENSIONS ARE IN MILLIMETRES UNLESS OTHERWISE SPECIFIED |                                   |          |                                            |                                  |          | SIGN TO BE MANUFACTURED IN ACCORDANCE WITH RMS QA SPECIFICATION 3400                                        | REVIEWED<br>NAME: J. Rozos<br>DATE: 24-03-21 |                                                                             | ADVANCED TECHNICAL SERVICES<br>INFRASTRUCTURE AND PLACE        | U TURN BAY (RIGHT ARROW) | SHEET 1 OF 1<br>SCALE: 1:10 |
|                                                              |                                   |          |                                            |                                  |          |   |                                              |                                                                             |                                                                | EDMS No.<br>XXXXXXXXXX   | ISSUE<br>01                 |

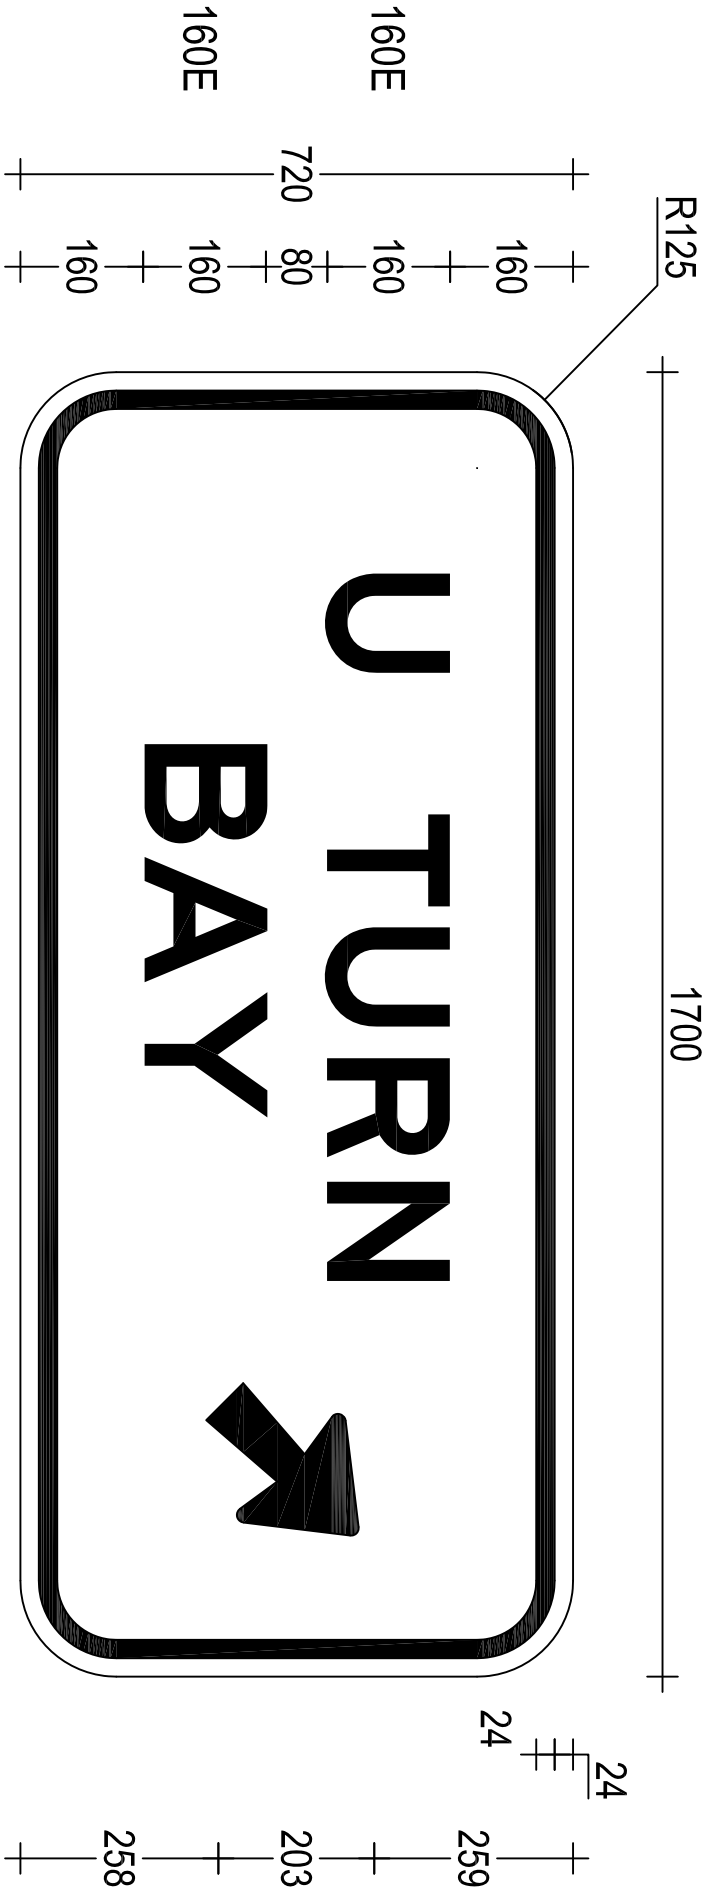

G9-391n\_(R)  
1700 x 720

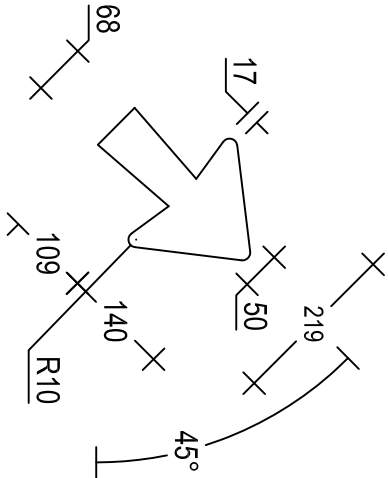

ACCEPTED FOR CONSTRUCTION