

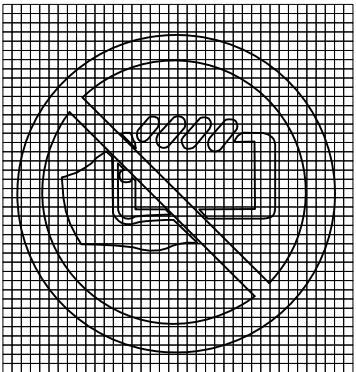
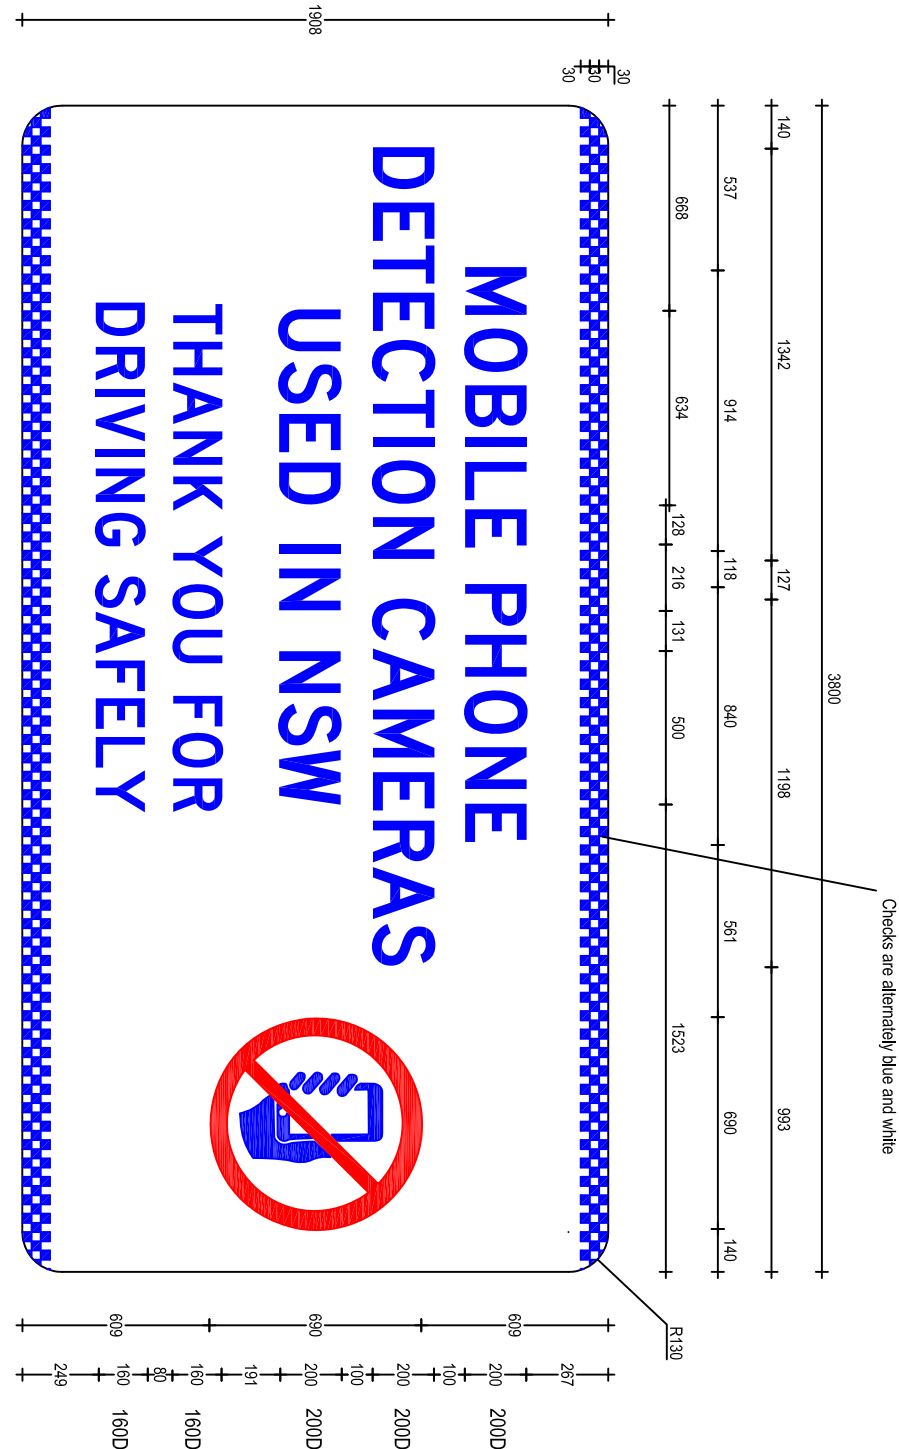


0	5	10	15	20	25	30	35	40	45	50
50mm ON A3 SIZE ORIGINAL										
OR CODE		Scan to Check Document Version	REV	DATE	AMENDMENT / REVISION DESCRIPTION	APPROVAL	DRAWING FILE LOCATION / NAME: H:\SIGNS\TTP\DRAWINGS\PLOT\GUIDE\G9-399\JWG			
			01	23-03-18	AS Forms & material classification revised	P. Oliver	MATERIALS: ALUMINIUM SIGN			
							AS1906.1 CL.400 BLUE LEGEND, SYMBOL AND CHECKS ON AS1906.1 CL.400 WHITE REFLECTORISED GROUND WITH AS1906.1 CL.400 RED REFL ANNULUS AND SLASH			
							SIGN TO BE MANUFACTURED IN ACCORDANCE WITH RMS QA SPECIFICATION 3400			
							DESIGNED			
							VERIFIED			
							PREPARED BY			
							GUIDANCE AND DELINEATION UNIT			
							TRAFFIC ENGINEERING SERVICES			
							TECHNICAL AND PROJECT SERVICES			
							SCALE: 1:25			
							EDMS No.			
							XXXXXXXXXX			
							SHEET No.			
							1			
							ISSUE			
							01			
							SHEET 1 OF 1			
							GUIDE SIGN			
							G9-399N			
							MOBILE PHONE DETECTION CAMERAS			
							A3			

ACCEPTED FOR CONSTRUCTION

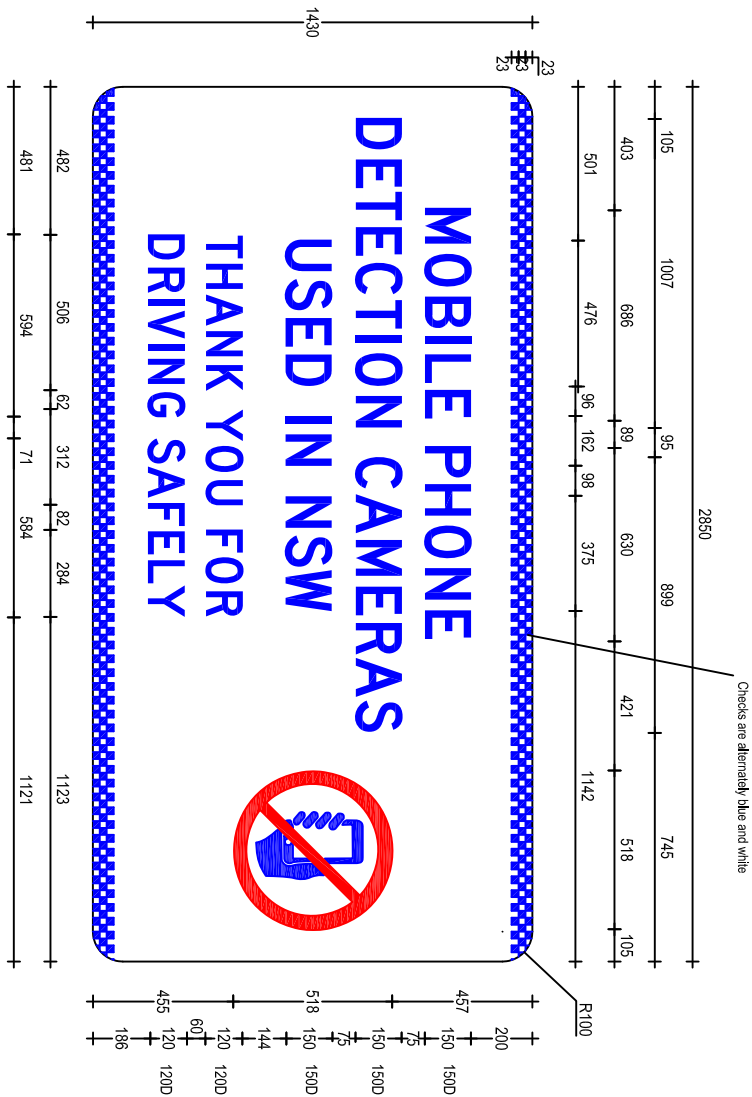

Not To Scale

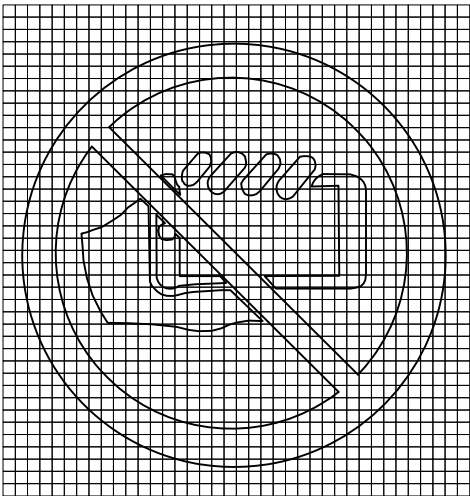

Not To Scale