


OR CODE	Scan to Check Document Version	REV	DATE	AMENDMENT / REVISION DESCRIPTION	APPROVAL	DRAWING FILE LOCATION / NAME: H:\SIGN\TTT\DRAWINGS\PLOT\GUIDE\G9-40-2.DWG
		01	23-03-18	AS Forms & material classification revised	P. Oliver	
ALL DIMENSIONS ARE IN MILLIMETRES UNLESS OTHERWISE SPECIFIED						SIGN TO BE MANUFACTURED IN ACCORDANCE WITH RMS QA SPECIFICATION 3400
DESIGNED						NAME ... M. Davies DATE ... 24-3-21
REVIEWED						NAME ... J. Rozos DATE ... 24-03-21
VERIFIED						NAME ... P. Oliver TITLE ... Manager, Guidance & Delineation DATE ... 24-03-21
PREPARED BY						NSW GOVERNMENT Transport Roads & Maritime Services
GUIDANCE AND DELINEATION UNIT ADVANCED TECHNICAL SERVICES INFRASTRUCTURE AND PLACE						
GUIDE SIGN G9-40-2 LOCAL TRAFFIC ONLY (ROADWORKS)						SCALE: 1:10
SHEET 1 OF 1						EDMS No. XXXXXXXXXX
						SHEET No. 1
						ISSUE 01
						A3

ACCEPTED FOR CONSTRUCTION

G9-40-2(A)
900 x 600

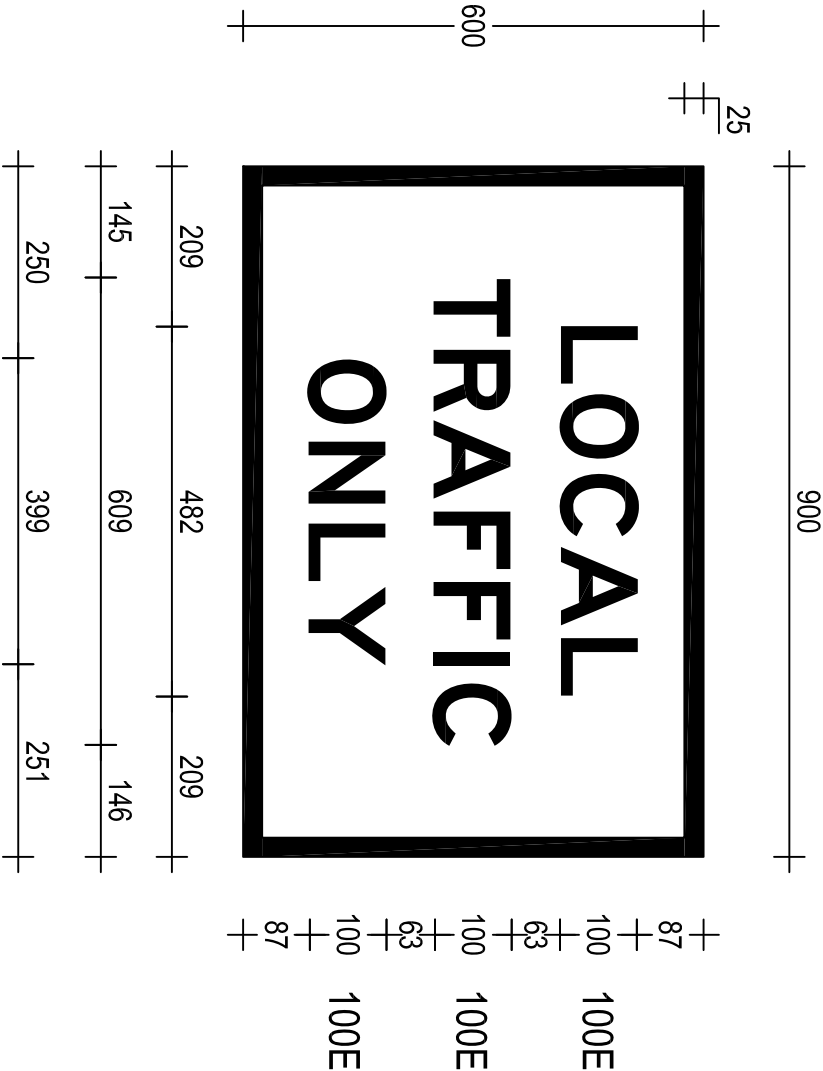

G9-40-2(B)
1200 x 900

