


0	5	10	15	20	25	30	35	40	45	50mm ON A3 SIZE ORIGINAL
---	---	----	----	----	----	----	----	----	----	--------------------------

OR CODE	Scan to Check Document Version	REV	DATE	AMENDMENT / REVISION DESCRIPTION	APPROVAL	DRAWING FILE LOCATION / NAME: H:\SIGN\TTT\DRAWINGS\PLOT\GUIDE\G9-5-1_R.DWG
		01	23-09-18	AS Forms & material classification revised	P. Oliver	
ALL DIMENSIONS ARE IN MILLIMETRES UNLESS OTHERWISE SPECIFIED						SIGN TO BE MANUFACTURED IN ACCORDANCE WITH RMS QA SPECIFICATION 3400
MATERIALS: ALUMINIUM SIGN BLACK LEGEND CHEVRON AND BORDER ON AS1906.1 CL.400 WHITE REFLECTORISED GROUND						
DESIGNED						
SIGNED . M. Davies						
NAME .						
DATE . 30-7-19						
REVIEWED						
SIGNED . J. Rozos						
NAME .						
DATE . 30-7-19						
VERIFIED						
SIGNED .						
NAME . P. Oliver						
TITLE . Manager, Guidance & Delineation						
DATE . 30-7-19						
PREPARED BY						
GUIDANCE AND DELINEATION UNIT						
TRAFFIC ENGINEERING SERVICES						
TECHNICAL AND PROJECT SERVICES						
GUIDE SIGN						A3
G9-5-1(R)						
DETOUR FOR HIGH VEHICLES(RIGHT)						
SCALE: 1:10						
EDMS No. XXXXXXXXXX						
SHEET No. 1						
ISSUE 01						
SHEET 1 OF 1						

ACCEPTED FOR CONSTRUCTION

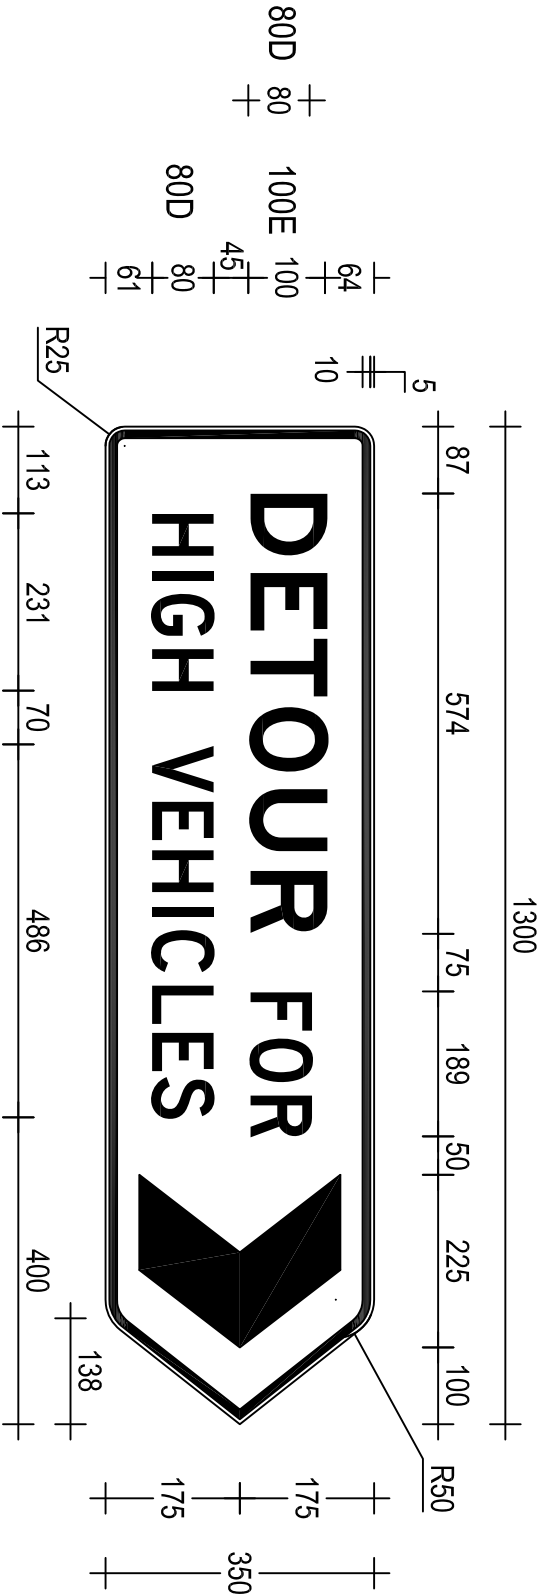

G9-5-1(R)
1300 x 350

