


OR CODE	Scan to Check Document Version	REV	DATE	AMENDMENT / REVISION DESCRIPTION	APPROVAL	DRAWING FILE LOCATION / NAME: H:\SIGN\T\T\DRAWINGS\PLOT\GUIDE\G9-80-2.DWG
		01	23-03-18	AS Forms & material classification revised	P.Oliver	
ALL DIMENSIONS ARE IN MILLIMETRES UNLESS OTHERWISE SPECIFIED						SIGN TO BE MANUFACTURED IN ACCORDANCE WITH RMS QA SPECIFICATION 3400
DESIGNED						NAME : M.Davies DATE : 24-3-21
VERIFIED						NAME : P.Oliver TITLE : Manager, Guidance & Delineation DATE : 24-03-21
PREPARED BY						GUIDANCE AND DELINEATION UNIT ADVANCED TECHNICAL SERVICES INFRASTRUCTURE AND PLACE
GUIDE SIGN						SCALE: 1:20
G9-80-2						EDMS No. XXXXXXXXXX
ON RIGHT						SHEET No. 1
						ISSUE 01
						SHEET 1 OF 1
						A3

ACCEPTED FOR CONSTRUCTION

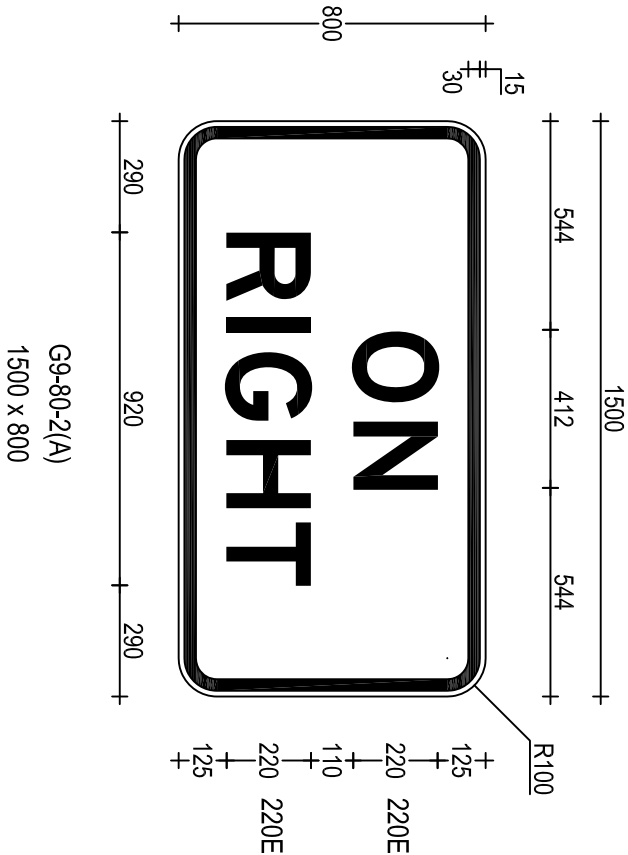

G9-80-2(B)
3000 x 1600