


50mm ON A3 SIZE ORIGINAL

OR CODE			Scan to Check Document Version		REV	DATE	AMENDMENT / REVISION DESCRIPTION	APPROVAL	DRAWING FILE LOCATION / NAME: H:\SIGNS\TTT\DRAWINGS\PI\OTREGULAT\R29.DWG		DESIGNED	VERIFIED		REGULATORY SIGN R2-9(R) RIGHT LANE MUST TURN RIGHT		SHEET 1 OF 1		A	
					01	23-08-18	AS Fonts & material classification revised	P Oliver	MATERIALS: ALUMINIUM SIGN BLACK LEGEND AND BORDER ON AS1906.1 CL.400 WHITE REFLECTORISED GROUND		SIGNED M. Davies DATE 31-07-19	SIGNED P Oliver NAME DATE 31-07-19		TRANS ROADS & MARITIME SERVICES		EDMS No. XXXXXXXXXX		SHEET No. 1	
									SIGN TO BE MANUFACTURED IN ACCORDANCE WITH RMS QA SPECIFICATION 3400		REVIEWED J Rozos DATE 31-07-19	TITLE Manager Guidance & Delineation DATE 31-07-19		GUIDANCE AND DELINEATION UNIT TRAFFIC ENGINEERING SERVICES TECHNICAL AND PROJECT SERVICES		SCALE: 1:10		© Roads and Maritime Service	

ACCEPTED FOR CONSTRUCTION

R2-9A(R)
450 x 750

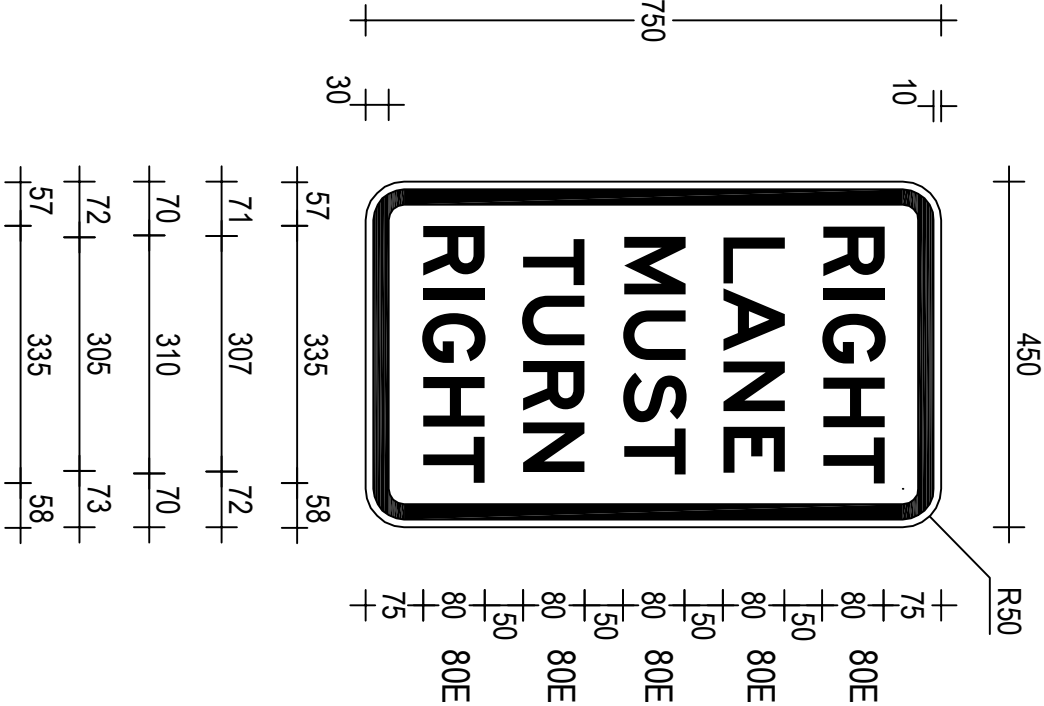

R2-9B(R)
600 x 1000

