
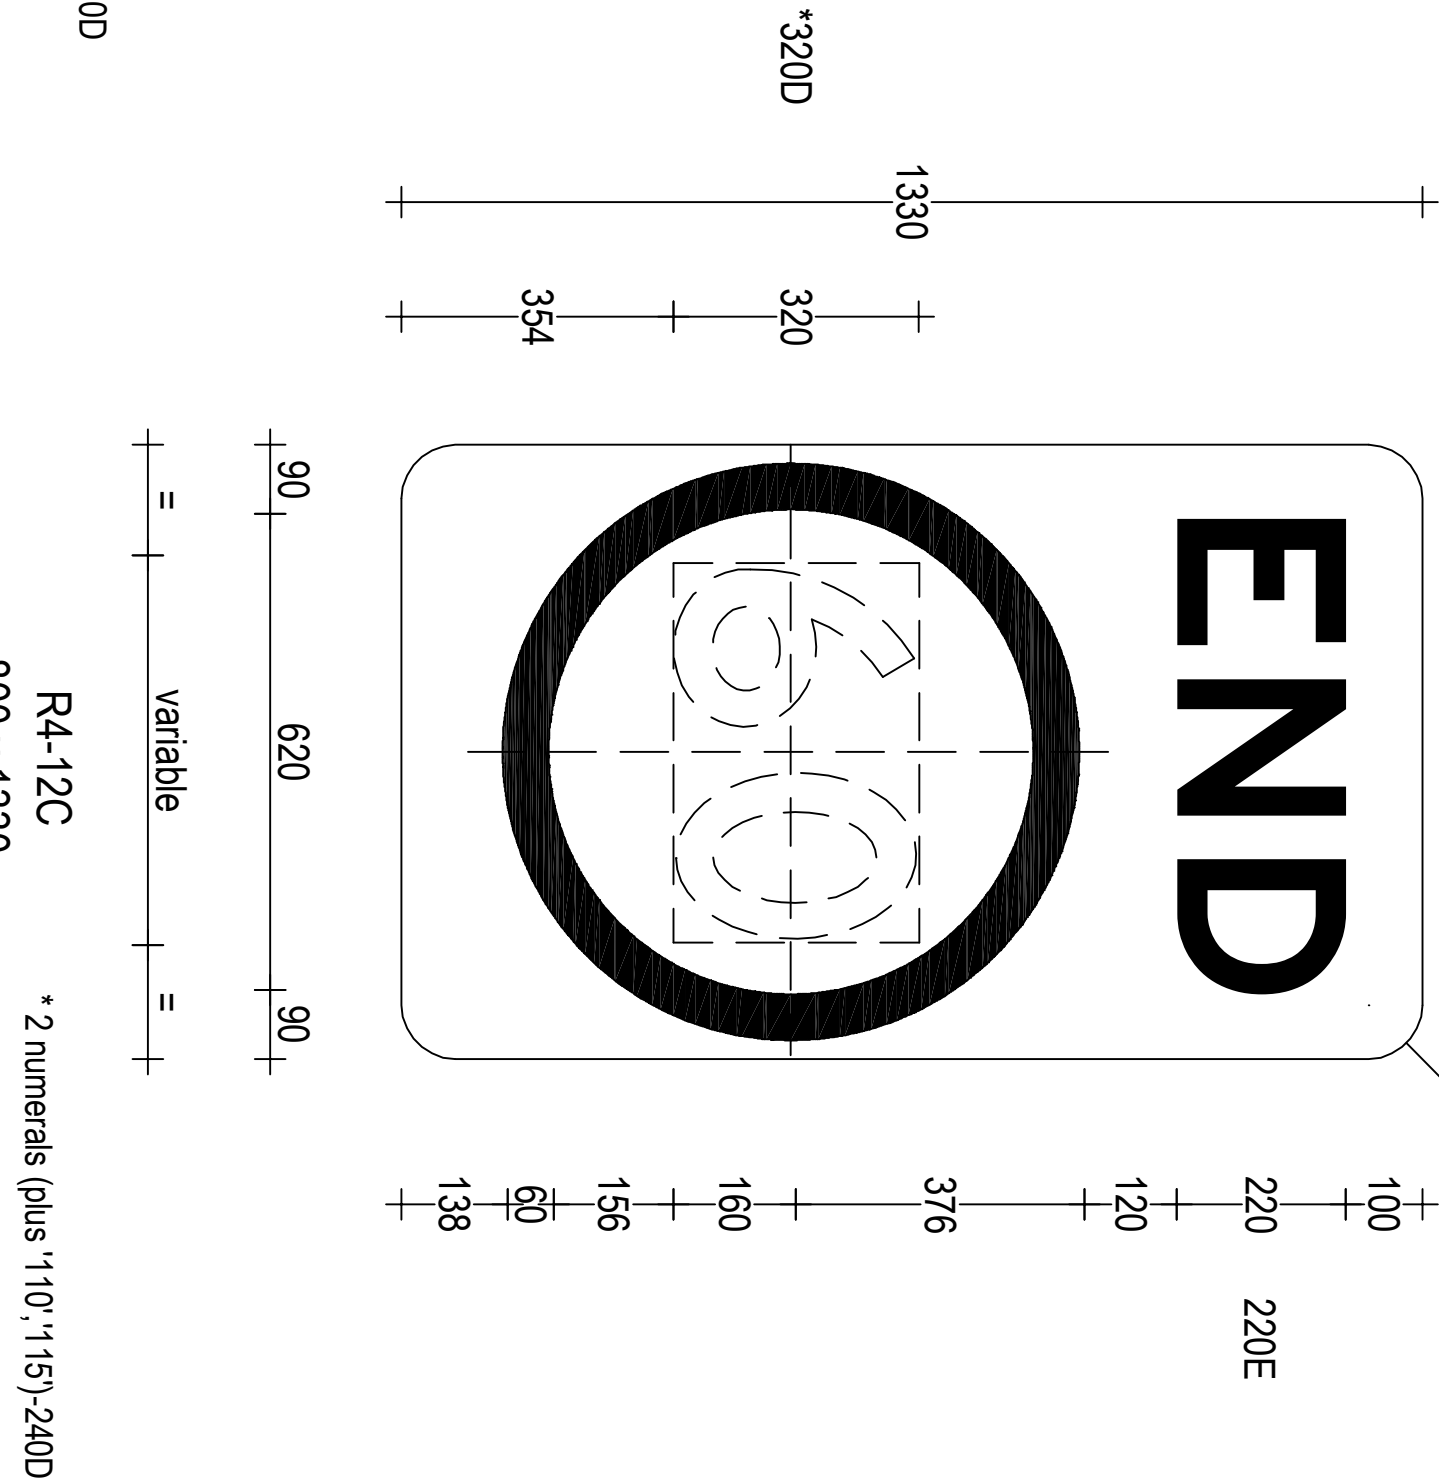


0 5 10 15 20 25 30 35 40 45 50mm ON A3 SIZE ORIGINAL

OR CODE		ISSUED TO CHECK DOCUMENT VERSION		REV	DATE	AMENDMENT / REVISION DESCRIPTION	APPROVAL	DRAWING FILE LOCATION / NAME: H:\SIGNS\TIDDAWAMUS\RA\OTRREGRA-12\DWG	DESIGNED	VERIFIED	REGULATORY SIGN R4-12 END SPEED LIMIT		SHEET 1 OF 1		A					
		01		23-06-18		AS Forms & material Classification revised	P Oliver	MATERIALS: ALUMINIUM SIGN BLACK LEGEND, NUMERAL AND ANNULUS ON AS1906.1 CL.400 WHITE REFLECTORISED GROUND	SIGNED NAME: M. Davies DATE: 31-07-19 REVIEWED NAME: J. Rozos DATE: 31-07-19	SIGNED NAME: P. Oliver TITLE: Manager, Guidance & Delineation DATE: 31-07-19	 Transport Roads & Maritime Services PREPARED BY GUIDANCE AND DELINEATION UNIT TRAFFIC ENGINEERING SERVICES TECHNICAL AND PROJECT SERVICES		SCALE: 1:10		EDMS No. XXXXXXXXXX		SHEET No. 1		ISS 0	
ALL DIMENSIONS ARE IN MILLIMETRES UNLESS OTHERWISE SPECIFIED									SIGN TO BE MANUFACTURED IN ACCORDANCE WITH RMS QA SPECIFICATION 3400											

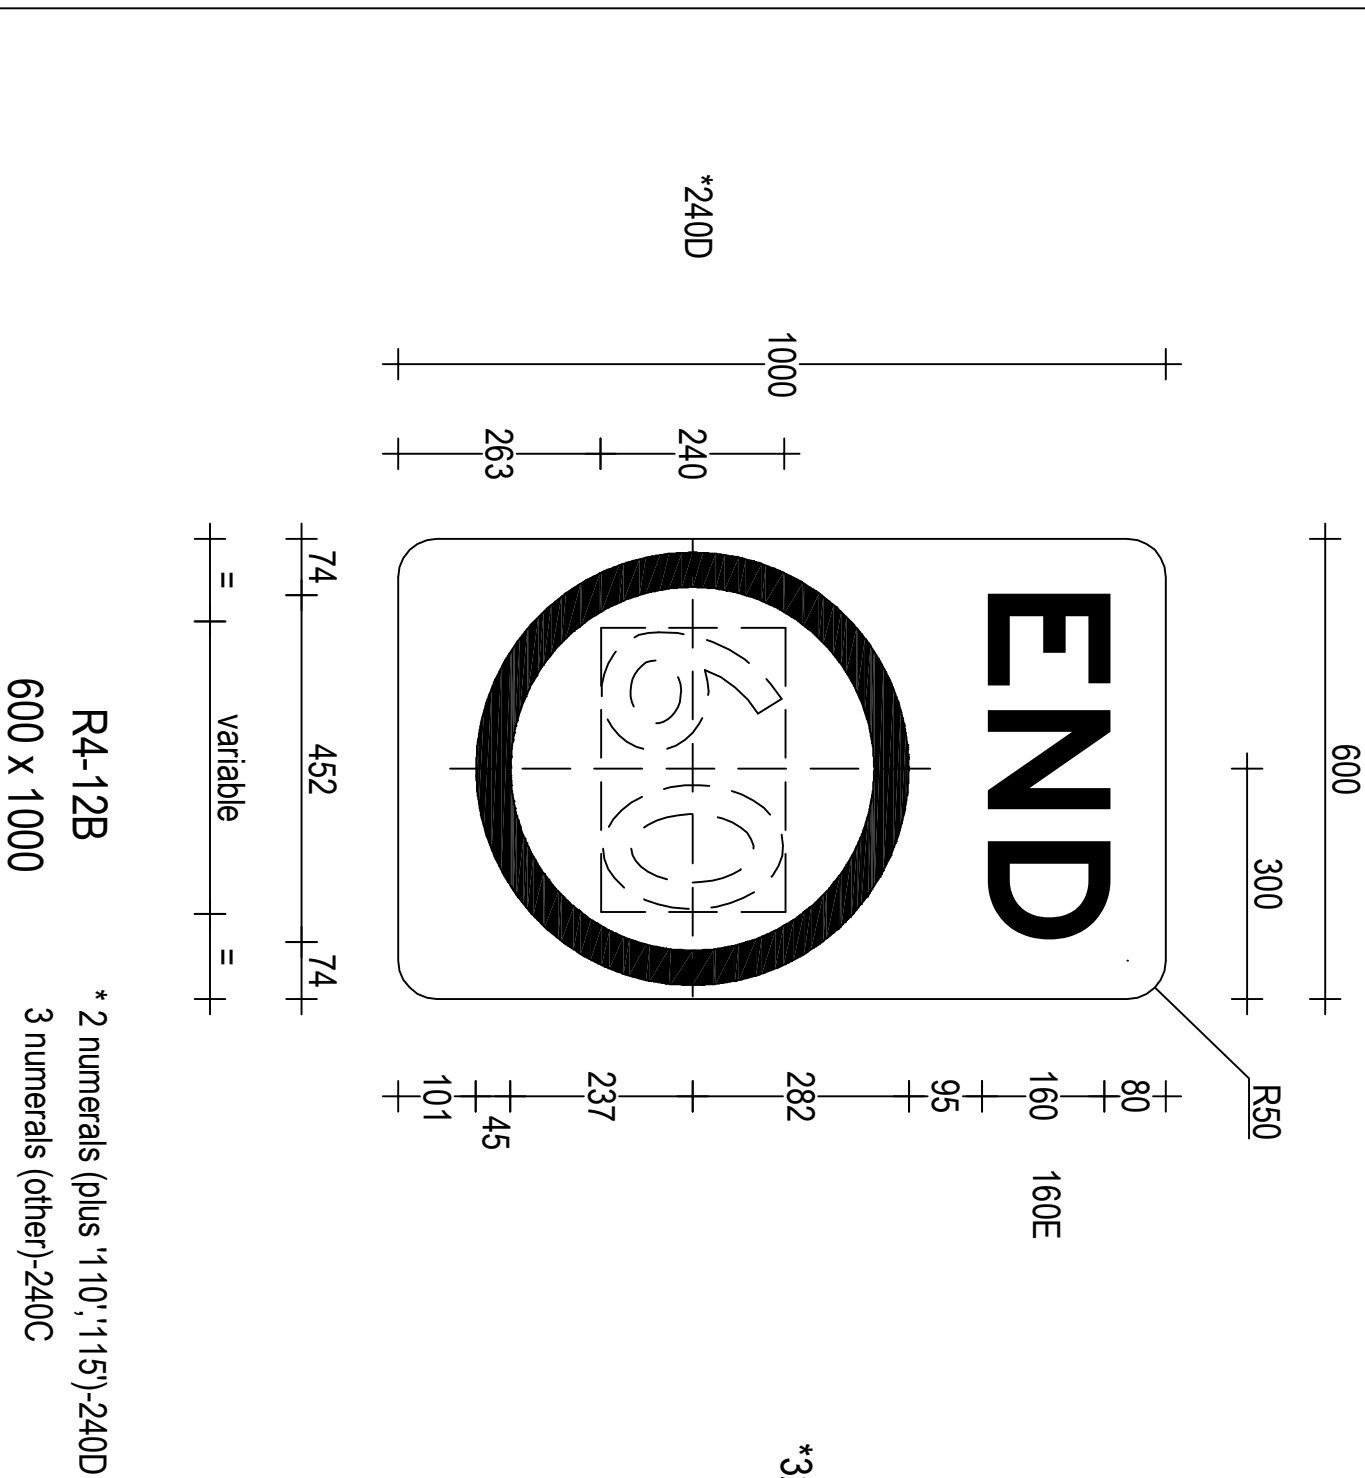

ACCEPTED FOR CONSTRUCTION