


OR CODE		Scan to Check Document Version		REV	DATE	AMENDMENT / REVISION DESCRIPTION	APPROVAL	DRAWING FILE LOCATION / NAME: H:\SIGN\ITTDRAWINGS\PLOT\REGULATR4-201-3n.DWG	DESIGNED	VERIFIED	REGULATORY SIGN		A3		
				01	23-03-18	AS Forms & material classification revised	P. Oliver		NAME M.Davies DATE 31-07-19	NAME P. Oliver TITLE Manager, Guidance & Delineation DATE 31-07-19	R4-201-3n WINDING ROAD				
MATERIALS: ALUMINIUM SIGN BLACK LEGEND AND BORDER ON AS1906.1 CL.400 WHITE REFLECTORISED GROUND									REVIEWED	SHEET 1 OF 1					
									NAME J.Rozos DATE 31-07-19						
ALL DIMENSIONS ARE IN MILLIMETRES UNLESS OTHERWISE SPECIFIED									SIGN TO BE MANUFACTURED IN ACCORDANCE WITH RMS QA SPECIFICATION 3400					SCALE: 1:15	
									PREPARED BY GUIDANCE AND DELINEATION UNIT TRAFFIC ENGINEERING SERVICES TECHNICAL AND PROJECT SERVICES					EDMS No. XXXXXXXXXX	
														SHEET No. 1	
														ISSUE 01	
© Roads and Maritime Services															

ACCEPTED FOR CONSTRUCTION

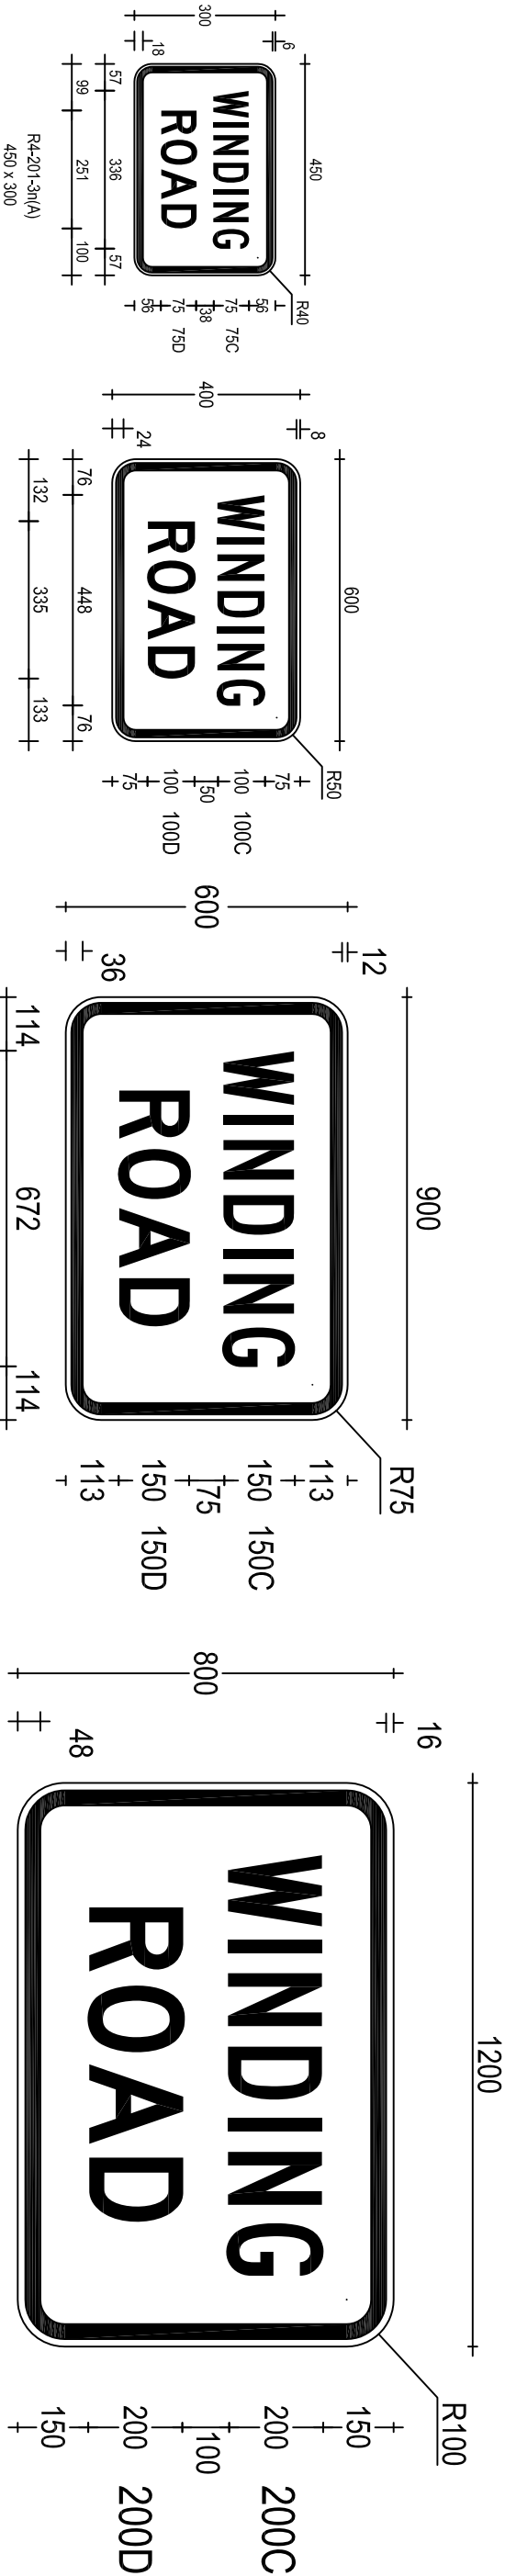

R4-201-3n(C)
900 X 600

R4-201-3n(D)
1200 X 800