



R5-41-2 Example

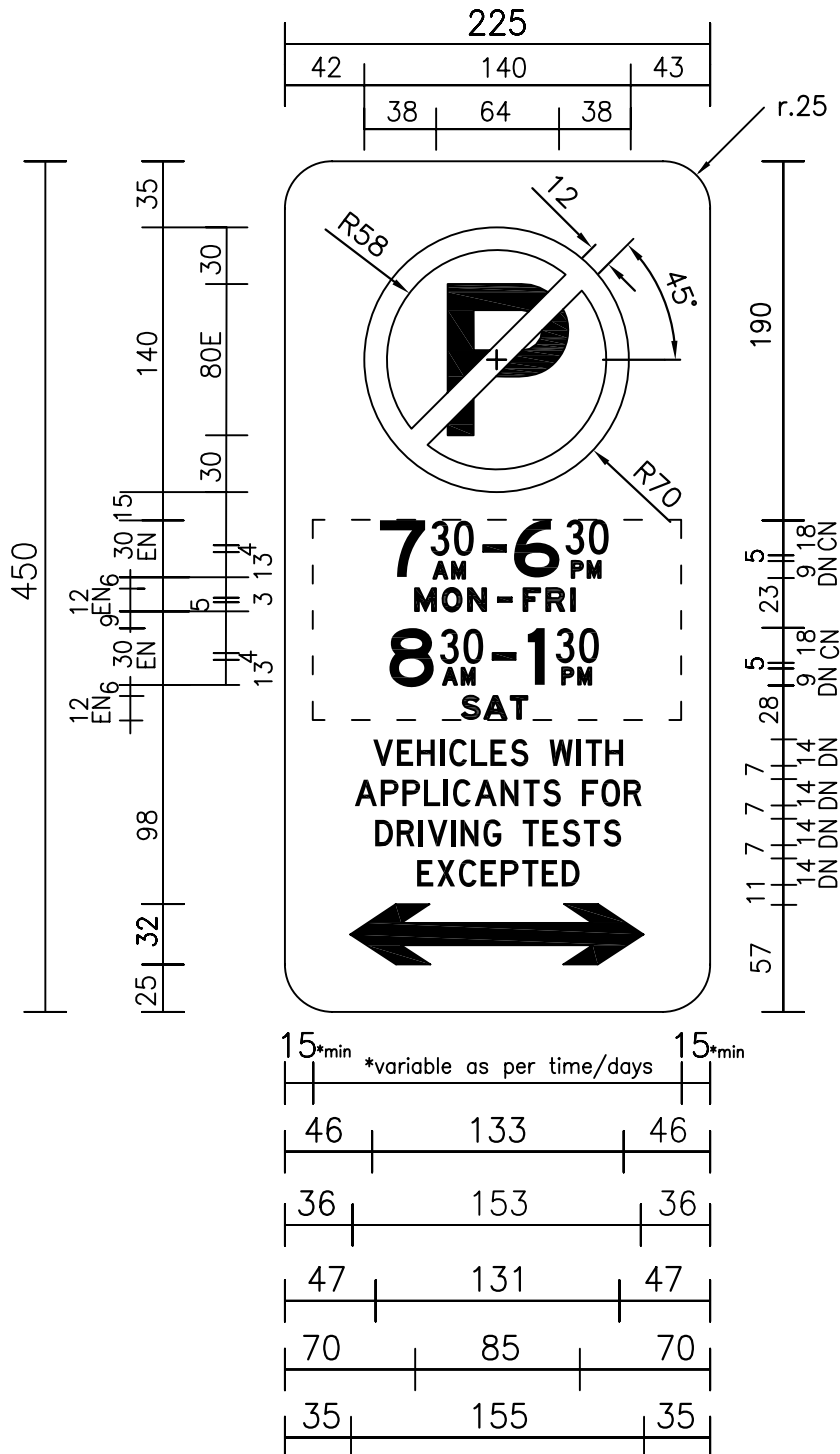

Red letters, numerals, arrow, annulus & slash,
black letter P, on white ground.

Detail of Arrow Adapt arrows L, R or LR to suit

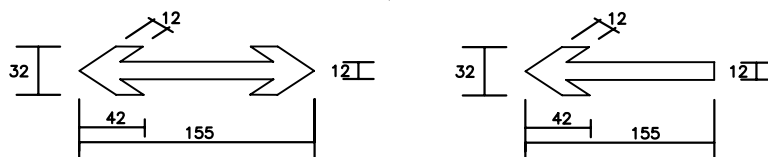

SCALE 1:5

TITLE

REGULATORY SIGN R5-41-2

Drawn: VC 13.02.13

CHKD: FR 14.02.13



GUIDANCE AND DELINEATION UNIT
27-31 ARGYLE ST, PARRAMATTA 2150

H:\SIGNS\TTT\DRAWINGS\PLOT\REGULAT\ R5-41-2.DWG

Revision: -