



QR CODE		Scan to Check Document Version	REV	DATE	AMENDMENT / REVISION DESCRIPTION	APPROVAL	DRAWING FILE LOCATION / NAME: H:\SIGNS\TTP\DRAWINGS\PI\OTREG\LATR6-15.DWG	
			01	23-08-18	AS Fonts & material classification revised	P. Oliver		
		MATERIALS: ALUMINIUM SIGN BLACK SYMBOL ON AS1906.1 CL.400 WHITE REFLECTORISED GROUND WITH AS1906.1 CL.400 RED REFL ANNULUS & BAR						
		SIGN TO BE MANUFACTURED IN ACCORDANCE WITH RMS QA SPECIFICATION 3400						
		DESIGNED		VERIFIED				
		SIGNED: 		SIGNED: 				
		NAME: M. Davies		NAME: P. Oliver				
		DATE: 31-07-19		DATE: 31-07-19				
		REVIEWED		TITLE: Manager, Guidance & Delineation				
		SIGNED: 		DATE: 31-07-19				
		NAME: J. Rozos						
		DATE: 31-07-19						
		 Transport Roads & Maritime Services						
		PREPARED BY GUIDANCE AND DELINEATION UNIT TRAFFIC ENGINEERING SERVICES TECHNICAL AND PROJECT SERVICES						
		REGULATORY SIGN R6-15 PEDESTRIANS PROHIBITED (SYMBOLIC)						
		SHEET 1 OF 1						
		SCALE: 1:15						
		EDMS No. XXXXXXXXXX						
		SHEET No. 1						
		ISS 0						

© Roads and Maritime Service


ACCEPTED FOR CONSTRUCTION

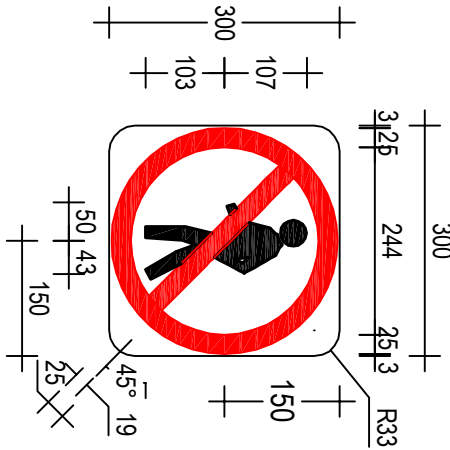


R6-15(A)
300 x 300

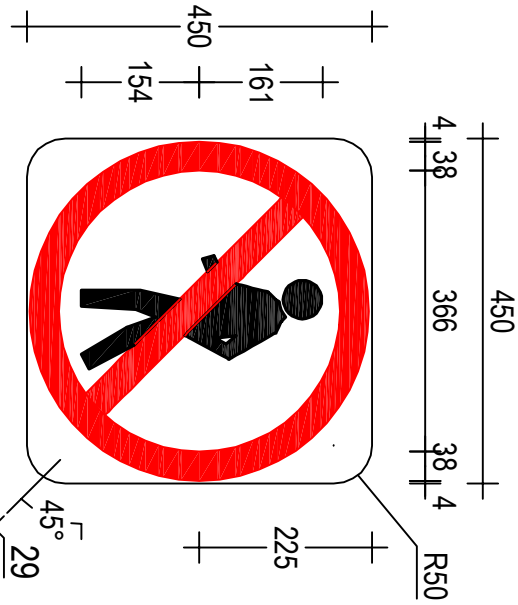

R6-15(B)
450 x 450

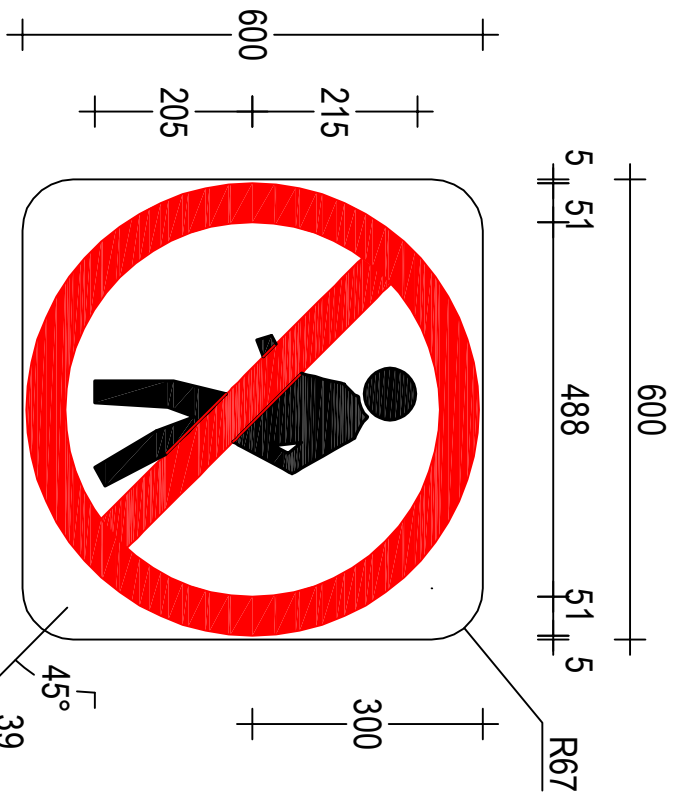

R6-15n(C)
600 x 600

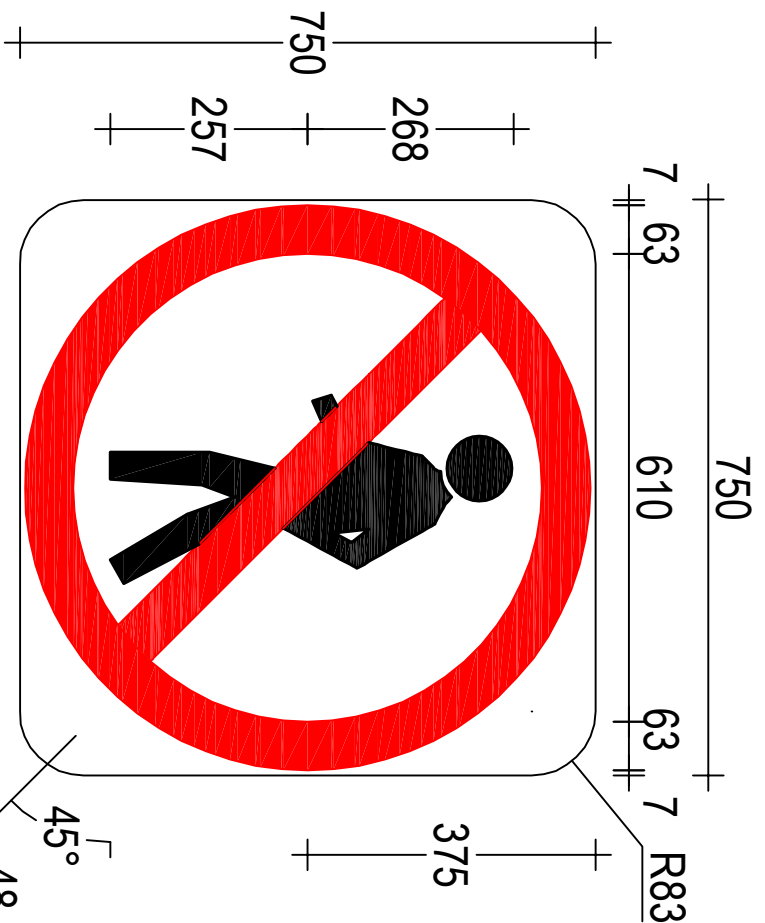

R6-15n(D)
750 x 750

