



OR CODE	Scan to Check Document Version	REV	DATE	AMENDMENT / REVISION DESCRIPTION	APPROVAL	DRAWING FILE LOCATION / NAME: H:\SIGN\ITTT\DRAWINGS\PLOT\REGULATR6-22.DWG	DESIGNED	VERIFIED	PREPARED BY	REGULATORY SIGN	A3
		01	23-03-18	AS Forms & material classification revised	P. Oliver		SIGNED: M. Davies NAME: M. Davies DATE: 31-07-19	SIGNED: P. Oliver NAME: P. Oliver TITLE: Manager, Guidance & Delineation DATE: 31-07-19	NSW GOVERNMENT Transport Roads & Maritime Services	R6-22 TRUCKS & BUSES MUST USE LOW GEAR	SHEET 1 OF 1
ALL DIMENSIONS ARE IN MILLIMETRES UNLESS OTHERWISE SPECIFIED						SIGN TO BE MANUFACTURED IN ACCORDANCE WITH RMS QA SPECIFICATION 3400	SCALE: 1:20		EDMS No. XXXXXXXXXX	SHEET No. 1	ISSUE 01


ACCEPTED FOR CONSTRUCTION

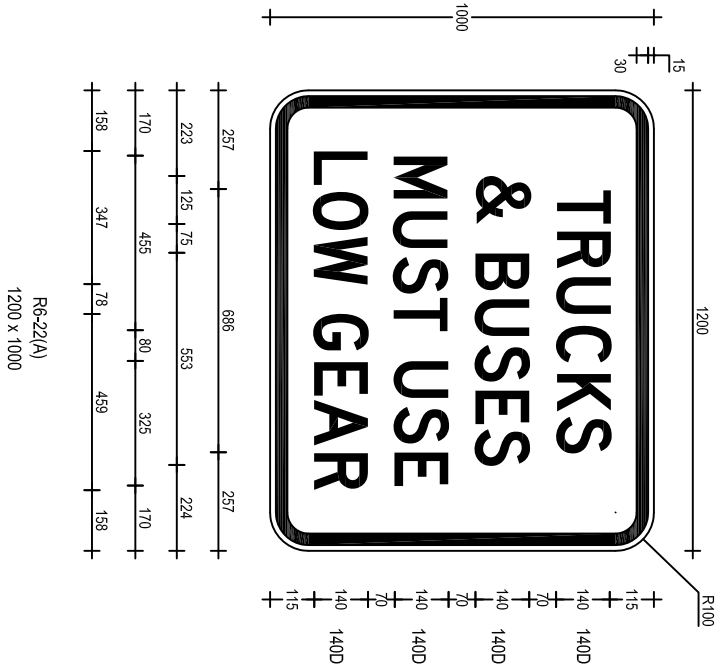

R6-22(A)
1200 x 1000

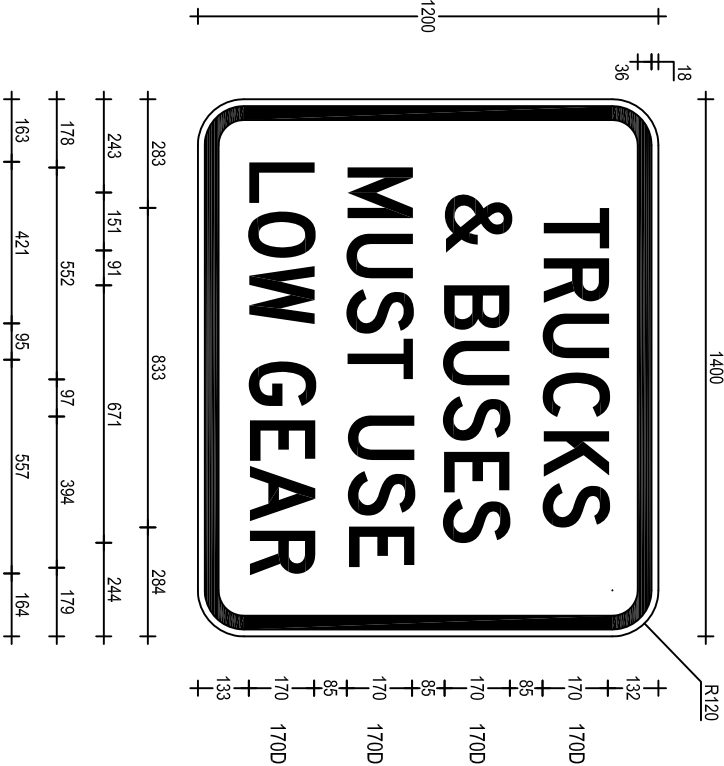

R6-22(B)
1400 x 1200

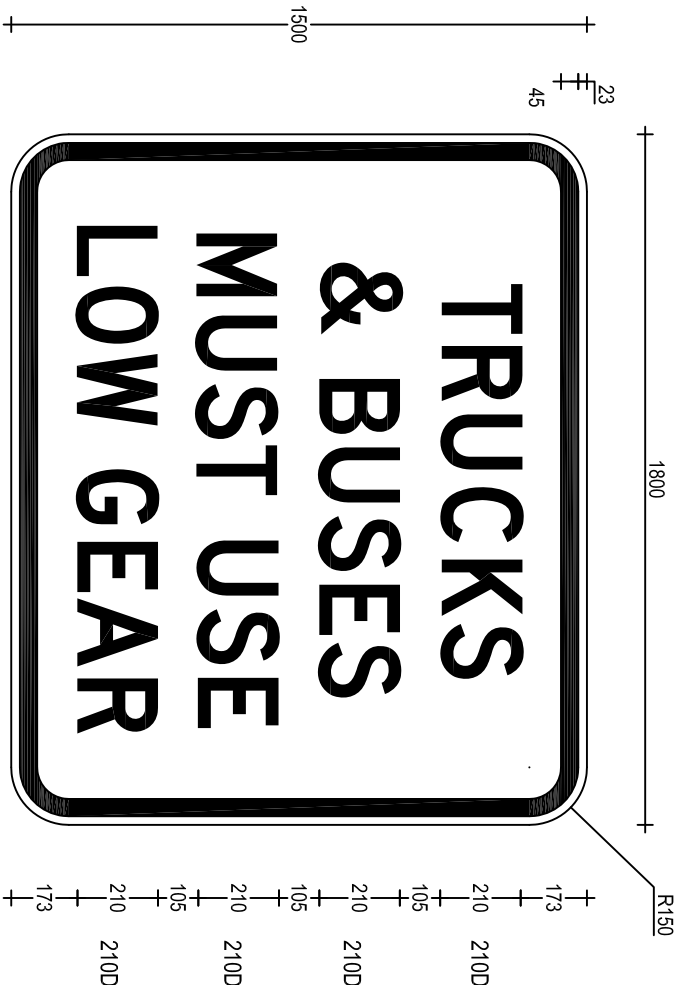

R6-22(C)
1800 x 1500