


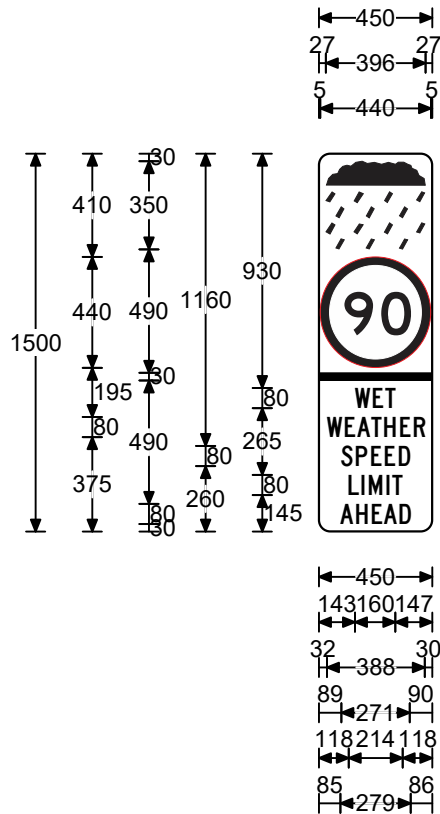

Legend

WET
WEATHER
SPEED
LIMIT
AHEAD

Font Type


FHWA Series C2000EX
FHWA Series C2000EX
FHWA Series C2000EX
FHWA Series C2000EX
FHWA Series C2000EX

Font Size

80
80
80
80
80

Specifications:
Aluminium Sign
Black lgd, symbol & Annulus
Cl.400 White refl grd(AS1906.1)


Size:	1500 x 450	Date:	23/1/23
Area:	0.68 sq.m	Scale:	1:30
Border:	0 x 0	Drawn:	daviesm
Cnr Rad:	45	Checked:	
Patch CR:	0	File:	r6-249n_a
Prepared using TraSiCAD Product of QMR		Path:	H:\Signs\TTT\DRAWINGS\REGULAT\TrasiCAD
		R6-249n(A)	

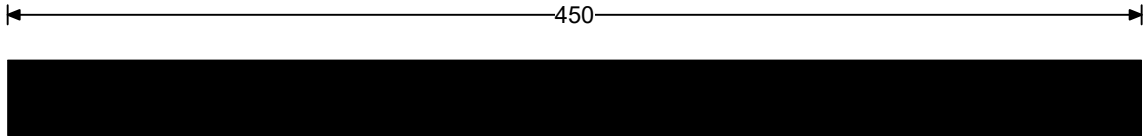

Legend Font Type Font Size

Patch Detail


Size:	30 x 450	Date:	23/1/23
Area:	0.01 sq.m	Scale:	1:3
Border:	0 x 0	Drawn:	daviesm
Cnr Rad:	0	Checked:	
Patch CR:	NA	File:	r6-249n_a
Prepared using TraSiCAD Product of QMR		Path:	H:\Signs\TTT\DRAWINGS\REGULAT\TrasiCAD
			R6-249n(A)

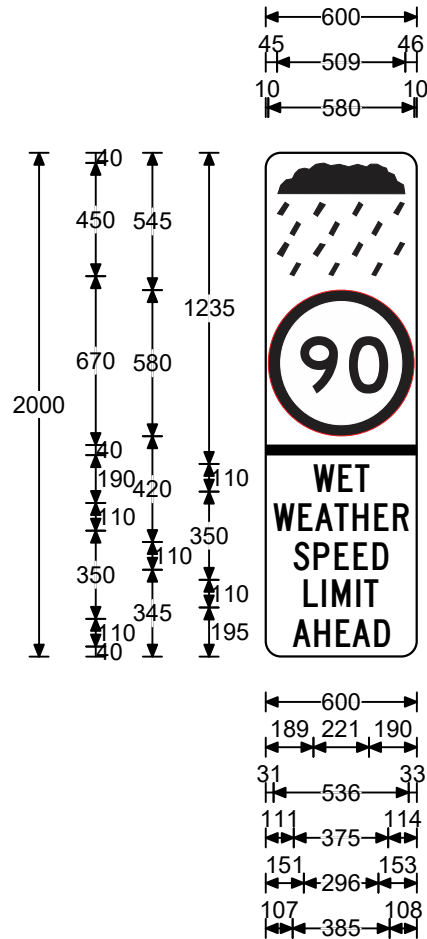

Legend	Font Type	Font Size
WET	FHWA Series C2000EX	110
WEATHER	FHWA Series C2000EX	110
SPEED	FHWA Series C2000EX	110
LIMIT	FHWA Series C2000EX	110
AHEAD	FHWA Series C2000EX	110

Specifications:
 Aluminium Sign
 Black lgd, symbol & Annulus
 Cl.400 White refl grd(AS1906.1)


Size:	2000 x 600	Date:	24/1/23
Area:	1.2 sq.m	Scale:	1:30
Border:	0 x 0	Drawn:	daviesm
Cnr Rad:	60	Checked:	
Patch CR:	0	File:	r6-249n_b
Prepared using TraSiCAD Product of QMR		Path:	H:\Signs\TTT\DRAWINGS\REGULAT\TrasiCAD
		R6-249n(B)	

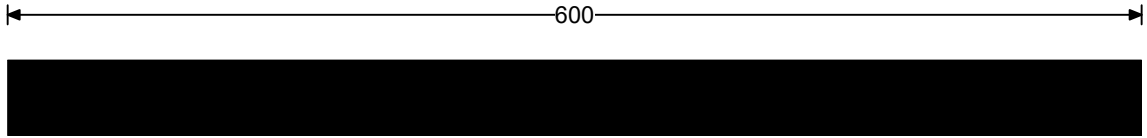

Legend Font Type Font Size

Patch Detail

Size:	40 x 600	Date:	24/1/23
Area:	0.02 sq.m	Scale:	1:4
Border:	0 x 0	Drawn:	daviesm
Cnr Rad:	0	Checked:	
Patch CR:	NA	File:	r6-249n_b
Prepared using TraSiCAD Product of QMR		Path:	H:\Signs\TTT\DRAWINGS\REGULAT\TrasiCAD
			R6-249n(B)

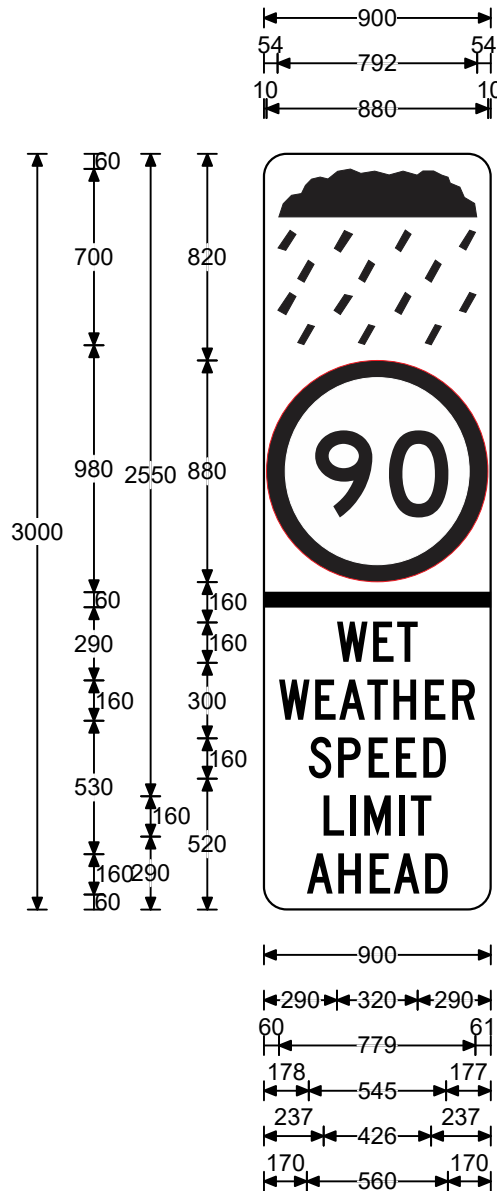

Legend

WET
WEATHER
SPEED
LIMIT
AHEAD

Font Type

FHWA Series C2000EX
FHWA Series C2000EX
FHWA Series C2000EX
FHWA Series C2000EX
FHWA Series C2000EX

Font Size

160
160
160
160
160

Specifications:
Aluminium Sign
Black lgd, symbol & Annulus
Cl.400 White refl grd(AS1906.1)

Size:	3000 x 900	Date:	23/1/23
Area:	2.7 sq.m	Scale:	1:30
Border:	0 x 0	Drawn:	daviesm
Cnr Rad:	90	Checked:	
Patch CR:	0	File:	r6-249n_c
Prepared using TraSiCAD Product of QMR		Path:	H:\Signs\TTT\DRAWINGS\REGULAT\TrasiCAD
		R6-249n(C)	


900

60

Legend Font Type Font Size

Patch Detail

Size:	60 x 900	Date:	23/1/23
Area:	0.05 sq.m	Scale:	1:10
Border:	0 x 0	Drawn:	daviesm
Cnr Rad:	0	Checked:	
Patch CR:	NA	File:	r6-249n_c
Prepared using TraSiCAD Product of QMR		Path:	H:\Signs\TTT\DRAWINGS\REGULAT\TrasiCAD
			R6-249n(C)

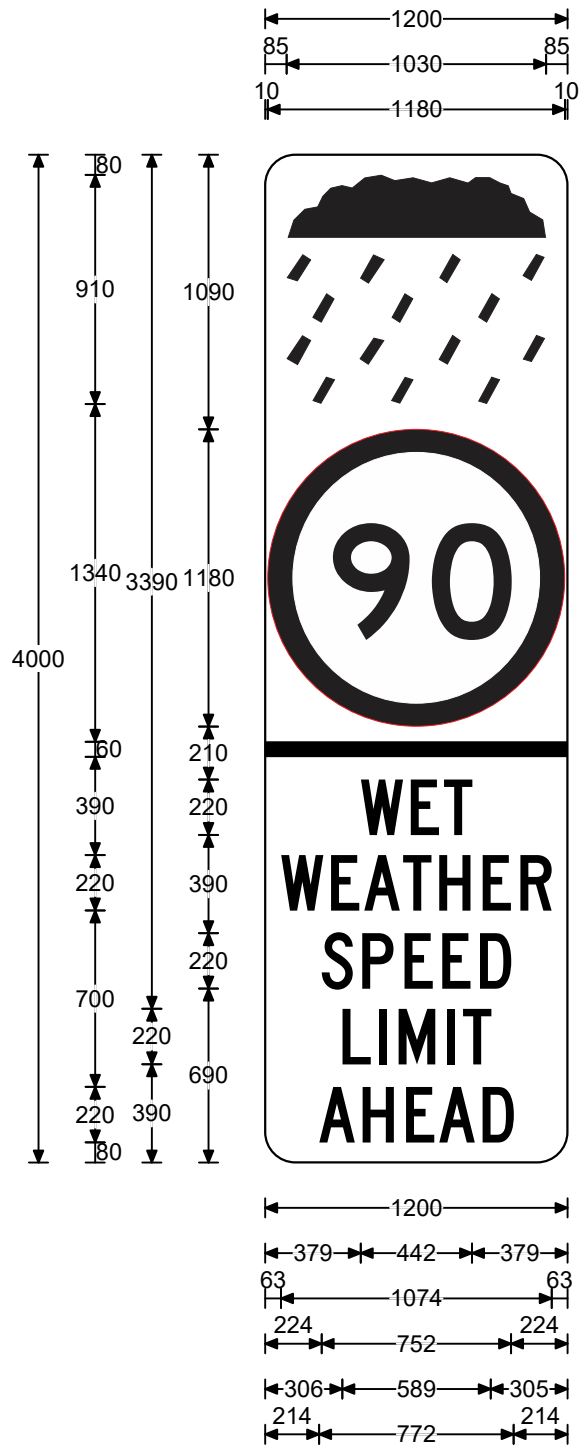

Legend

WET
WEATHER
SPEED
LIMIT
AHEAD

Font Type

FHWA Series C2000EX
FHWA Series C2000EX
FHWA Series C2000EX
FHWA Series C2000EX
FHWA Series C2000EX

Font Size

220
220
220
220
220

Specifications:
Aluminium Sign
Black lgd, symbol & Annulus
Cl.400 White refl grd(AS1906.1)

Size:	4000 x 1200	Date:	24/1/23
Area:	4.8 sq.m	Scale:	1:30
Border:	0 x 0	Drawn:	daviesm
Cnr Rad:	120	Checked:	
Patch CR:	0	File:	r6-249n_d
Prepared using TraSiCAD Product of QMR		Path:	H:\Signs\TTT\DRAWINGS\REGULAT\TrasiCAD
		R6-249n(D)	

1200

60

Legend Font Type Font Size

Patch Detail

Size:	60 x 1200	Date:	24/1/23
Area:	0.07 sq.m	Scale:	1:10
Border:	0 x 0	Drawn:	daviesm
Cnr Rad:	0	Checked:	
Patch CR:	NA	File:	r6-249n_d
Prepared using TraSiCAD Product of QMR		Path:	H:\Signs\TTT\DRAWINGS\REGULAT\TrasiCAD
			R6-249n(D)