


OR CODE	Scan to Check Document Version	REV	DATE	AMENDMENT / REVISION DESCRIPTION	APPROVAL	DRAWING FILE LOCATION / NAME: H:\SIGN\ITTDRAWINGS\PL\OTREG\RG&3.DWG
		01	23-03-18	AS Forms & material classification revised	P.Oliver	
ALL DIMENSIONS ARE IN MILLIMETRES UNLESS OTHERWISE SPECIFIED						
SIGN TO BE MANUFACTURED IN ACCORDANCE WITH RMS QA SPECIFICATION 3400						
DESIGNED						
SIGNATURE: M. Davies						
NAME: M. Davies						
DATE: 31-07-19						
REVIEWED						
SIGNATURE: J. Rozdos						
NAME: J. Rozdos						
DATE: 31-07-19						
VERIFIED						
SIGNATURE: P. Oliver						
NAME: P. Oliver						
TITLE: Manager, Guidance & Definition						
DATE: 31-07-19						
PREPARED BY						
GUIDANCE AND DELINEATION UNIT						
TRAFFIC ENGINEERING SERVICES						
TECHNICAL AND PROJECT SERVICES						
REGULATORY SIGN						
R6-3						
BRIDGE LOAD LIMIT X t GROSS						
SCALE: 1:15						
EDMS No. XXXXXXXXXX						
SHEET No. 1						
ISSUE 01						
SHEET 1 OF 1						
A3						

ACCEPTED FOR CONSTRUCTION

R6-3(A)
600 x 900

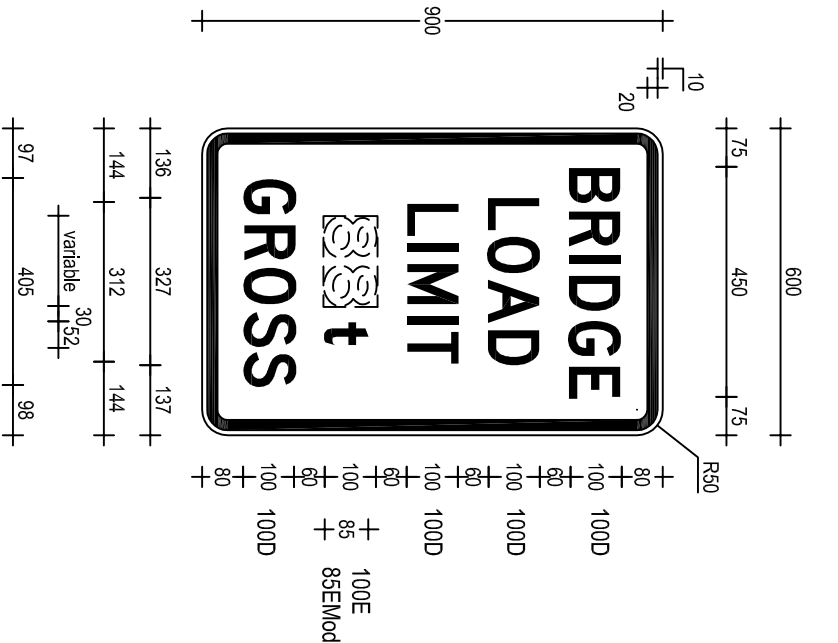

R6-3(B)
900 x 1350

