

510253035404550mm ON A3 SIZE ORIGINAL

| OR CODE                                                              | Scan to Check<br>Document Version | REV | DATE     | AMENDMENT / REVISION DESCRIPTION           | APPROVAL  | DRAWING FILE LOCATION / NAME: H:\SIGN\TTT\DRAWINGS\PLOT\REGULAT\TR6-30.DWG |
|----------------------------------------------------------------------|-----------------------------------|-----|----------|--------------------------------------------|-----------|----------------------------------------------------------------------------|
|                                                                      |                                   | 01  | 23-03-18 | AS Forms & material classification revised | P. Oliver |                                                                            |
| ALL DIMENSIONS ARE IN MILLIMETRES UNLESS OTHERWISE SPECIFIED         |                                   |     |          |                                            |           |                                                                            |
| SIGN TO BE MANUFACTURED IN ACCORDANCE WITH RMS QA SPECIFICATION 3400 |                                   |     |          |                                            |           |                                                                            |

| DESIGNED                                        | VERIFIED                                               |
|-------------------------------------------------|--------------------------------------------------------|
| SIGNED .....<br>NAME M. Davies<br>DATE 31-07-19 | SIGNED .....<br>NAME P. Oliver                         |
| REVIEWED .....<br>NAME J. Rozos                 | TITLE Manager, Guidance & Delineation<br>DATE 31-07-19 |



Transport  
Roads & Maritime  
Services

PREPARED BY  
GUIDANCE AND DELINEATION UNIT  
TRAFFIC ENGINEERING SERVICES  
TECHNICAL AND PROJECT SERVICES

REGULATORY SIGN

R6-30  
MEDIAN TURNING LANE (With Arrows)

SCALE: 1:15



EDMS No. XXXXXXXXXX

SHEET No. 1

ISSUE 01

SHEET 1 OF 1

A3

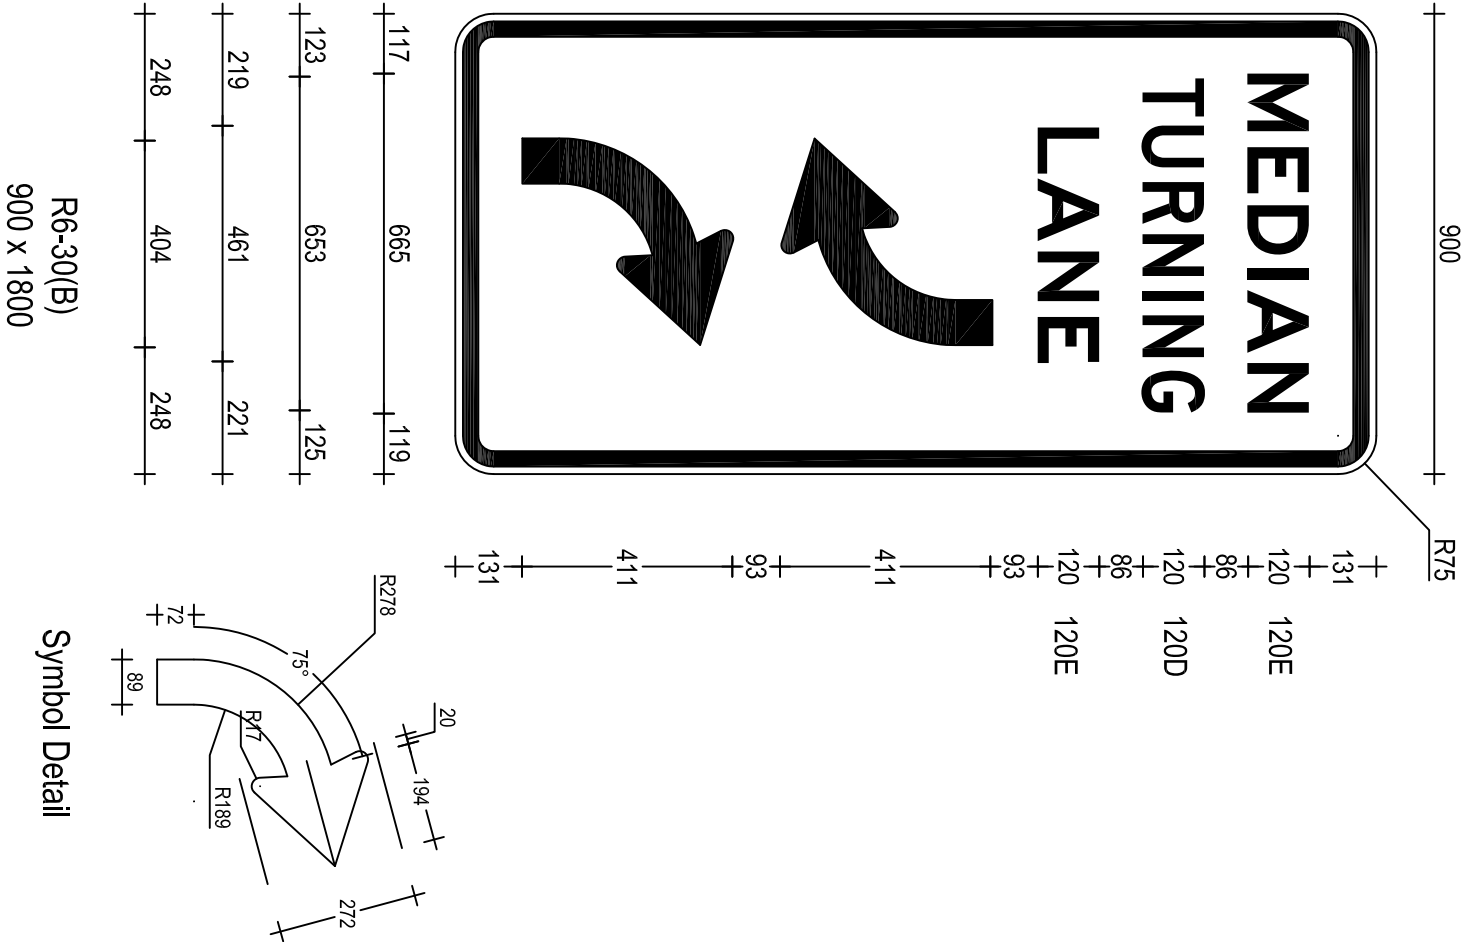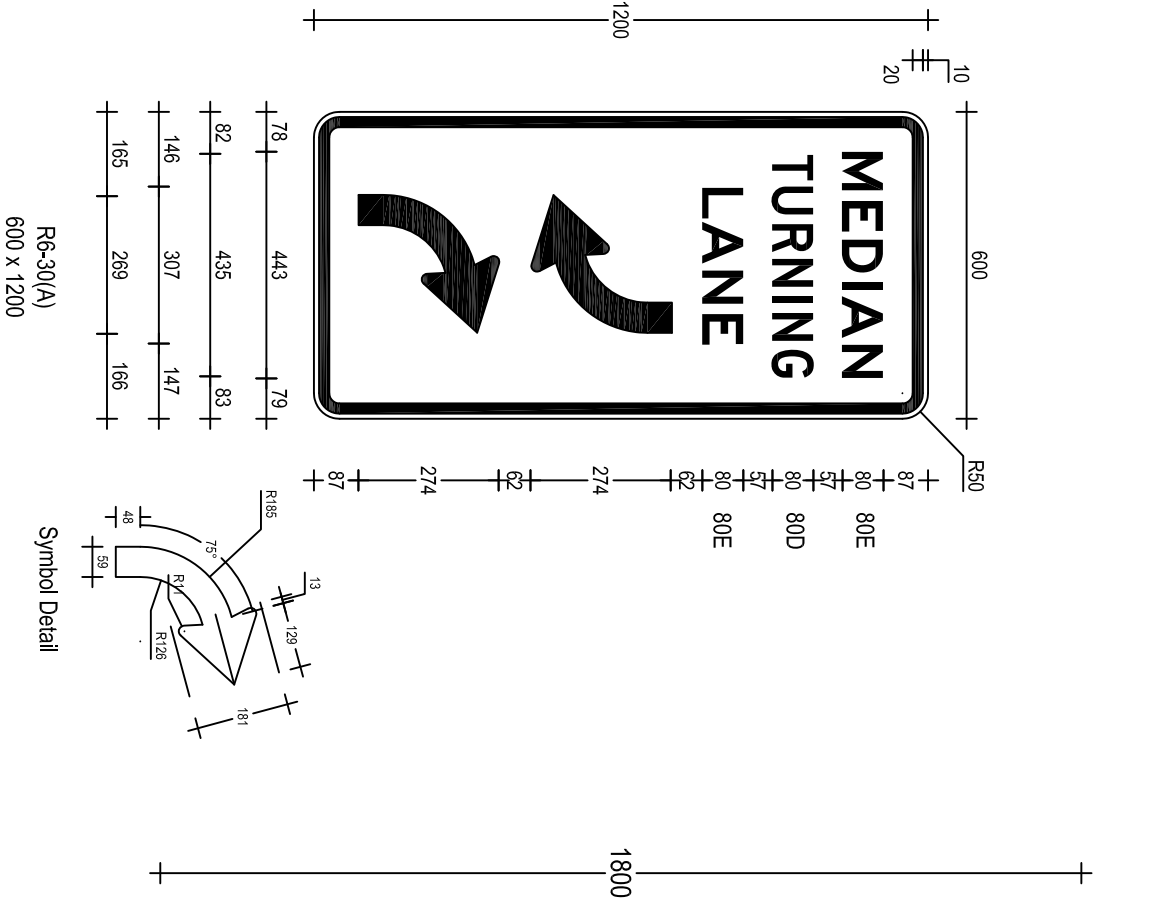

ACCEPTED FOR CONSTRUCTION