

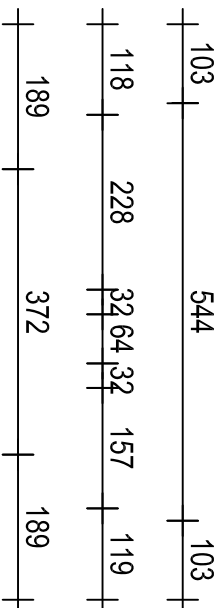


0 5 10 15 20 25 30 35 40 45 50mm ON A3 SIZE ORIGINAL

OR CODE			Scan to Check Document Version		REV	DATE	AMENDMENT / REVISION DESCRIPTION		APPROVAL	DRAWING FILE LOCATION / NAME: H:\SIGNS\TTRDRAWINGS\PLOT\REGULATORY-1-4.DWG	
					01	22-06-18	AS Form & material classification revised		P.Oliver		
MATERIALS: ALUMINIUM SIGN BLACK LEGEND AND BORDER ON AS1906.1 CL.400 WHITE REFLECTORISED GROUND WITH CL.400 WHITE REFL. "B" ON CL.400 RED REFL GRD											
SIGN TO BE MANUFACTURED IN ACCORDANCE WITH RMS QA SPECIFICATION 2400											
ALL DIMENSIONS ARE IN MILLIMETRES UNLESS OTHERWISE SPECIFIED											
DESIGNED					VERIFIED						
SIGNED 					SIGNED 						
NAME: M. Davies					NAME: P. Oliver						
DATE: 31-07-19					DATE: 31-07-19						
REVIEWED					TITLE: Manager Guidance & Delineation						
SIGNED 					DATE: 31-07-19						
NAME: J. Rozos											
DATE: 31-07-19											
 Transport Roads & Maritime Services											
GUIDANCE AND DELINEATION UNIT TRAFFIC ENGINEERING SERVICES TECHNICAL AND PROJECT SERVICES											
REGULATORY SIGN R7-1-1-4N BUS LANE (AM or PM) (OVERHEAD)											
SHEET 1 OF 1											
SCALE: 1:10					EDMS No. XXXXXXXXXX		SHEET No. 1		ISSUE 01		

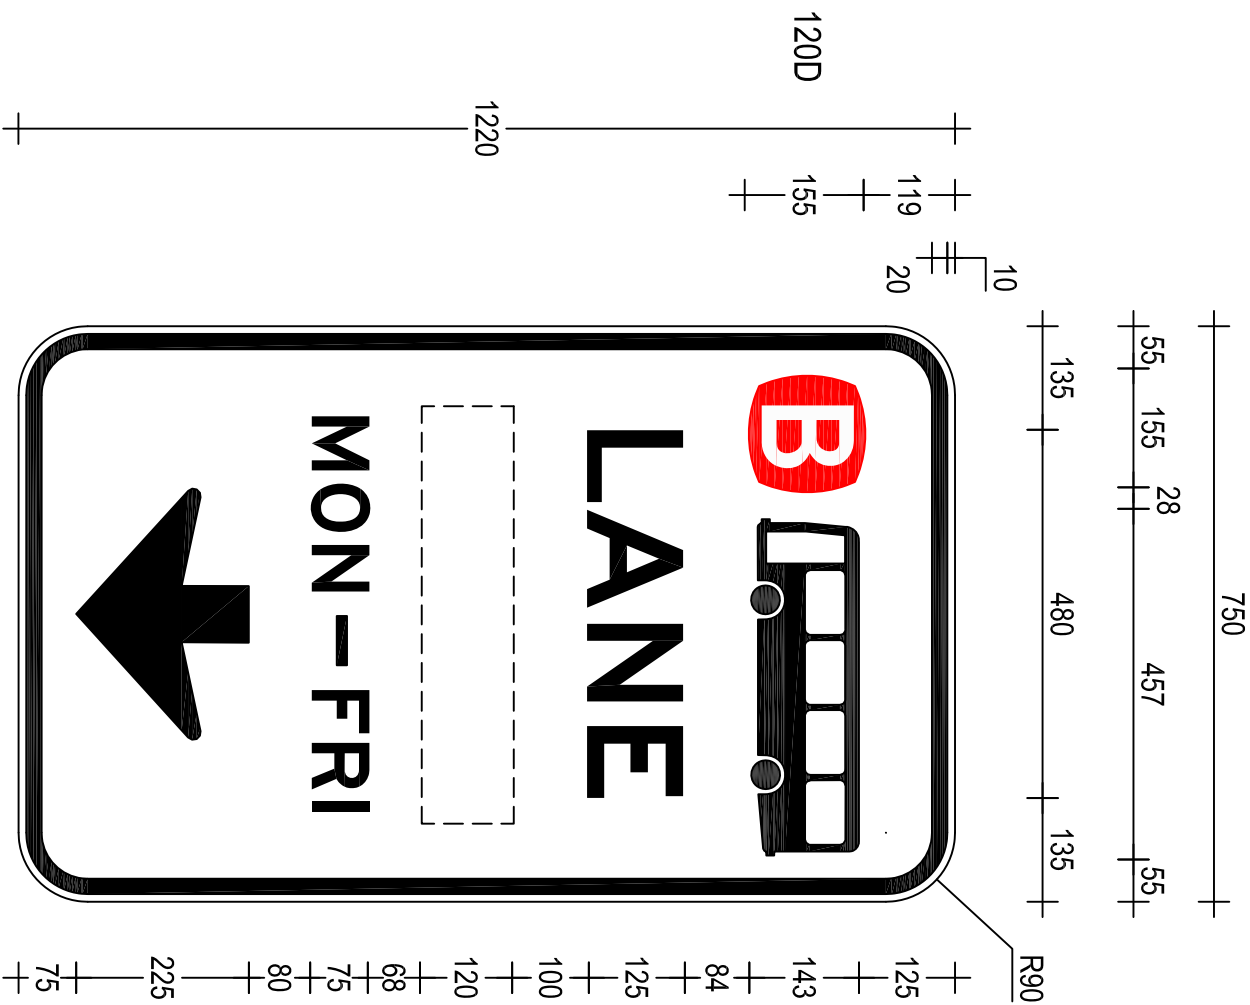

R7-1-1-4n
750 x 1220

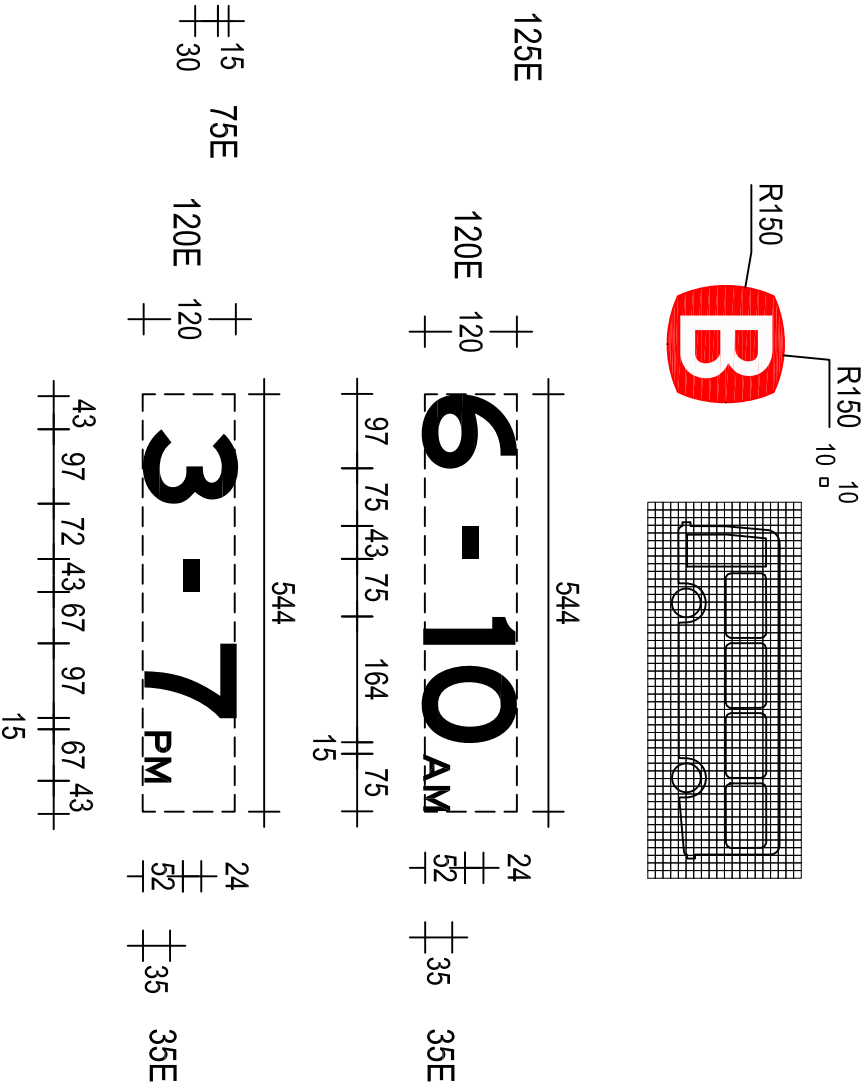

* Note: Times may vary. This is an example only.

ACCEPTED FOR CONSTRUCTION