
 


OR CODE			Scan to Check Document Version			REV	DATE	AMENDMENT / REVISION DESCRIPTION			APPROVAL	DRAWING FILE LOCATION / NAME: H:\SIGN\T\T\DRAWINGS\PLOT\REGULAT\R7-3.DWG		
						01	23-03-18	AS Forms & material classification revised			P. Oliver			
ALL DIMENSIONS ARE IN MILLIMETRES UNLESS OTHERWISE SPECIFIED														
SIGN TO BE MANUFACTURED IN ACCORDANCE WITH RMS QA SPECIFICATION 3400														
MATERIALS: ALUMINIUM SIGN BLACK LEGEND AND BORDER ON AS1906.1 CL.400 WHITE REFLECTORISED GROUND														
DESIGNED														
SIGNED														
NAME			M. Davies											
DATE			31-07-19											
REVIEWED														
SIGNED														
NAME			J. Rozdos											
DATE			31-07-19											
VERIFIED														
SIGNED														
NAME			P. Oliver											
TITLE			Manager, Guidance & Delineation											
DATE			31-07-19											
 Transport Roads & Maritime Services GOVERNMENT														
PREPARED BY GUIDANCE AND DELINEATION UNIT TRAFFIC ENGINEERING SERVICES TECHNICAL AND PROJECT SERVICES														
REGULATORY SIGN R7-3(R) RIGHT LANE														
SHEET 1 OF 1														
SCALE: 1:15			EDMS No. XXXXXXXXXX			SHEET No. 1			ISSUE 01			A3		

ACCEPTED FOR CONSTRUCTION

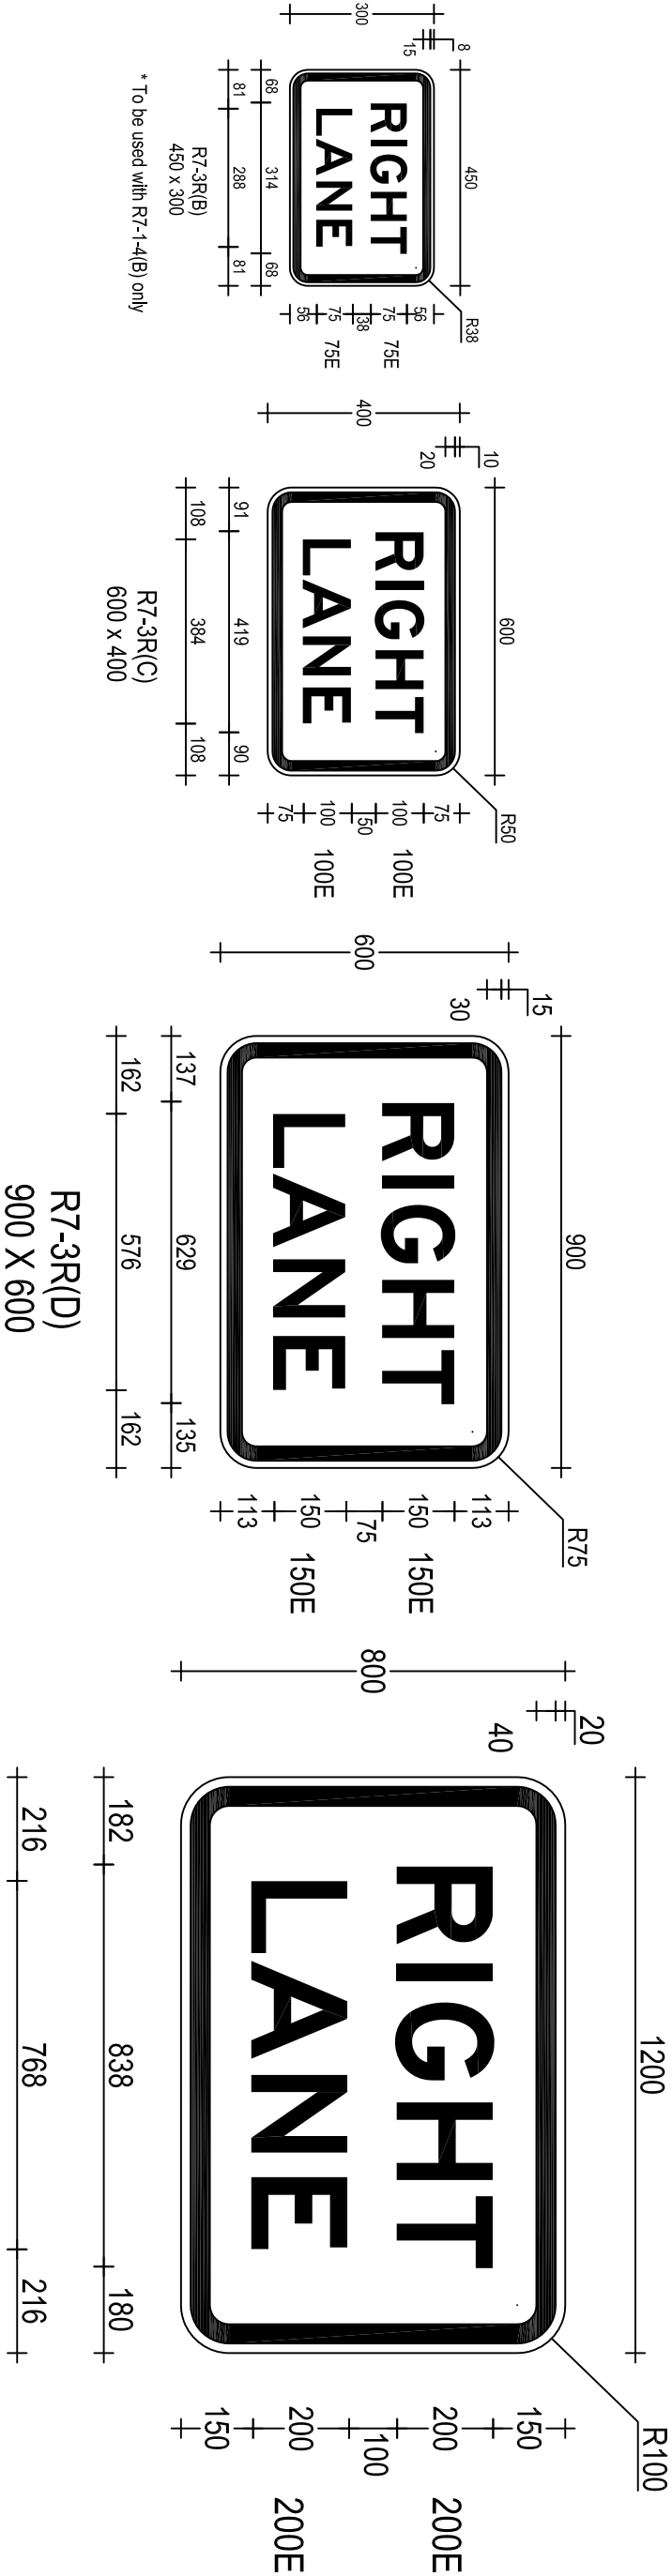

* To be used with R7-1-4(B) only

R7-3R(E)
1200 x 800