
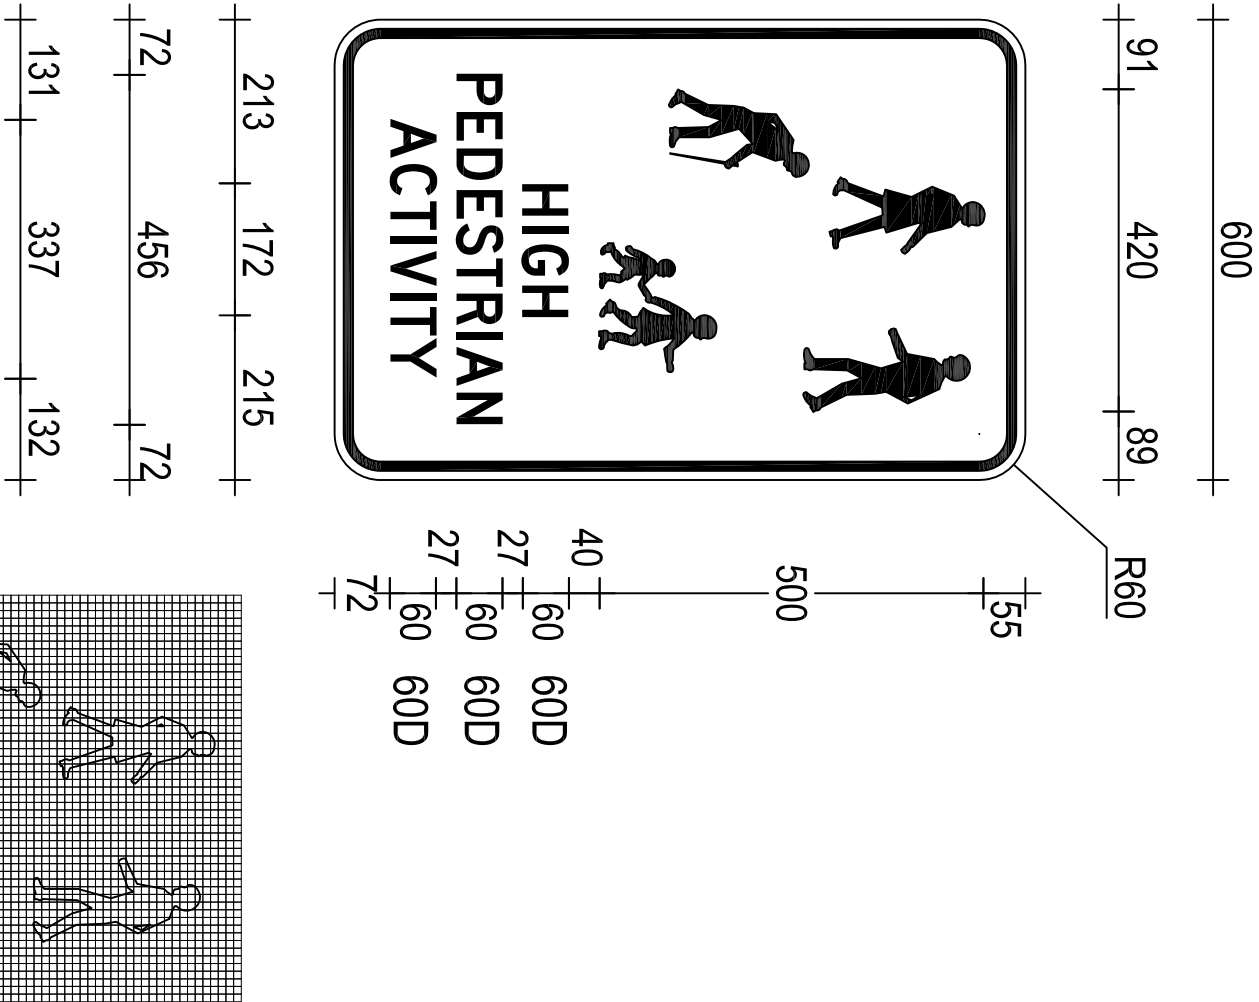


OR CODE		Scan to Check Document Version		REV	DATE	AMENDMENT / REVISION DESCRIPTION	APPROVAL	DRAWING FILE LOCATION / NAME: H:\SIGN\TTT\DRAWINGS\PICTO\REGULATR\R9-213n.DWG		DESIGNED	VERIFIED	PREPARED BY GUIDANCE AND DELINEATION UNIT ADVANCED TECHNICAL SERVICES INFRASTRUCTURE AND PLACE		REGULATORY SIGN R9-213n HIGH PEDESTRIAN ACTIVITY		SHEET 1 OF 1		A3			
				01	22-03-18	AS Forms & material classification revised	P. Oliver	MATERIALS: ALUMINIUM SIGN BLACK LEGEND, SYMBOL AND BORDER ON AS1906.1 CL.400 WHITE REFLECTORISED GROUND		NAME : M. Davies DATE : 24-03-21 REVIEWED NAME : J. Rozz05 DATE : 24-03-21	NAME : P. Oliver TITLE : Manager, Guidance & Delineation DATE : 24-03-21	 Transport Roads & Maritime Services		SCALE: 1:10		EDMS No. XXXXXXXXXX		SHEET No. 1		ISSUE 01	
ALL DIMENSIONS ARE IN MILLIMETRES UNLESS OTHERWISE SPECIFIED										SIGN TO BE MANUFACTURED IN ACCORDANCE WITH RMS QA SPECIFICATION 3400											

© Roads and Maritime Services

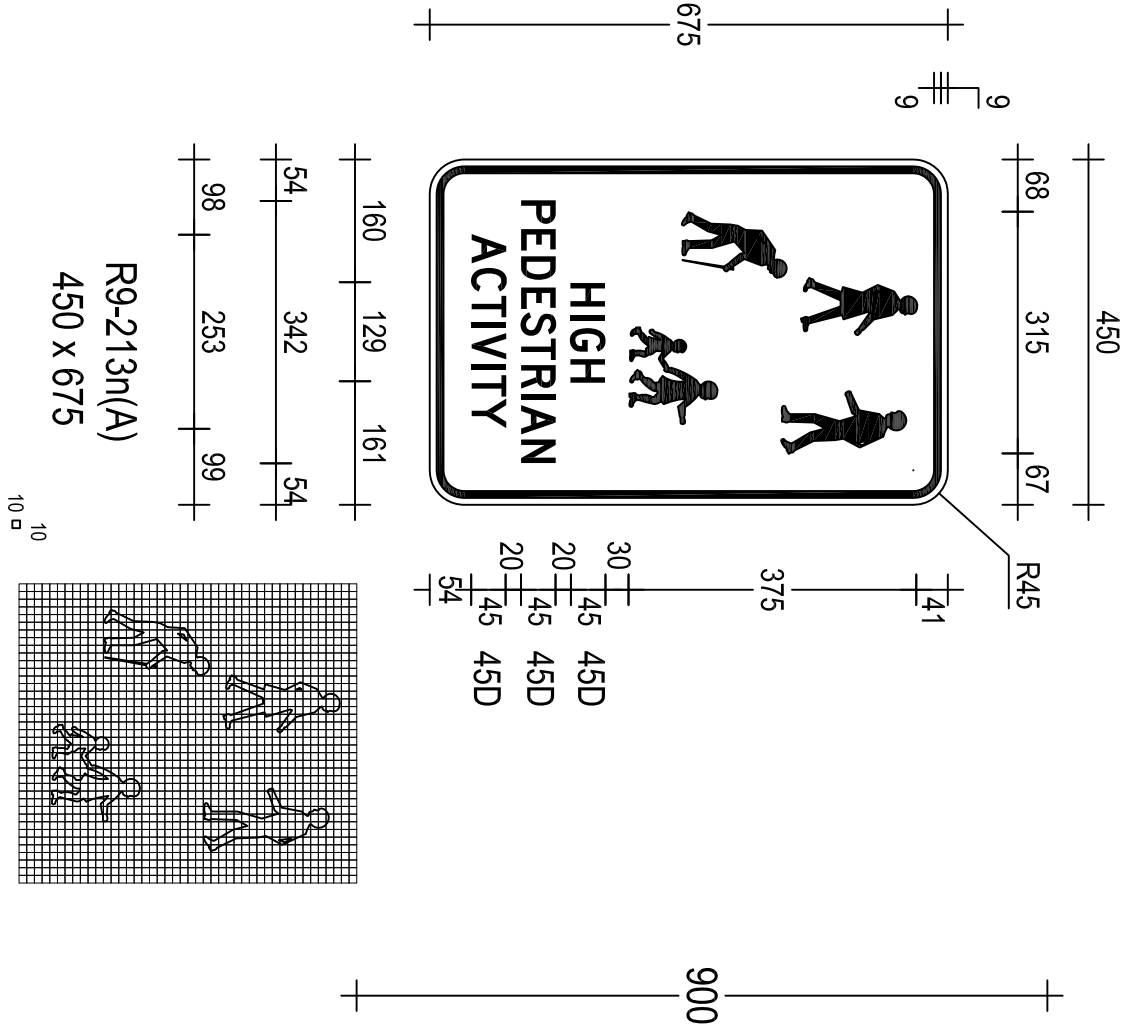

ACCEPTED FOR CONSTRUCTION