


OR CODE		Scan to Check Document Version		REV	DATE	AMENDMENT / REVISION DESCRIPTION	APPROVAL	DRAWING FILE LOCATION / NAME: H:\SIGN\TTT\DRAWINGS\PLOT\REGULATR9-215n.DWG		DESIGNED		VERIFIED		PREPARED BY		REGULATORY SIGN		A3					
				01	22-03-18	AS Forms & material classification revised	P. Oliver	MATERIALS: ALUMINIUM SIGN BLACK LEGEND AND BORDER ON AS1906.1 CL 400 WHITE REFLECTORISED GROUND		NAME M. Davies DATE 24-03-21		NAME P. Oliver TITLE Manager, Guidance & Delineation DATE 24-03-21		NSW Transport Roads & Maritime Services		R9-215n BUSES AND AUTHORISED VEHICLES EXCEPTED							
								SIGN TO BE MANUFACTURED IN ACCORDANCE WITH RMS QA SPECIFICATION 3400		REVIEWED NAME J. Roz205 DATE 24-03-21				GUIDANCE AND DELINEATION UNIT ADVANCED TECHNICAL SERVICES INFRASTRUCTURE AND PLACE		SHEET 1 OF 1							
ALL DIMENSIONS ARE IN MILLIMETRES UNLESS OTHERWISE SPECIFIED																							
SCALE: 1:5																							
© Roads and Maritime Services																EDMS No. XXXXXXXXXX				SHEET No. 1		ISSUE 01	

ACCEPTED FOR CONSTRUCTION

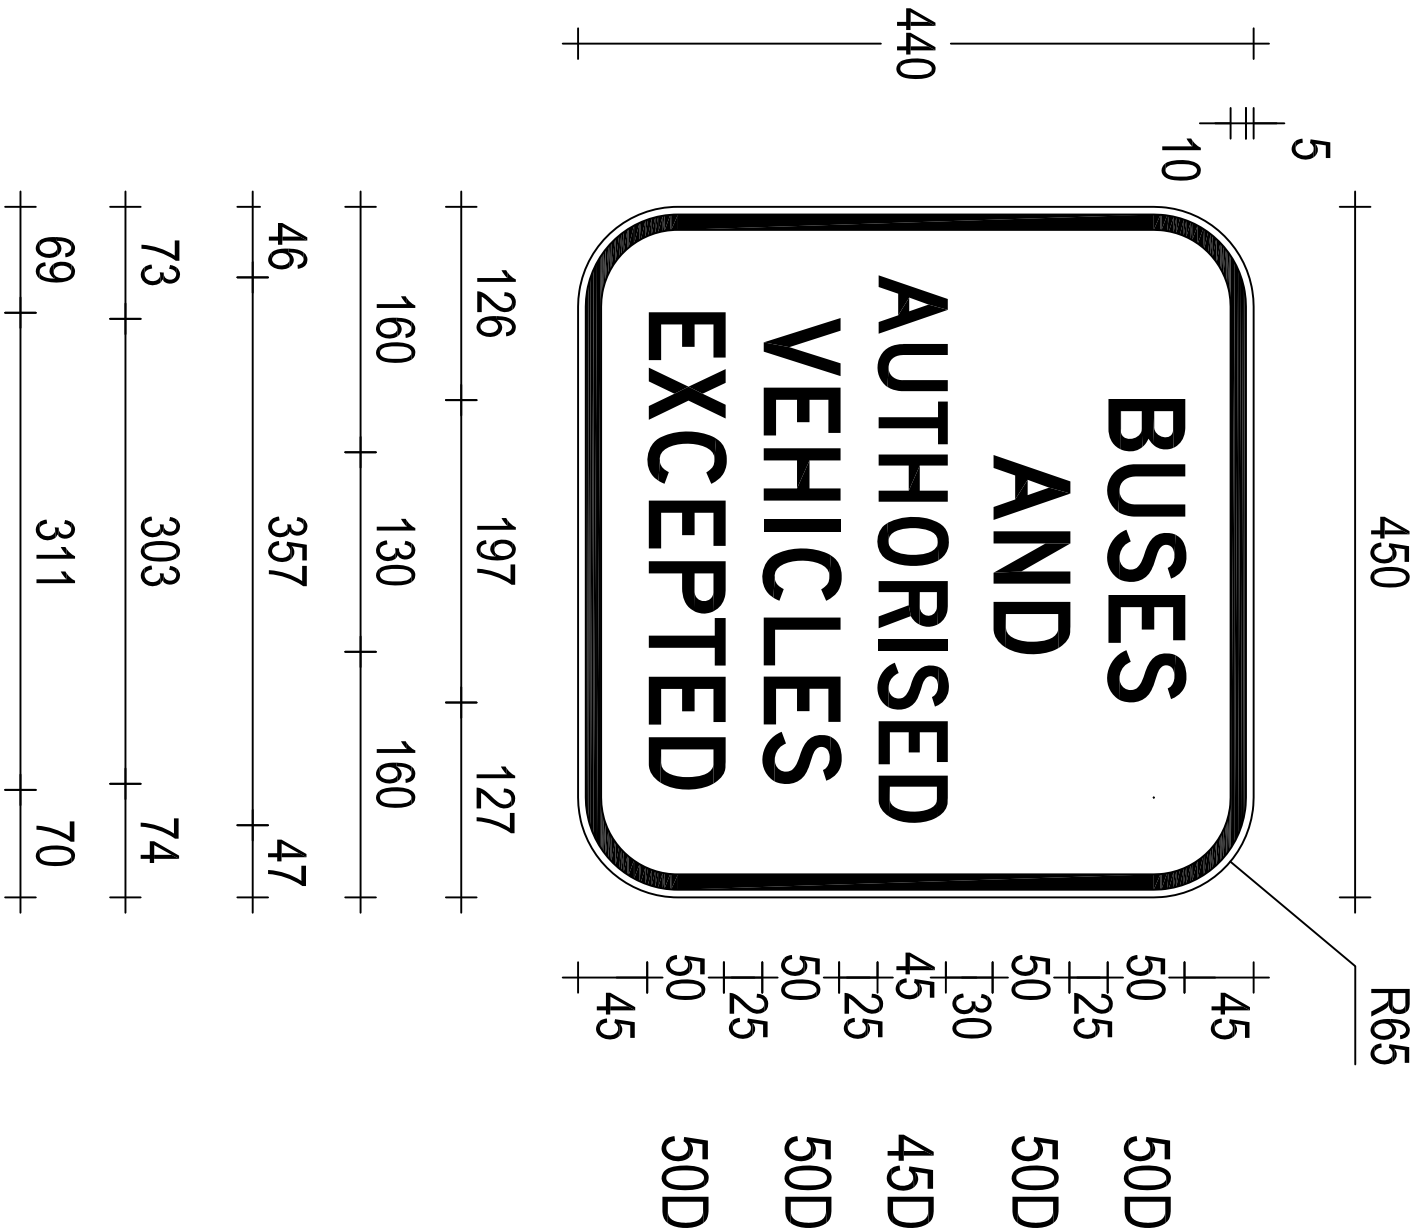

R9-215n
450 x 440