


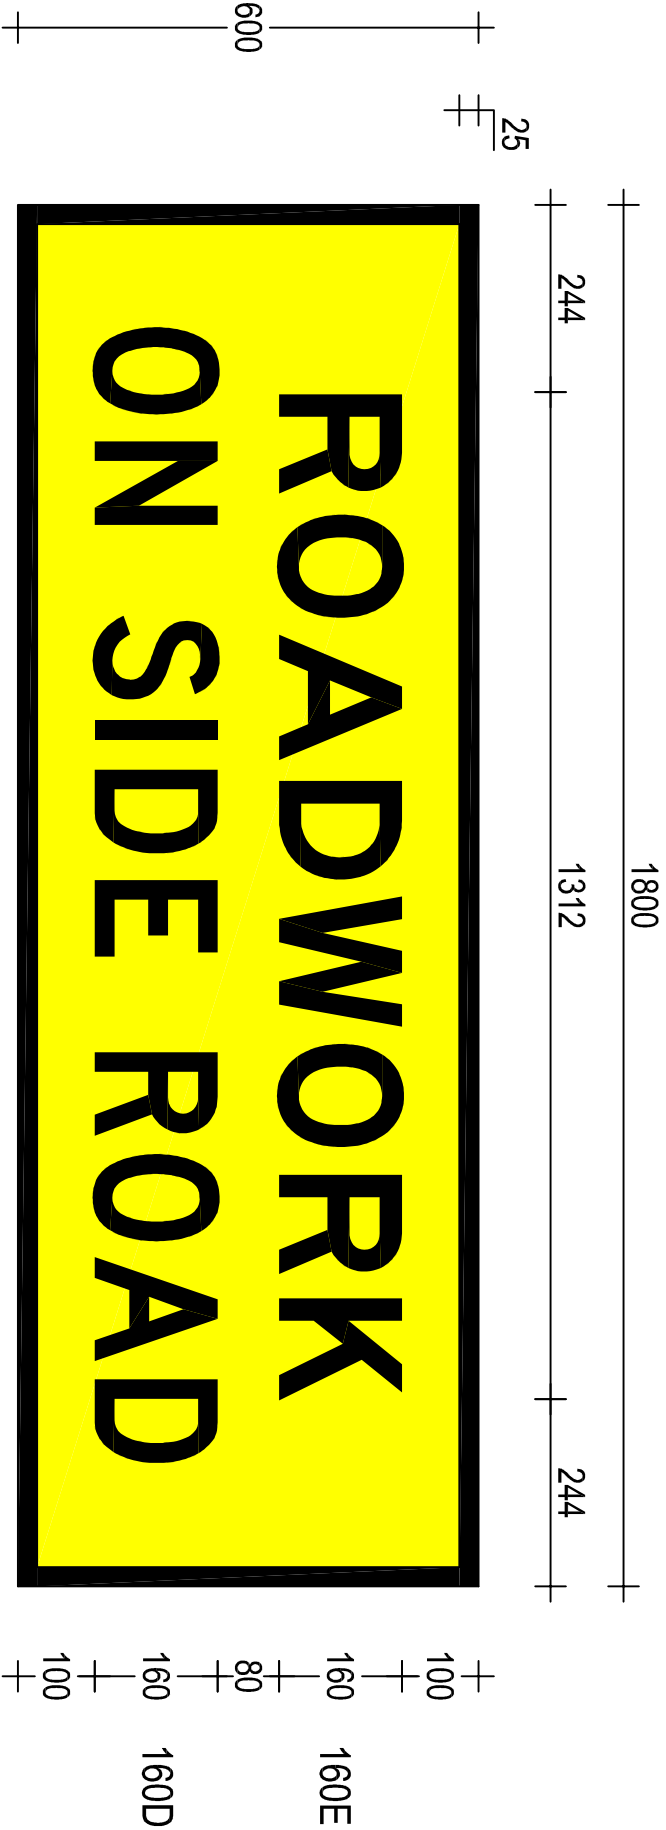

T1-25
1800 x 600

ACCEPTED FOR CONSTRUCTION

THIS DRAWING MAY BE PREPARED IN COLOUR AND MAY BE INCOMPLETE IF COPIED

0 5 10 15 20 25 30 35 40 45 50mm ON A3 SIZE ORIGINAL

OR CODE	Scan to Check Document Version	REV	DATE	AMENDMENT / REVISION DESCRIPTION	APPROVAL	DRAWING FILE LOCATION / NAME: H:\SIGN\T1\DRAWINGS\T1\OTTEMP\T1-25.DWG
		01	22-03-18	AS Forms & material classification revised	P.Oliver	
ALL DIMENSIONS ARE IN MILLIMETRES UNLESS OTHERWISE SPECIFIED						
SIGN TO BE MANUFACTURED IN ACCORDANCE WITH RMS QA SPECIFICATION 3400						
MATERIALS: ALUMINIUM SIGN BLACK LEGEND AND BORDER ON AS1906.1 CL.400 YELLOW REFLECTORISED GROUND						
DESIGNED						
SIGNED 						
NAME M. Davies						
DATE 12-07-19						
REVIEWED						
SIGNED 						
NAME J. Rozos						
DATE 12-07-19						
VERIFIED						
SIGNED 						
NAME P. Oliver						
TITLE Manager, Guidance & Delineation						
DATE 12-07-19						
 Transport Roads & Maritime Services						
GUIDANCE AND DELINEATION TRAFFIC ENGINEERING SERVICES TECHNICAL AND PROJECT SERVICES						
TEMPORARY SIGN						
T1-25						
ROADWORK ON SIDE ROAD						
SHEET 1 OF 1						
SCALE: 1:10						
EDMS No. XXXXXXXXXX						
SHEET No. 1						
ISSUE 01						
A3						