


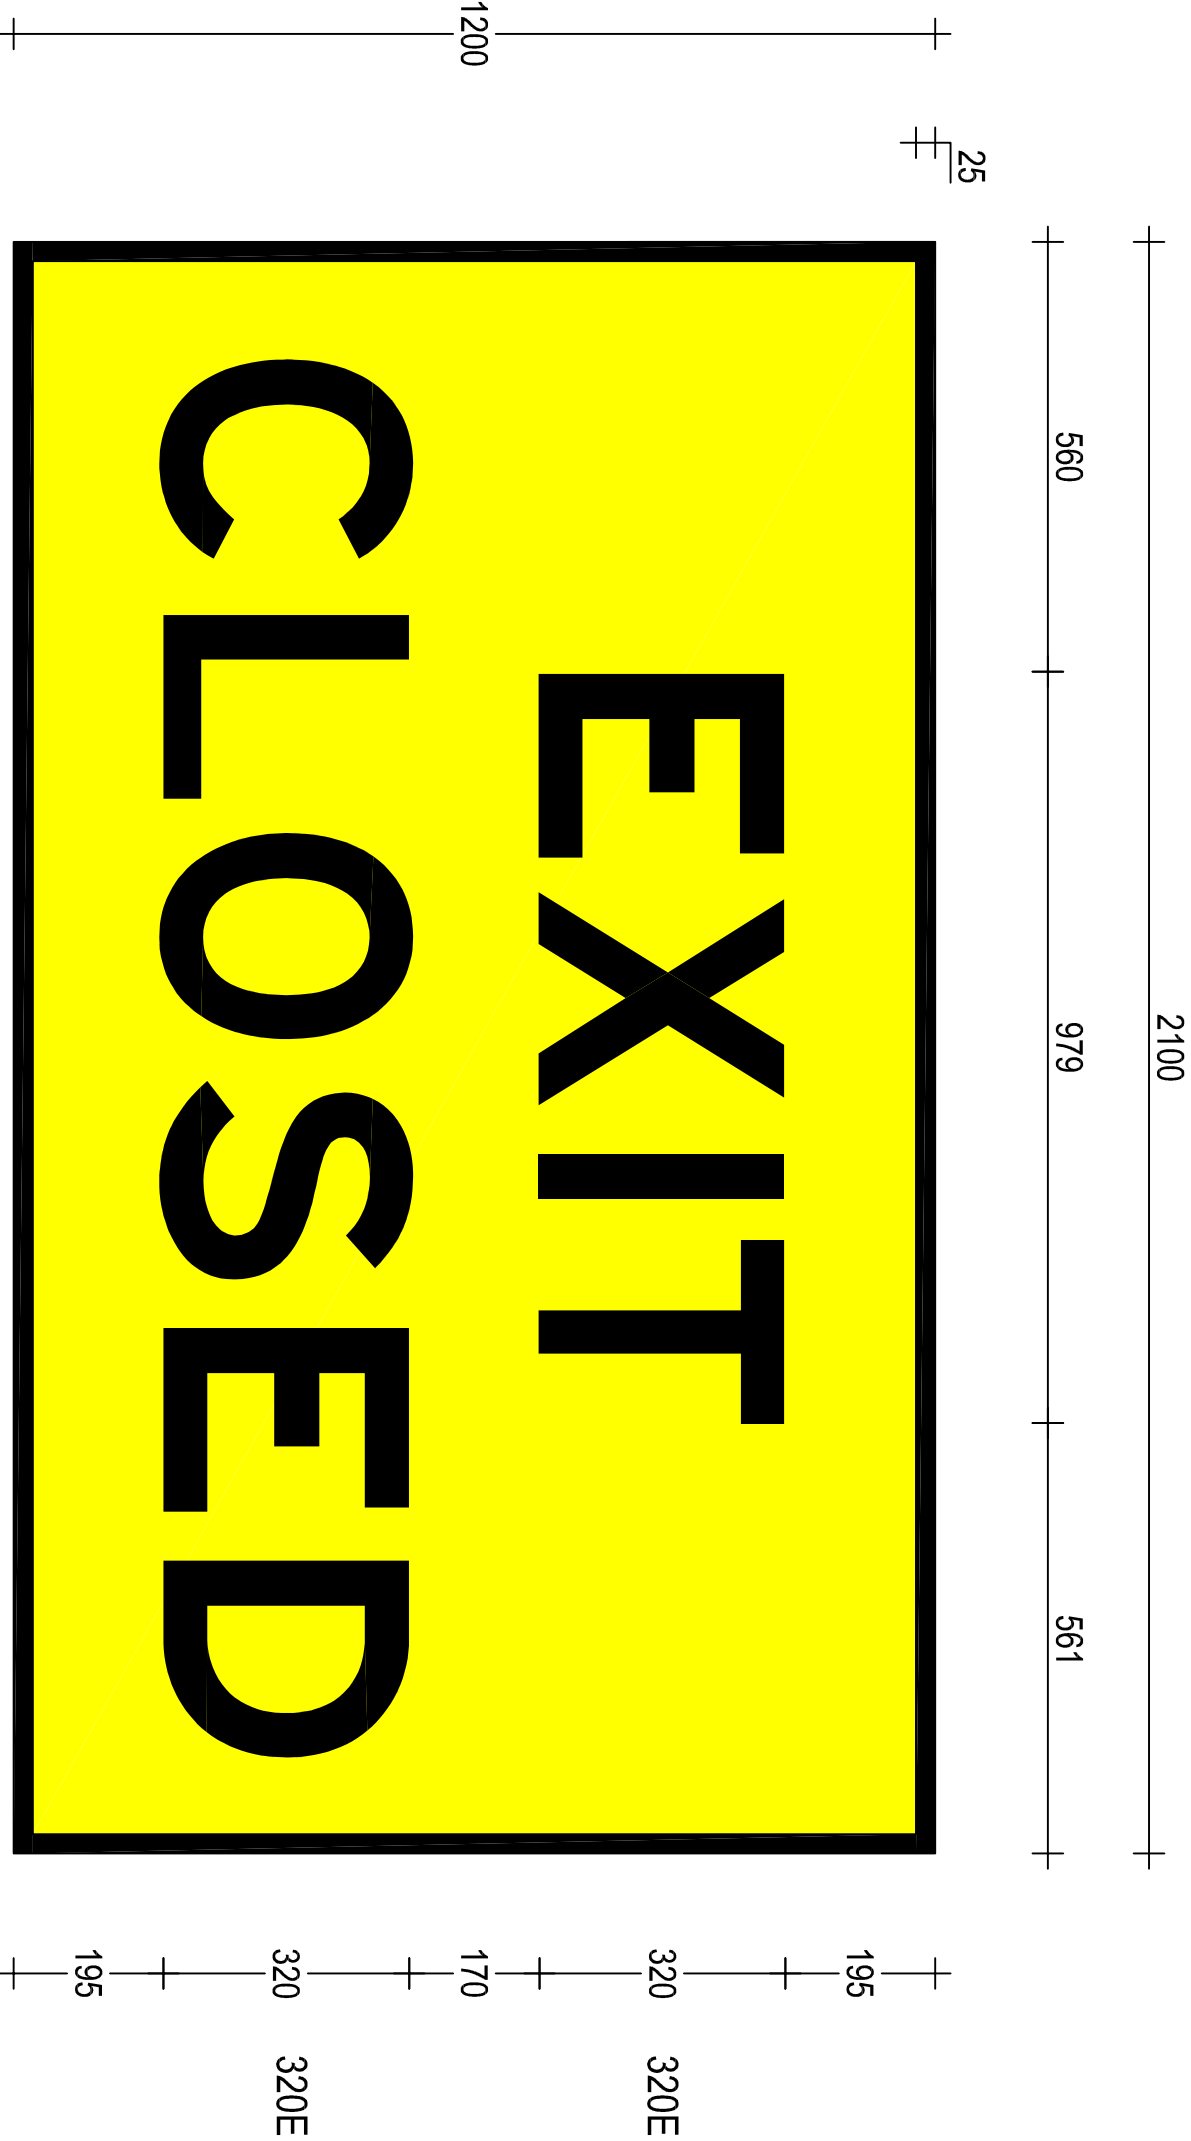


T2-20n
2100 x 1200

ACCEPTED FOR CONSTRUCTION

THIS DRAWING MAY BE PREPARED IN COLOUR AND MAY BE INCOMPLETE IF COPIED

0 5 10 15 20 25 30 35 40 45 50mm ON A3 SIZE ORIGINAL

 OR CODE	Scan to Check Document Version	REV	DATE	AMENDMENT / REVISION DESCRIPTION	APPROVAL	DRAWING FILE LOCATION / NAME: H:\SIGN\TTP\DRAWINGS\PL\OTTEMP\T220n.DWG
		01	23-03-18	AS Forms & material classification revised	P.Oliver	
ALL DIMENSIONS ARE IN MILLIMETRES UNLESS OTHERWISE SPECIFIED						
SIGN TO BE MANUFACTURED IN ACCORDANCE WITH RMS QA SPECIFICATION 3400						
MATERIALS: ALUMINIUM SIGN BLACK LEGEND AND BORDER ON AS1906.1 CL.400 YELLOW REFLECTORISED GROUND						
DESIGNED		VERIFIED				
SIGNED		SIGNED				
NAME M.Davies		NAME P.Oliver				
DATE 12-07-19		DATE 12-07-19				
REVIEWED		TITLE Manager, Guidance & Delineation				
SIGNED		SIGNED				
NAME J. Rozos		NAME				
DATE 12-07-19		DATE 12-07-19				
 NSW GOVERNMENT Transport Roads & Maritime Services PREPARED BY GUIDANCE AND DELINEATION TRAFFIC ENGINEERING SERVICES TECHNICAL AND PROJECT SERVICES						
TEMPORARY SIGN						
T2-20n						
EXIT CLOSED						
SCALE: 1:10		EDMS N. XXXXXXXXXX	SHEET N. 1	ISSUE 01	A3	
SHEET 1 OF 1						