



1200

25

600

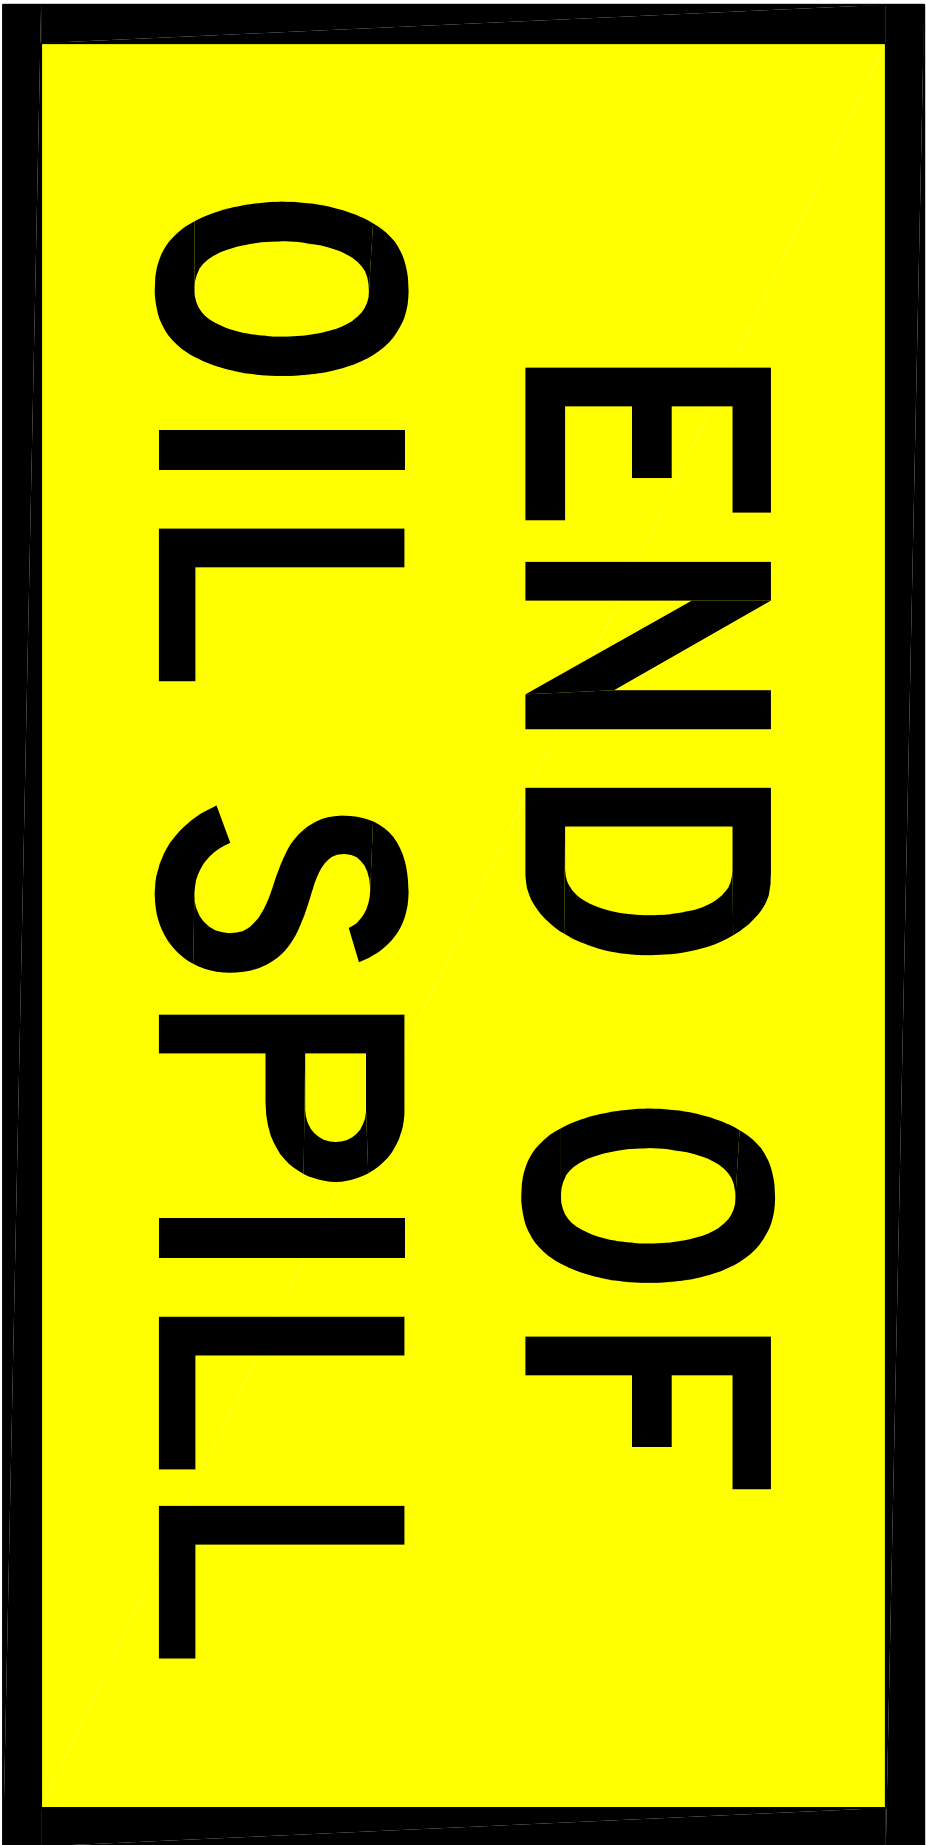

100 160D
160 160D
80
160 160D
100

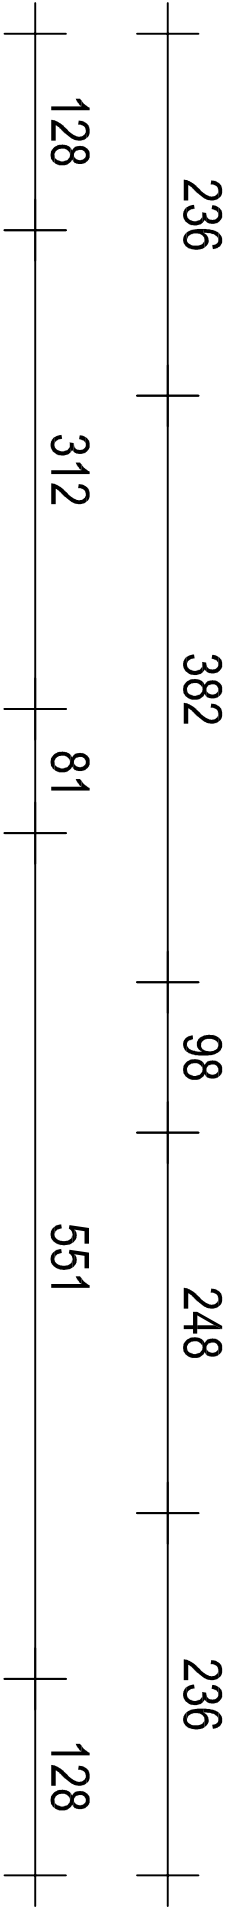

T4-215n

1200 x 600

ACCEPTED FOR CONSTRUCTION

OR CODE		Scan to Check Document Version		REV	DATE	AMENDMENT / REVISION DESCRIPTION	APPROVAL	DRAWING FILE LOCATION / NAME: H:\SIGN\TTP\DRAWINGS\PL\OTTEMP\T4215.DWG	DESIGNED	VERIFIED	TEMPORARY SIGN		T4-215n		END OF OIL SPILL		SHEET 1 OF 1		A3				
				01	23-03-18	AS Forms & material classification revised	P.Oliver		MATERIALS: ALUMINIUM SIGN BLACK LEGEND AND BORDER ON AS1906.1 CL.400 YELLOW REFLECTORISED GROUND	SIGNED  NAME M. Davies DATE 31-07-19 REVIEWED  SIGNED  NAME J. Rozos DATE 31-07-19	 SIGNED NAME P. Oliver DATE 31-07-19 TITLE Manager, Guidance & Delineation SIGNED DATE 31-07-19	 Transport Roads & Maritime Services GOVERNMENT		PREPARED BY GUIDANCE AND DELINEATION UNIT TRAFFIC ENGINEERING SERVICES TECHNICAL AND PROJECT SERVICES		SCALE: 1:5		EDMS N.:		SHEET N.:		ISSUE	
													XXXXXXXXXX		1		01						