

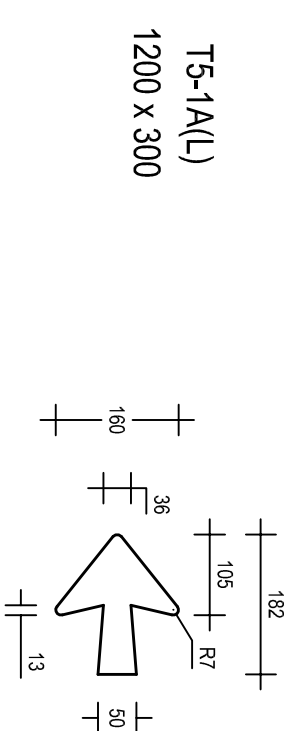


OR CODE	Scan to Check Document Version	REV	DATE	AMENDMENT / REVISION DESCRIPTION	APPROVAL	DRAWING FILE LOCATION / NAME: H:\SIGN\TTT\DRAWINGS\PL\OTTEMP\T5-1.LDWG
		01	23-03-18	AS Forms & material classification revised	P.Oliver	
ALL DIMENSIONS ARE IN MILLIMETRES UNLESS OTHERWISE SPECIFIED						SIGN TO BE MANUFACTURED IN ACCORDANCE WITH RMS QA SPECIFICATION 3400
DESIGNED						SIGNED NAME M. Davies DATE 12-07-19 REVIEWED SIGNED NAME J. Rozos DATE 12-07-19
VERIFIED						SIGNED NAME P. Oliver DATE 12-07-19 TITLE Manager, Guidance & Delineation
PREPARED BY NSW GOVERNMENT Transport Roads & Maritime Services						GUIDANCE AND DELINEATION TRAFFIC ENGINEERING SERVICES TECHNICAL AND PROJECT SERVICES
TEMPORARY SIGN T5-1(L) DETOUR LEFT ARROW						SCALE: 1:10
SHEET 1 OF 1						EDMS N _o . XXXXXXXXXX
A3						SHEET N _o . 1
						ISSUE 01

ACCEPTED FOR CONSTRUCTION

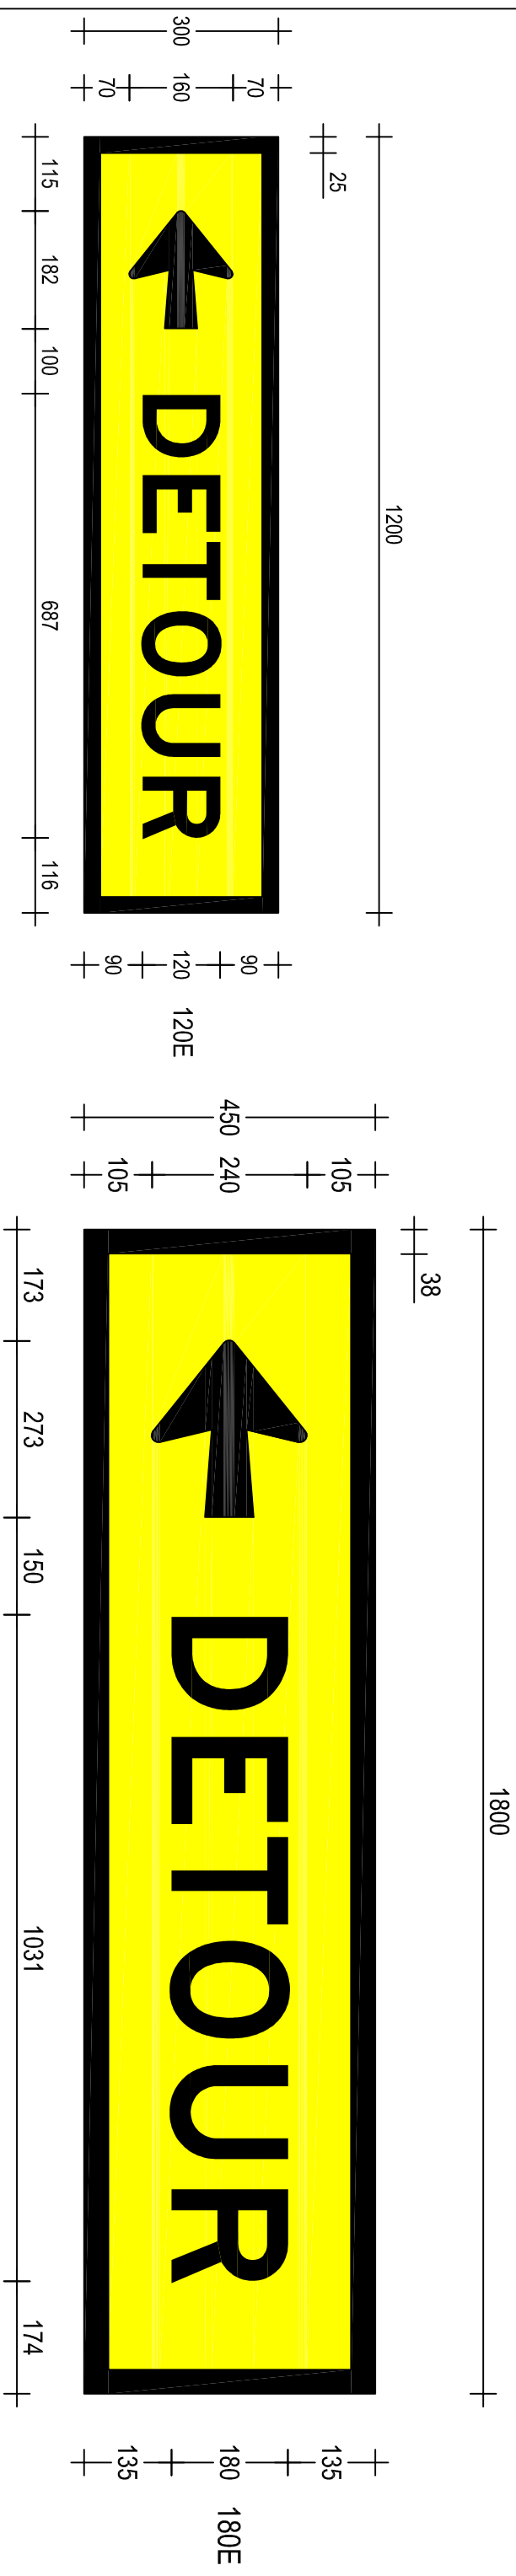

ARROW DETAIL

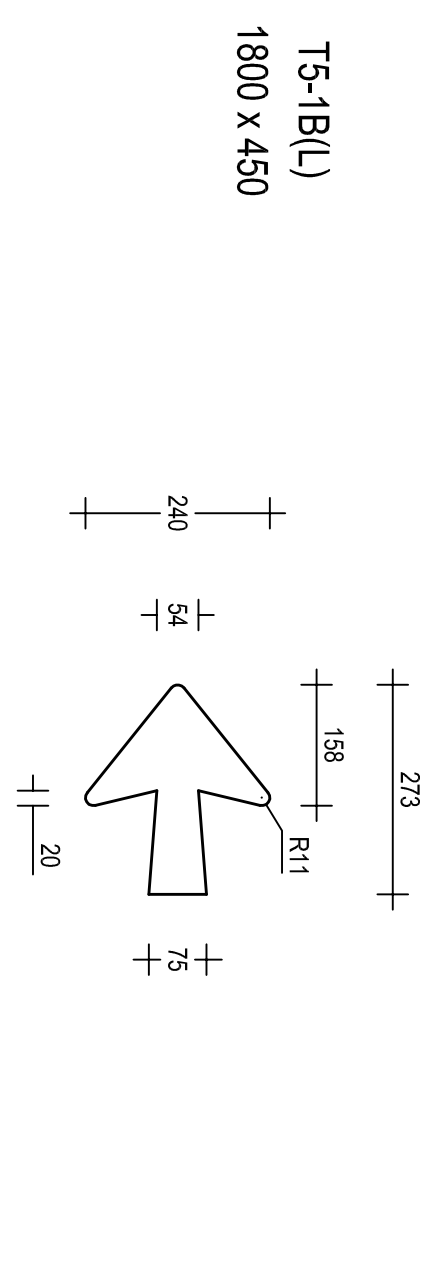

ARROW DETAIL