


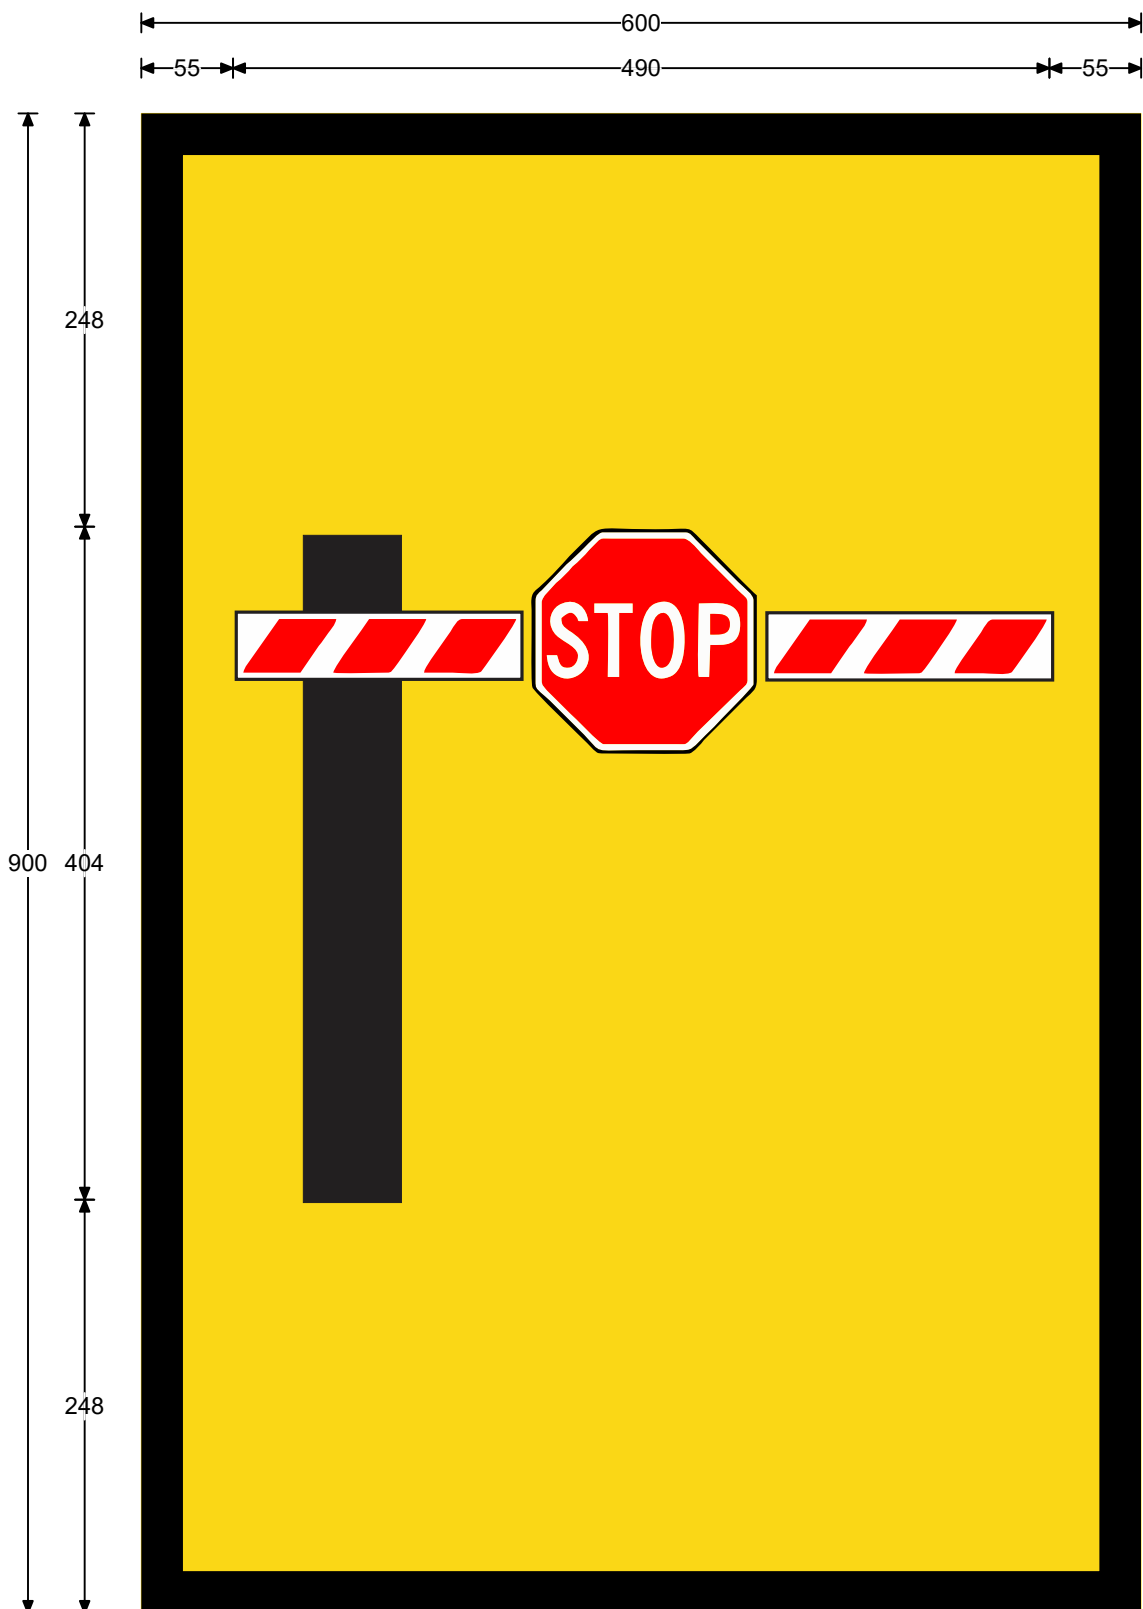

Legend

Font Type

Font Size

Specifications:

Aluminium Sign

Black Post & Border

Cl.400 Yellow refl grd(AS1906.1)

Boom Barrier:-Cl.400 Red refl Slash/ Cl.400 White refl
grd(AS1906.1)

Stop Sign:-Cl.400 White refl lgd & Bdr/ Cl.400 Red Refl Grd

Size:	900 x 600	Date:	28/4/20
Area:	0.54 sq.m	Scale:	1:4.5
Border:	0 x 25	Drawn:	DaviesM
Cnr Rad:	0	Checked:	
Patch CR:	NA	File:	tm2-52_d
 Prepared using TraSiCAD Product of QMR	Path: H:\Signs\TTT\DRAWINGS\IMMS Signs		
			tm2-52_d