
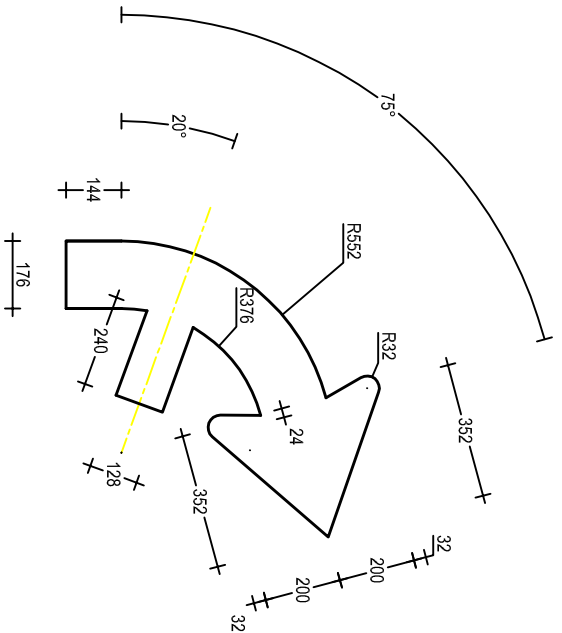
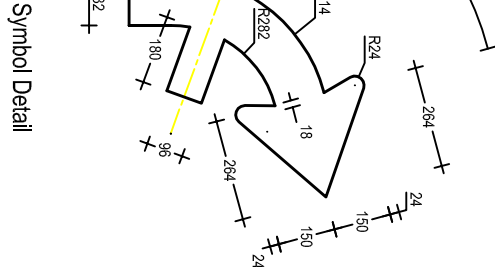
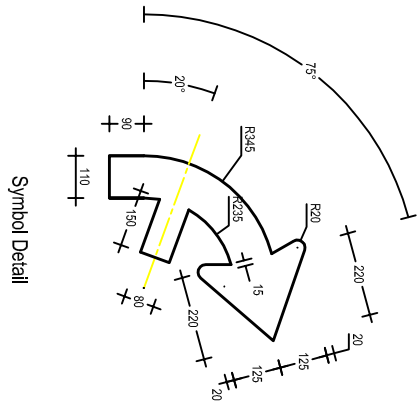
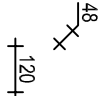
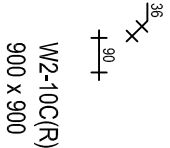
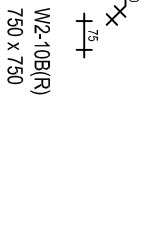
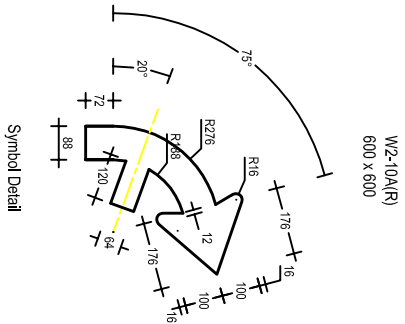


ALL DIMENSIONS ARE IN MILLIMETRES UNLESS OTHERWISE SPECIFIED				SIGN TO BE MANUFACTURED IN ACCORDANCE WITH RMS QA SPECIFICATION 3400				DRAWING FILE LOCATION / NAME: H:\SIGN\TTP\DRAWINGS\SPLOTTING\W2-10.DWG				DESIGNED				VERIFIED				WARNING SIGN				W2-10(R)				SIDE ROAD JUNCTION ON CURVE				INSIDE (Right Symbolic)				SHEET 1 OF 1				SCALE: 1:20				EDMS No. XXXXXXXX				SHEET No. 1				ISSUE 01				A3	
OR CODE				SIGN TO CHECK				REVISION				DATE				AMENDMENT / REVISION DESCRIPTION				APPROVAL				DRAWING FILE LOCATION / NAME: H:\SIGN\TTP\DRAWINGS\SPLOTTING\W2-10.DWG				DESIGNED				VERIFIED				WARNING SIGN				W2-10(R)				SIDE ROAD JUNCTION ON CURVE				INSIDE (Right Symbolic)				SHEET 1 OF 1				SCALE: 1:20				EDMS No. XXXXXXXX				SHEET No. 1				ISSUE 01				A3	
01				22-09-18				AS Form & material classification revised				P. Oliver				MATERIALS: ALUMINIUM SIGN BLACK SYMBOL AND BORDER ON AS1906.1 CL.400 YELLOW REFLECTORISED GROUND				SIGNATURE: M. Davies DATE: 31-07-19				SIGNATURE: P. Oliver DATE: 31-07-19				TITLE: Manager, Guidance & Delineation				PREPARED BY: J. Rozos				GUIDANCE AND DELINEATION UNIT				TRAFFIC ENGINEERING SERVICES				TECHNICAL AND PROJECT SERVICES				WARNING SIGN				W2-10(R)				SIDE ROAD JUNCTION ON CURVE				INSIDE (Right Symbolic)				SHEET 1 OF 1				SCALE: 1:20				EDMS No. XXXXXXXX				SHEET No. 1				ISSUE 01				A3	

ACCEPTED FOR CONSTRUCTION

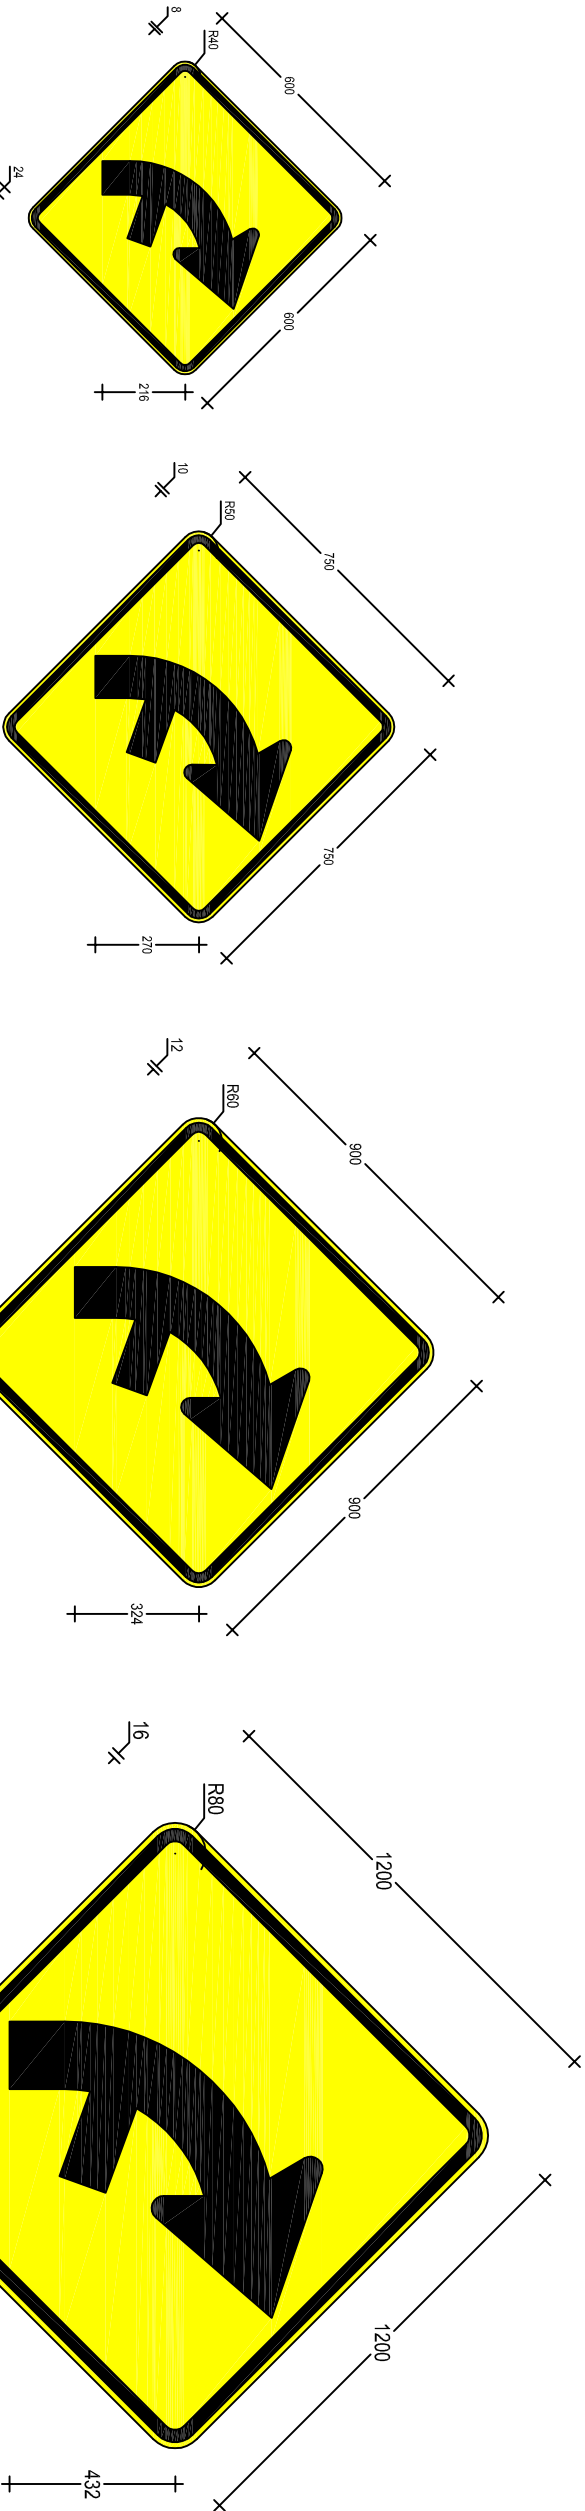

Symbol Detail