
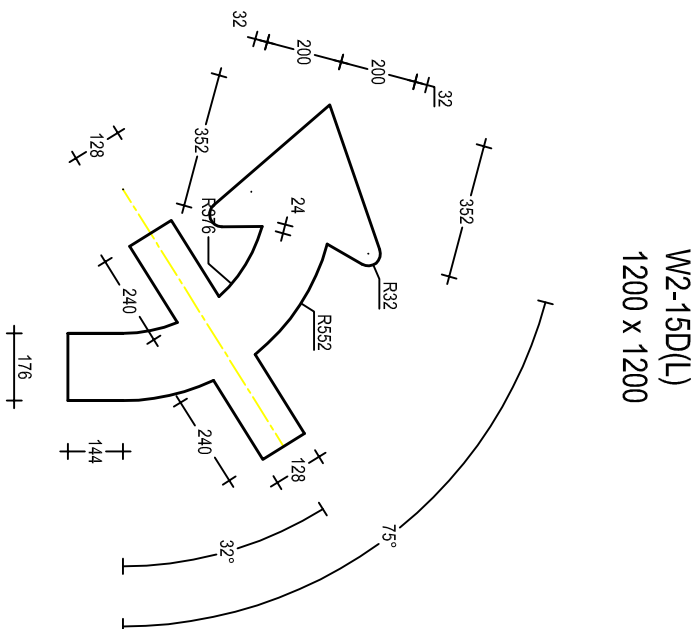
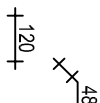
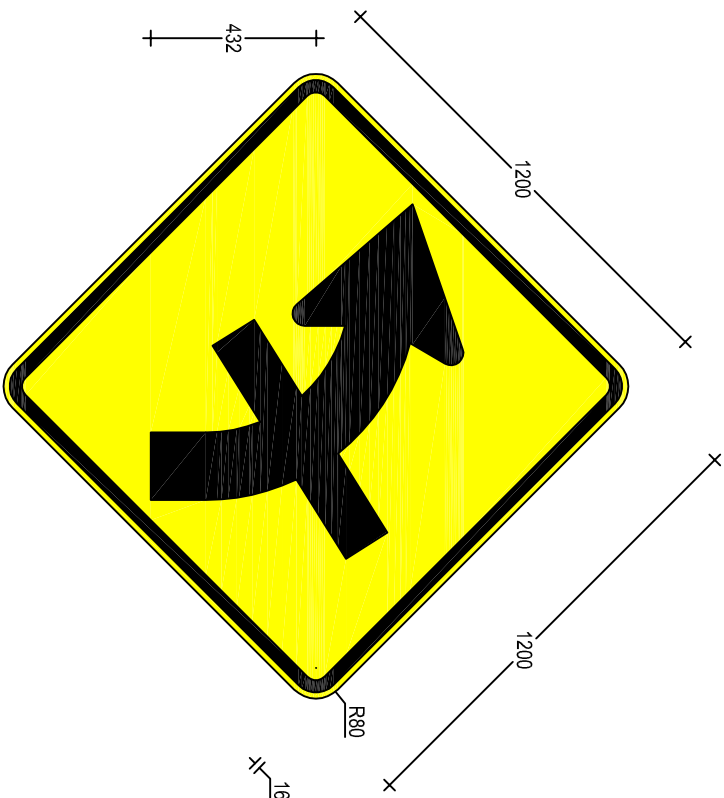
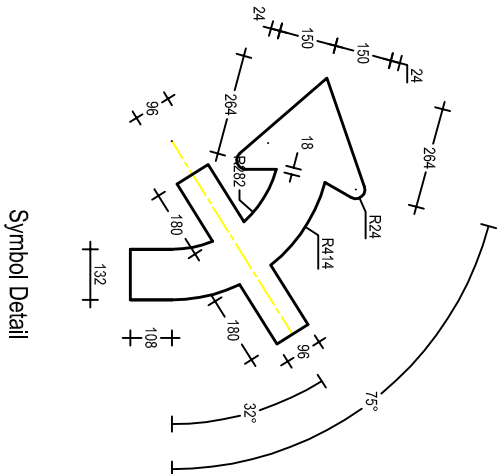
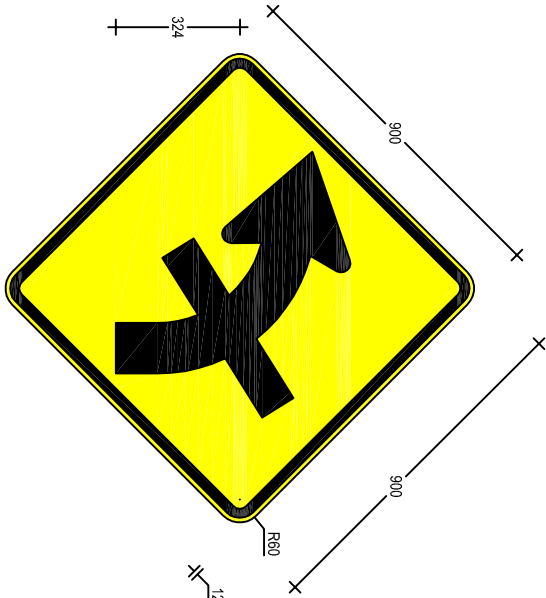
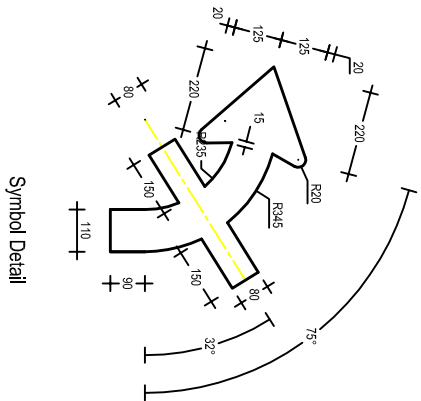
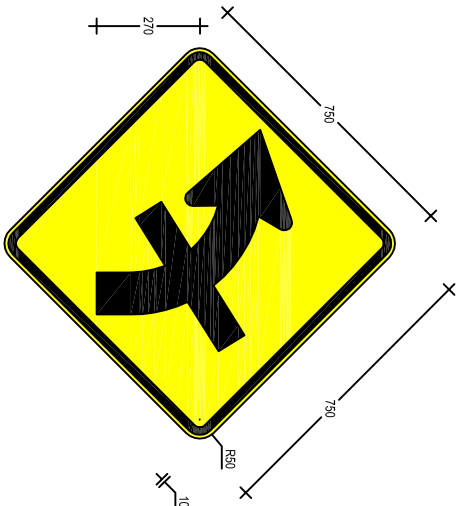
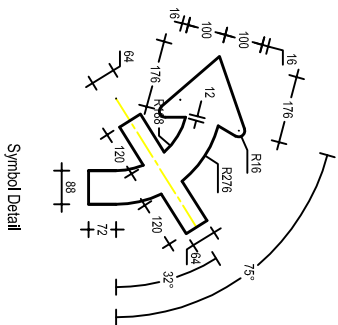


OR CODE		Scan to Check Document Version		REV	DATE	AMENDMENT / REVISION DESCRIPTION	APPROVAL	DRAWING FILE LOCATION / NAME: H:\SIGNS\ITTDRAWING\MSP\OTW\ARMW2-15\LDMG	DESIGNED	VERIFIED	WARNING SIGN W2-15(L) CROSSROAD ON CURVE (Left Symbolic)		A3	
				01	22-06-18	AS Fonts & material classification revised	P Oliver	MATERIALS: ALUMINIUM SIGN BLACK SYMBOL AND BORDER ON AS1906.1 CL.400 YELLOW REFLECTORISED GROUND	SIGNED NAME: M.Davies DATE: 31-07-19 REVIEWED SIGNED NAME: J.Rozzini DATE: 31-07-19	SIGNED NAME: P. Oliver TITLE: Manager Guidance & Delineation DATE: 31-07-19	SHEET 1 OF 1		EDMS No. XXXXXXXXXX SHEET No. 1 SCALE: 1:20	
ALL DIMENSIONS ARE IN MILLIMETRES UNLESS OTHERWISE SPECIFIED									SIGN TO BE MANUFACTURED IN ACCORDANCE WITH RMS QA SPECIFICATION 3400					

ACCEPTED FOR CONSTRUCTION

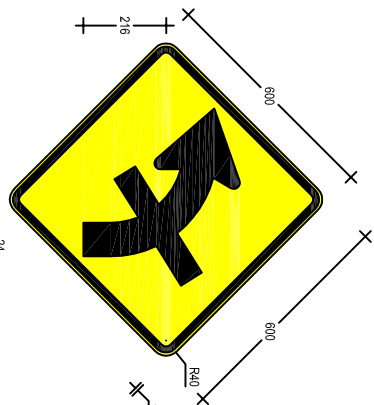

Symbol Detail