


0	5	10	15	20	25	30	35	40	45
OR CODE							Scan to Check Document Version		
REV							DATE		
AMENDMENT / REVISION DESCRIPTION							APPROVAL		
AS Forms & material classification revised							P.Oliver		
DRAWING FILE LOCATION / NAME: H:\SIGN\T\T\DRAWINGS\P\LOT\WARN\W211-2\DWG							DESIGNED		
SIGNED							NAME		
DATE							31-07-19		
REVIEWED							SIGNED		
NAME							J. Rozos		
DATE							31-07-19		
VERIFIED							SIGNED		
NAME							P.Oliver		
TITLE							Manager Guidance & Definition		
DATE							31-07-19		
PREPARED BY							GUIDANCE AND DELINEATION UNIT		
TRAFFIC ENGINEERING SERVICES							TECHNICAL AND PROJECT SERVICES		
WARNING SIGN							W2-211-2N		
CURVED ROAD SIDE ROAD JUNCTION RIGHT							(Symbolic) & REDUCE SPEED		
SCALE: 1:25							SHEET 1 OF 1		
EDMS No.							XXXXXXX		
SHEET No.							1		
ISSUE							01		

ACCEPTED FOR CONSTRUCTION

A3

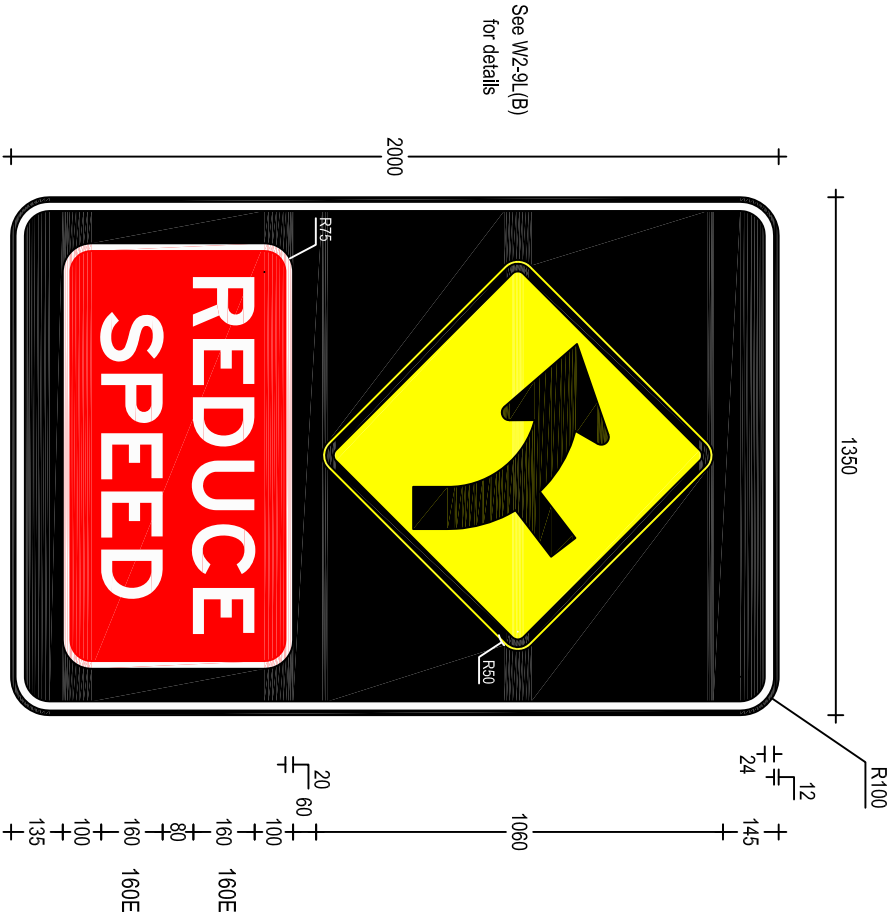


See W2-9L(B)
for details



W2-211-2n(B) (Option 2)
1350 x 2000

See W2-9R(B)
for details

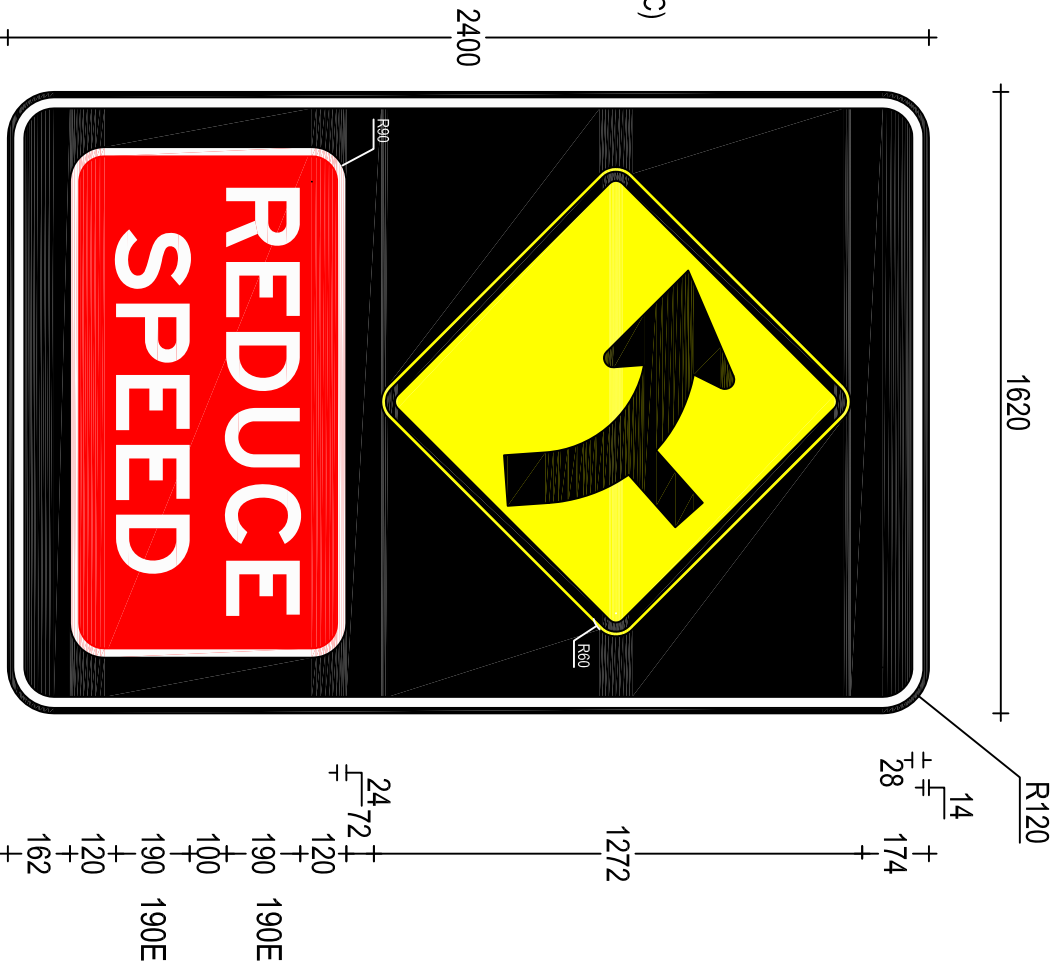

See W2-9L(C)
for details



W2-211-2n(C) (Option 2)
1620 x 2400

See W2-9R(C)
for details

W2-211-1n(B) (Option 1)
1350 x 2000

W2-211-1n(C) (Option 1)
1620 x 2400