
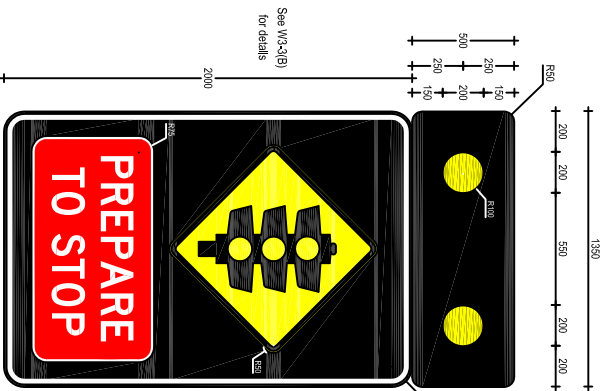


0	5	10	15	20	25	30	35	40	45	50mm ON A3 SIZE ORIGINAL			
PC CODE	REF	DATE	AMENDMENT / REVISION DESCRIPTION	APPROVAL	DRAWING FILE LOCATION NAME	DESIGNED	VERIFIED	PREPARED BY	WARNING SIGN	SCALE: 1:25	EDWG No.	SHEET No.	ISSUE
W3-204-1n	01	23-06-18	As Form & material specification revised	P. Oliver	W3-204-1n	NAME: Madeline DATE: 31-07-19	SIGNED: P. Oliver NAME: P. Oliver TITLE: Manager Guidance & Definition DATE: 31-07-19	TRANSPORT Roads & Maritime Services NSW Guidance and Delineation Unit Traffic Engineering Services Technical and Project Services	W3-204-1N TRAFFIC SIGNALS / PREPARE TO STOP with FLASHING LANTERNS	SCALE: 1:25	XXXXXXX	1	01
ALL DIMENSIONS ARE IN MILLIMETRES UNLESS OTHERWISE SPECIFIED											SHEET 1 OF 1		© Roads and Maritime Services

ACCEPTED FOR CONSTRUCTION

Note:- Lantems to Flash alternately when
ambered is showing on traffic signals

W3-204-1n(B) (Option 1) with Flashing Lantems
1350 x 2500

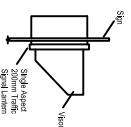



See W3-3(B)
for details



See W3-3(C)
for details



W3-204-1n(C) (Option 1) with Flashing Lantems
1620 x 2900

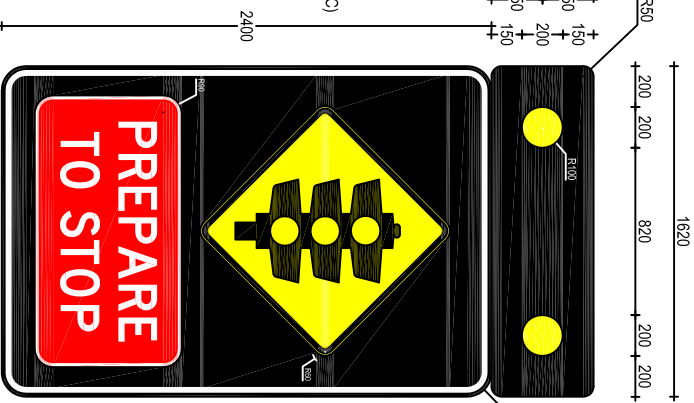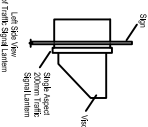

Note:- Lantems to Flash alternately when
ambered is showing on traffic signals

W3-204-5n(C) (Option 5)
1620 x 2400