


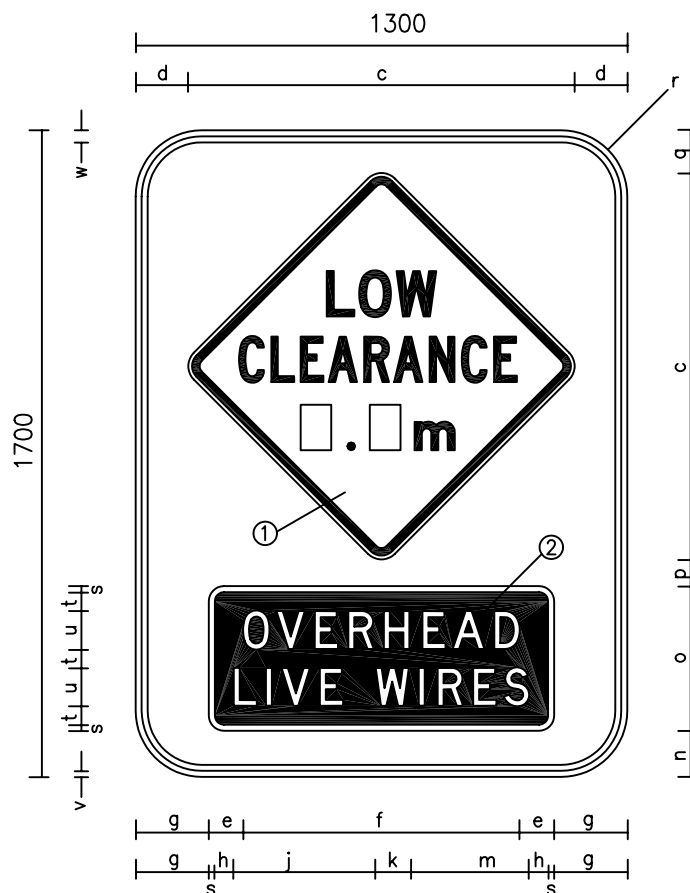

Cl.1 white reflectorised border on Cl.1 Standard green reflectorised ground.

① Black symbol and border on Cl.1 yellow reflectorised ground.

② Cl.1 white reflectorised legend and border on Cl.1 red reflectorised ground.

For Warning Sign use W4-8B.

	a	b	c	d	e	f	g	h	j	k	m	n
W3-205	1300	1700	1020	140	163	730	122	50	445	94	385	120

o	p	q	r	s	t	u	v	w
382	68	110	175	16	50	100DM	16	32

Scale 1:20

TITLE

WARNING SIGN
W3-205-1

Date: 18/02/98

Checked: —

Drawn: F.R.

Revision: —



File (Sign) K:\TTT\DRAWINGS\LOT\WARNING\W3-205-1.dwg