


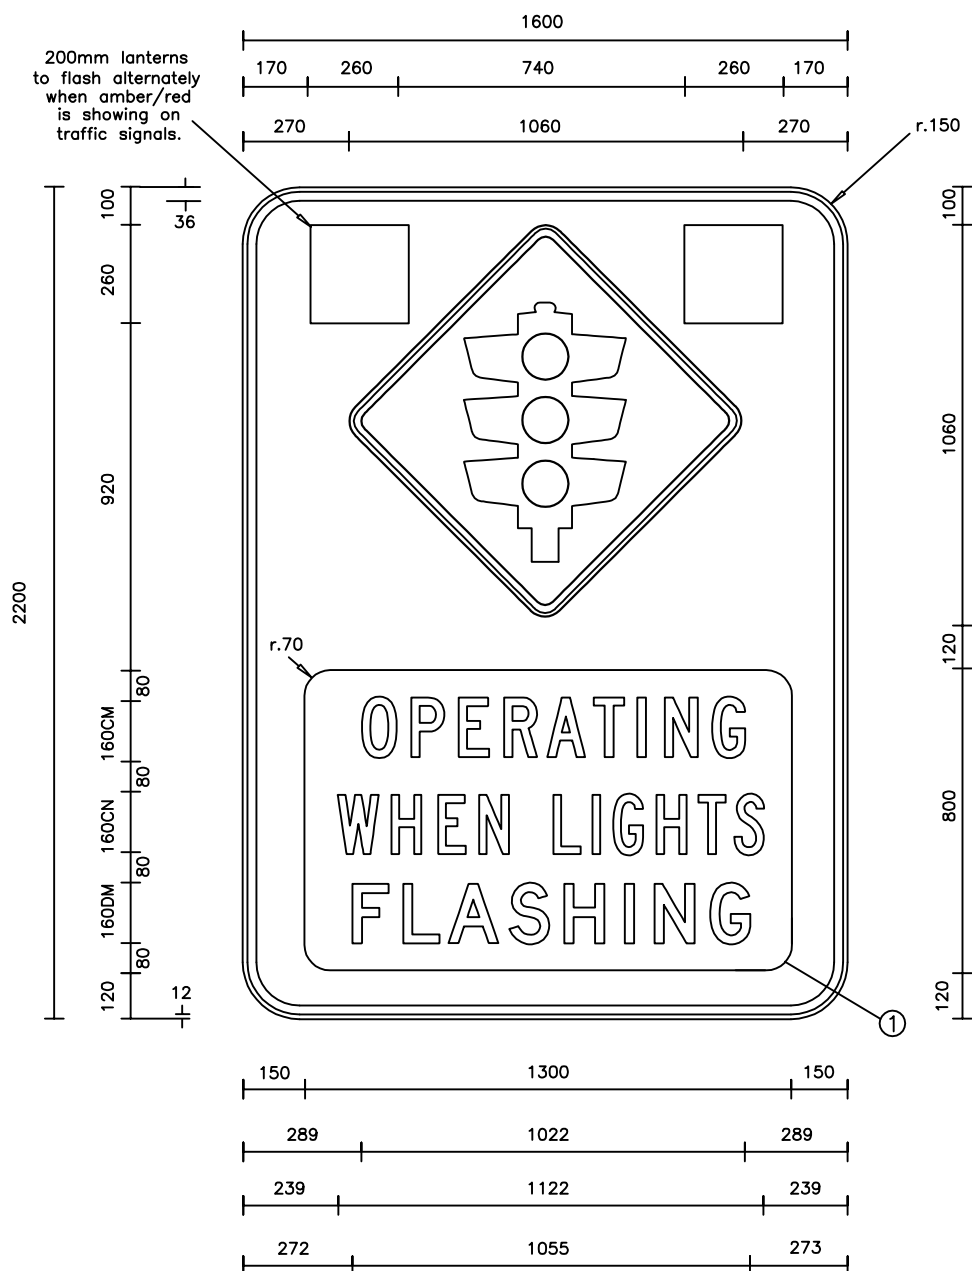

Black symbol, legend and border on Cl.1 yellow reflectorised ground.

① Black legend on Cl.1 White reflectorised ground.

For Traffic Light symbol use W3-3B.

Note: Circles in symbol to all be yellow as in AS 1742 Part 1.

SCALE:1:20

TITLE

WARNING SIGN
W3-207-1

Date: 28/05/09

Checked: FR

Drawn: VPALMER

Revision: 1

File (Sign) K:\TTT\DRAWINGS\LOT\WARNING\W3-207-1

