
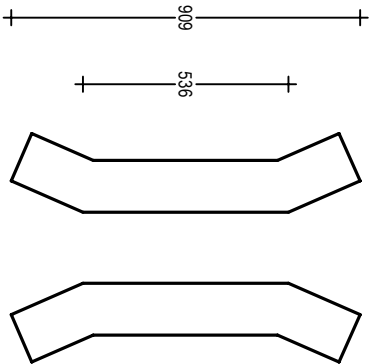
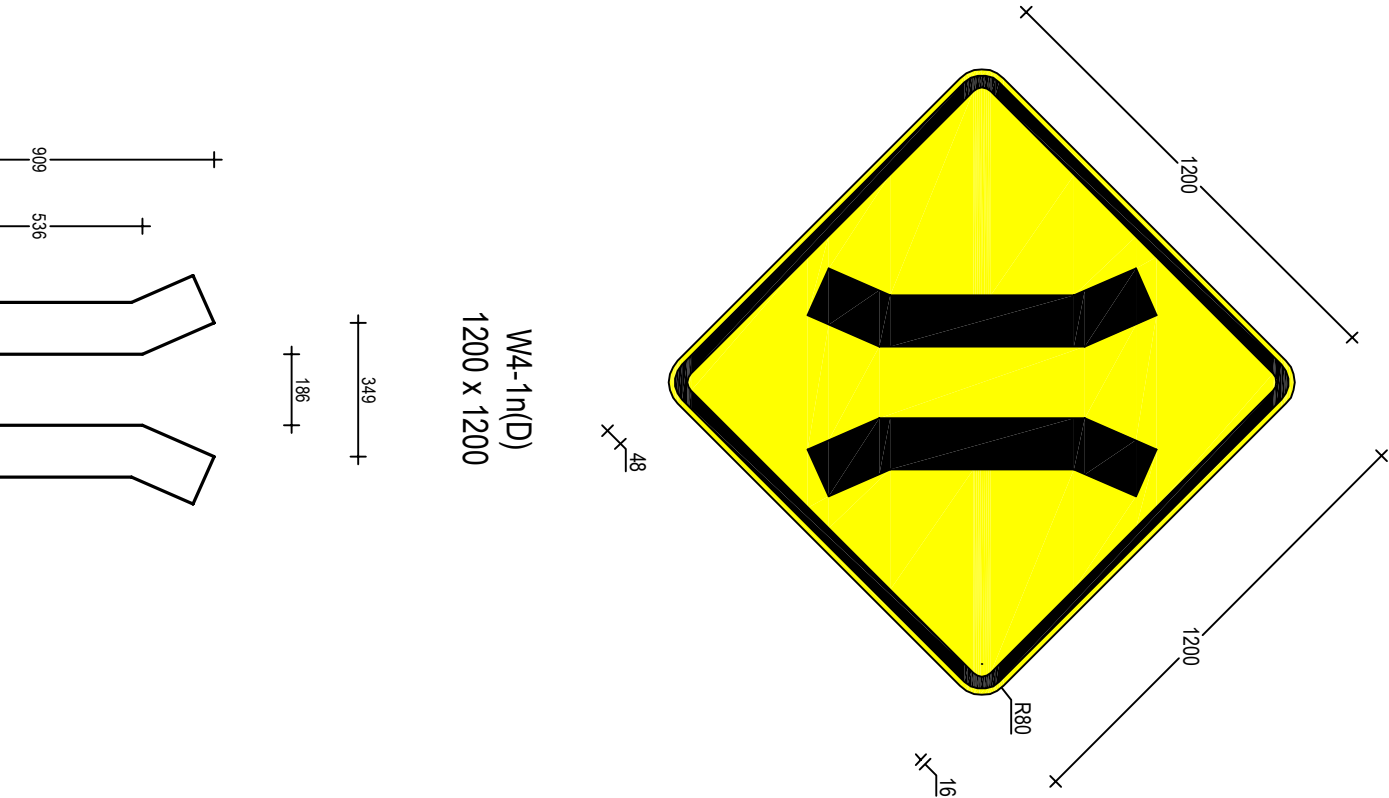
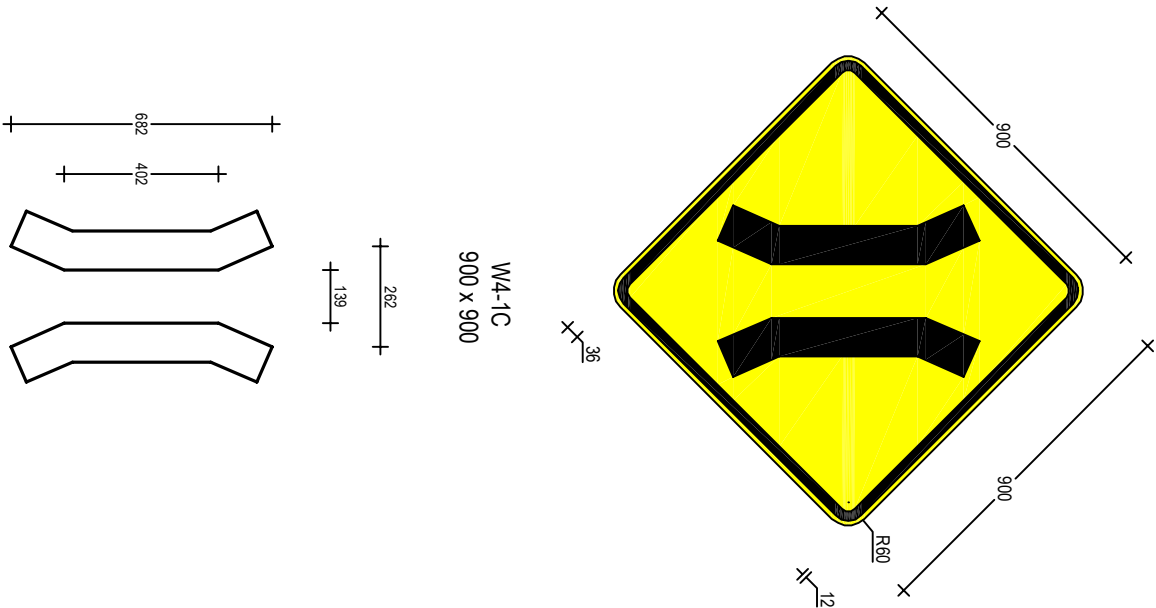
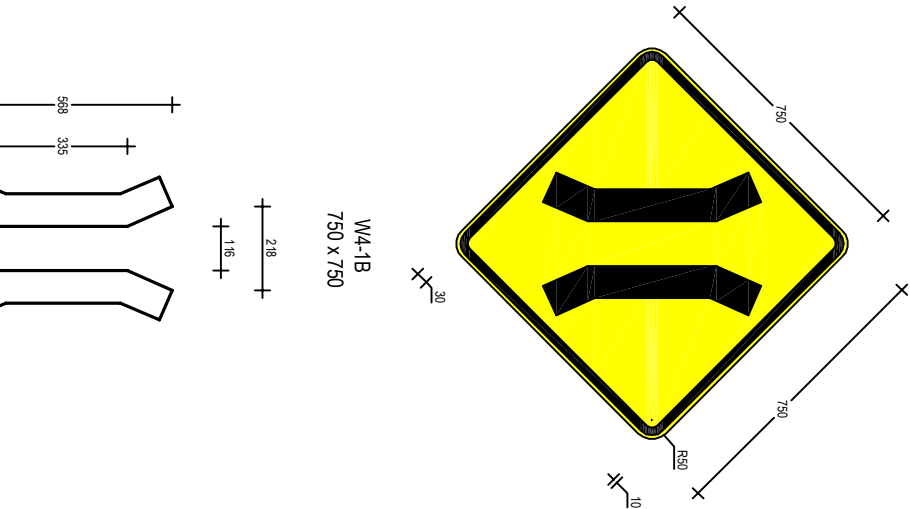


05101520253035404550mm ON A3 SIZE ORIGINAL

OR CODE	Scan to Check Document Version	REV	DATE	AMENDMENT / REVISION DESCRIPTION	APPROVAL	DRAWING FILE LOCATION / NAME: H:\SIGNS\TTP\DRAWINGS\PI\OTWARR\W4-1.DWG
		01	23-08-18	AS Fonts & material classification revised	P Oliver	
ALL DIMENSIONS ARE IN MILLIMETRES UNLESS OTHERWISE SPECIFIED						SIGN TO BE MANUFACTURED IN ACCORDANCE WITH RMS QA SPECIFICATION 3400
DESIGNED						VERIFIED
SIGNED:  NAME: M. Davies DATE: 31-07-19						SIGNED:  NAME: P. Oliver TITLE: Manager, Guidance & Delineation DATE: 31-07-19
REVIEWED SIGNED:  NAME: J. Rozdos DATE: 31-07-19						PREPARED BY GUIDANCE AND DELINEATION UNIT TRAFFIC ENGINEERING SERVICES TECHNICAL AND PROJECT SERVICES
MATERIALS: ALUMINIUM SIGN BLACK SYMBOL AND BORDER ON AS1906.1 CL.400 YELLOW REFLECTORISED GROUND						WARNING SIGN W4-1 NARROW BRIDGE (Symbolic)
SCALE: 1:20						EDMS No. XXXXXXXXXX SHEET No. 1 ISS 0
						SHEET 1 OF 1

ACCEPTED FOR CONSTRUCTION

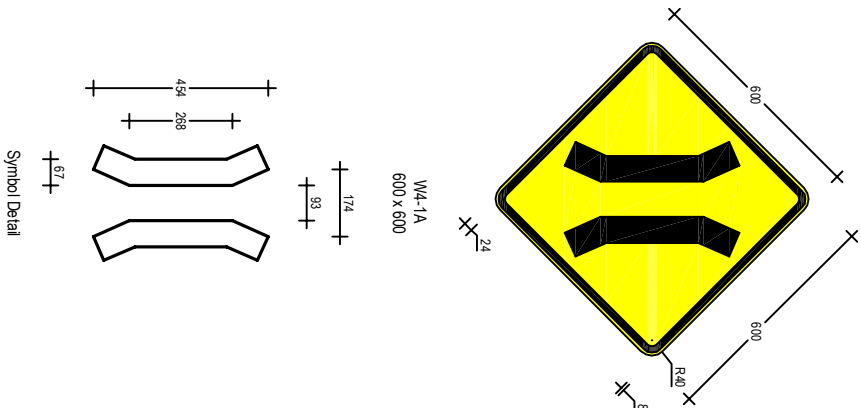

Symbol Detail