


5101520253035404550mm ON A3 SIZE ORIGINAL

OR CODE		Scan to Check Document Version		REV	DATE	AMENDMENT / REVISION DESCRIPTION		APPROVAL		DRAWING FILE LOCATION / NAME: H:\SIGNS\TTT\DRAWINGS\PI\OTWARR\W5-1.DWG	
		01		23-08-18		AS Fonts & material classification revised		P Oliver		MATERIALS: ALUMINIUM SIGN BLACK LEGEND AND BORDER ON AS1906.1 CL.400 YELLOW REFLECTORISED GROUND	
ALL DIMENSIONS ARE IN MILLIMETRES UNLESS OTHERWISE SPECIFIED										SIGN TO BE MANUFACTURED IN ACCORDANCE WITH RMS QA SPECIFICATION 3400	
DESIGNED		VERIFIED		PREPARED BY		WARNING SIGN		A			
SIGNED: M Davies NAME: M Davies DATE: 31-07-19		SIGNED: P Oliver NAME: P Oliver TITLE: Manager, Guidance & Delineation DATE: 31-07-19		NSW GOVERNMENT Transport Roads & Maritime Services		W5-1 FERRY		SHEET 1 OF 1			
SIGNED: J Rozdos NAME: J Rozdos DATE: 31-07-19		PREPARED BY GUIDANCE AND DELINEATION UNIT TRAFFIC ENGINEERING SERVICES TECHNICAL AND PROJECT SERVICES		SCALE: 1:20		EDMS No. XXXXXXXXXX		SHEET No. 1			
								ISS 0			

ACCEPTED FOR CONSTRUCTION

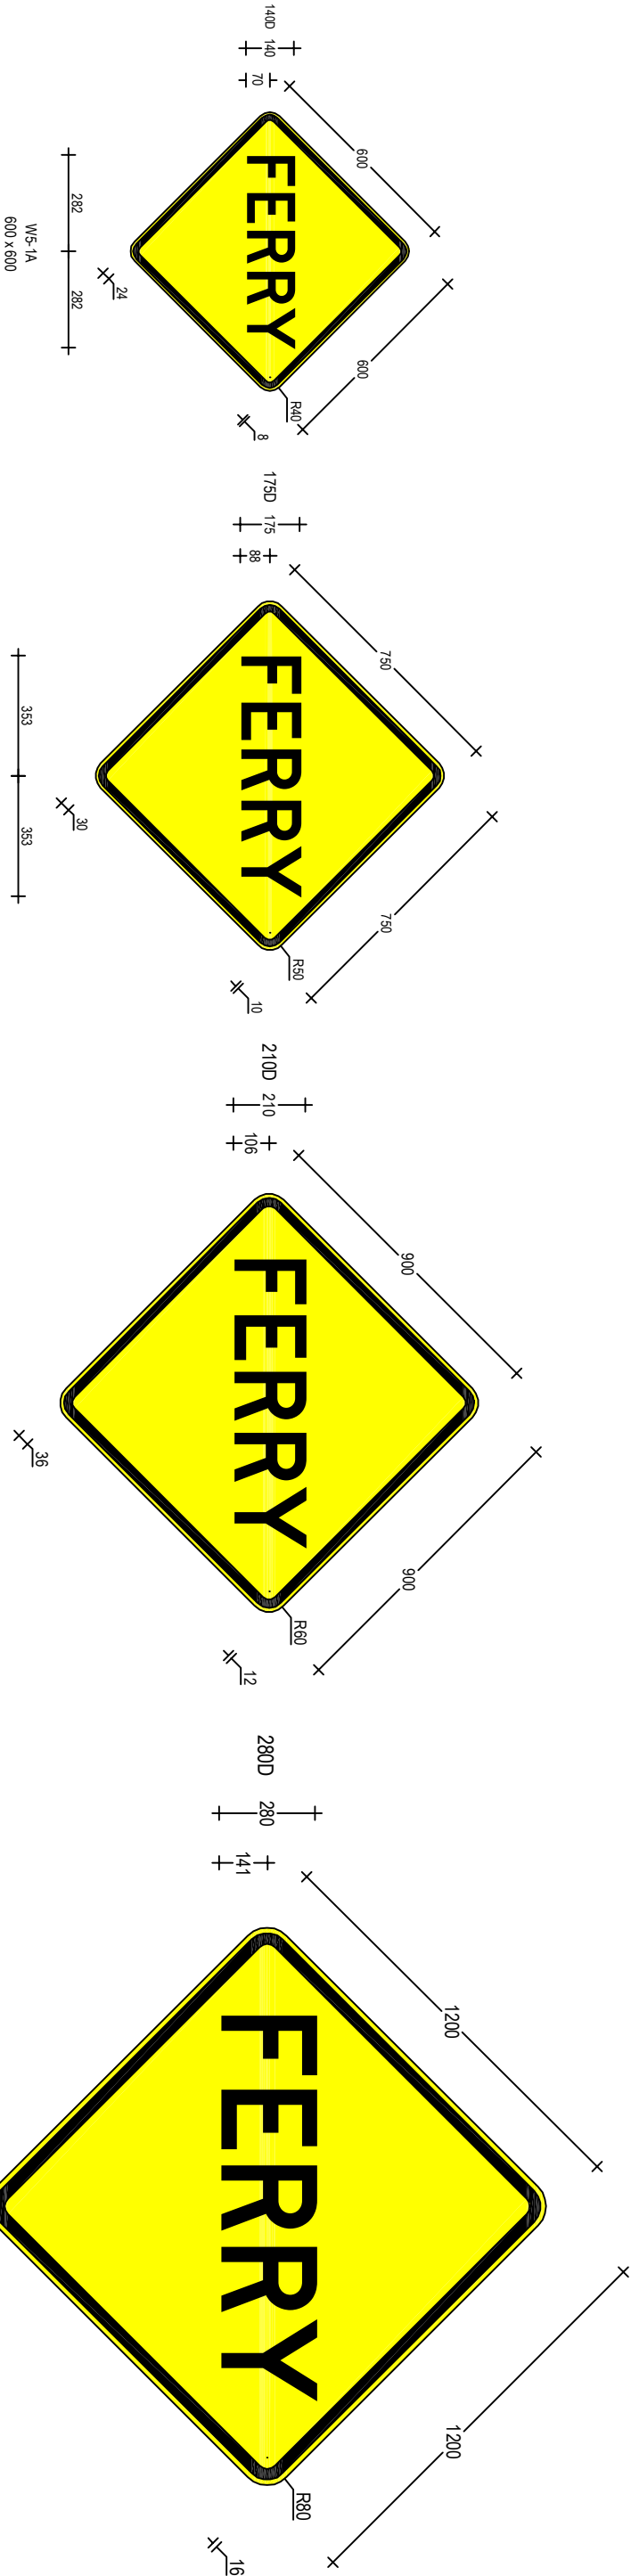

W5-1n(D)
1200 x 1200