


50mm ON A3 SIZE ORIGINAL

0	5	10	15	20	25	30	35	40	45
OR CODE									
Scan to Check Document Version									
REV		DATE		AMENDMENT / REVISION DESCRIPTION				APPROVAL	
01		23-08-18		AS Fonts & material classification revised				P Oliver	
DRAWING FILE LOCATION / NAME: H:\SIGNS\TTT\DRAWINGS\RP\OTWARR\W5-14.DWG									
MATERIALS: ALUMINIUM SIGN BLACK LEGEND AND BORDER ON AS1906.1 CL.400 YELLOW REFLECTORISED GROUND									
SIGN TO BE MANUFACTURED IN ACCORDANCE WITH RMS QA SPECIFICATION 3400									
DESIGNED					VERIFIED				
SIGNED NAME: M Davies DATE: 31-07-19					SIGNED NAME: P Oliver DATE: 31-07-19				
REVIEWED NAME: J Rozdos DATE: 31-07-19					TITLE: Manager, Guidance & Delineation				
PREPARED BY GUIDANCE AND DELINEATION UNIT TRAFFIC ENGINEERING SERVICES TECHNICAL AND PROJECT SERVICES					NSW GOVERNMENT Transport Roads & Maritime Services				
SCALE: 1:15					WARNING SIGN W5-14 GATE				
EDMS No. XXXXXXXXXX					SHEET No. 1				
ISS 0					SHEET 1 OF 1				

ACCEPTED FOR CONSTRUCTION

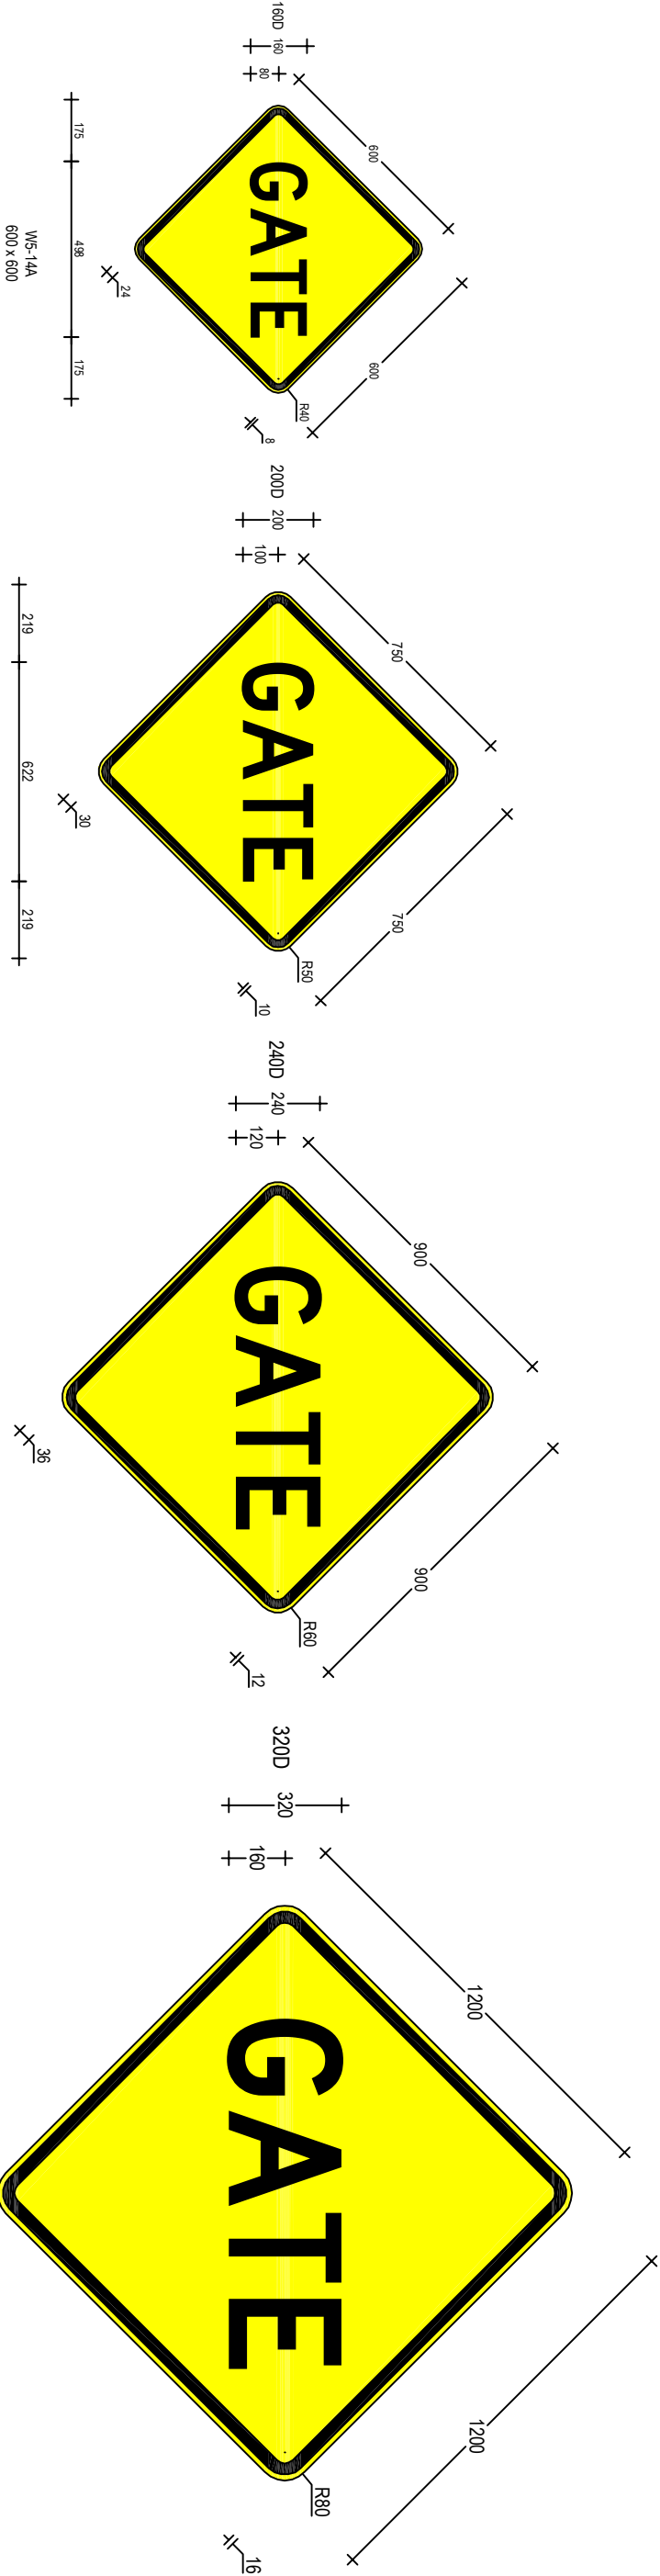

W5-14n(D)
1200 x 1200