


50mm ON A3 SIZE ORIGINAL

OR CODE		Scan to Check Document Version		REV	DATE	AMENDMENT / REVISION DESCRIPTION		APPROVAL	DRAWING FILE LOCATION / NAME: H:\SIGNS\TTT\DRAWINGS\SP\OTWARR\W5-16.DWG		
				01	23-08-18	AS Fonts & material classification revised		P Oliver	MATERIALS: ALUMINIUM SIGN BLACK LEGEND AND BORDER ON AS1906.1 CL 400 YELLOW REFLECTORISED GROUND		
ALL DIMENSIONS ARE IN MILLIMETRES UNLESS OTHERWISE SPECIFIED										SIGN TO BE MANUFACTURED IN ACCORDANCE WITH RMS QA SPECIFICATION 3400	
		DESIGNED		SIGNED	M. Davies		DATE		31-07-19		
		REVIEWED		SIGNED	J. Rozdos		DATE		31-07-19		
		VERIFIED		SIGNED	P Oliver		DATE		31-07-19		
				TITLE		Manager Guidance & Delineation		DATE		31-07-19	
				PREPARED BY		GUIDANCE AND DELINEATION UNIT		TRAFFIC ENGINEERING SERVICES		TECHNICAL AND PROJECT SERVICES	
				NSW GOVERNMENT		Transport Roads & Maritime Services					
										WARNING SIGN	
										W5-16 GRID	
										SCALE: 1:20	
										EDMS No. XXXXXXXXX	
										SHEET No. 1	
										ISS 0	
										SHEET 1 OF 1	

© Roads and Maritime Service

ACCEPTED FOR CONSTRUCTION

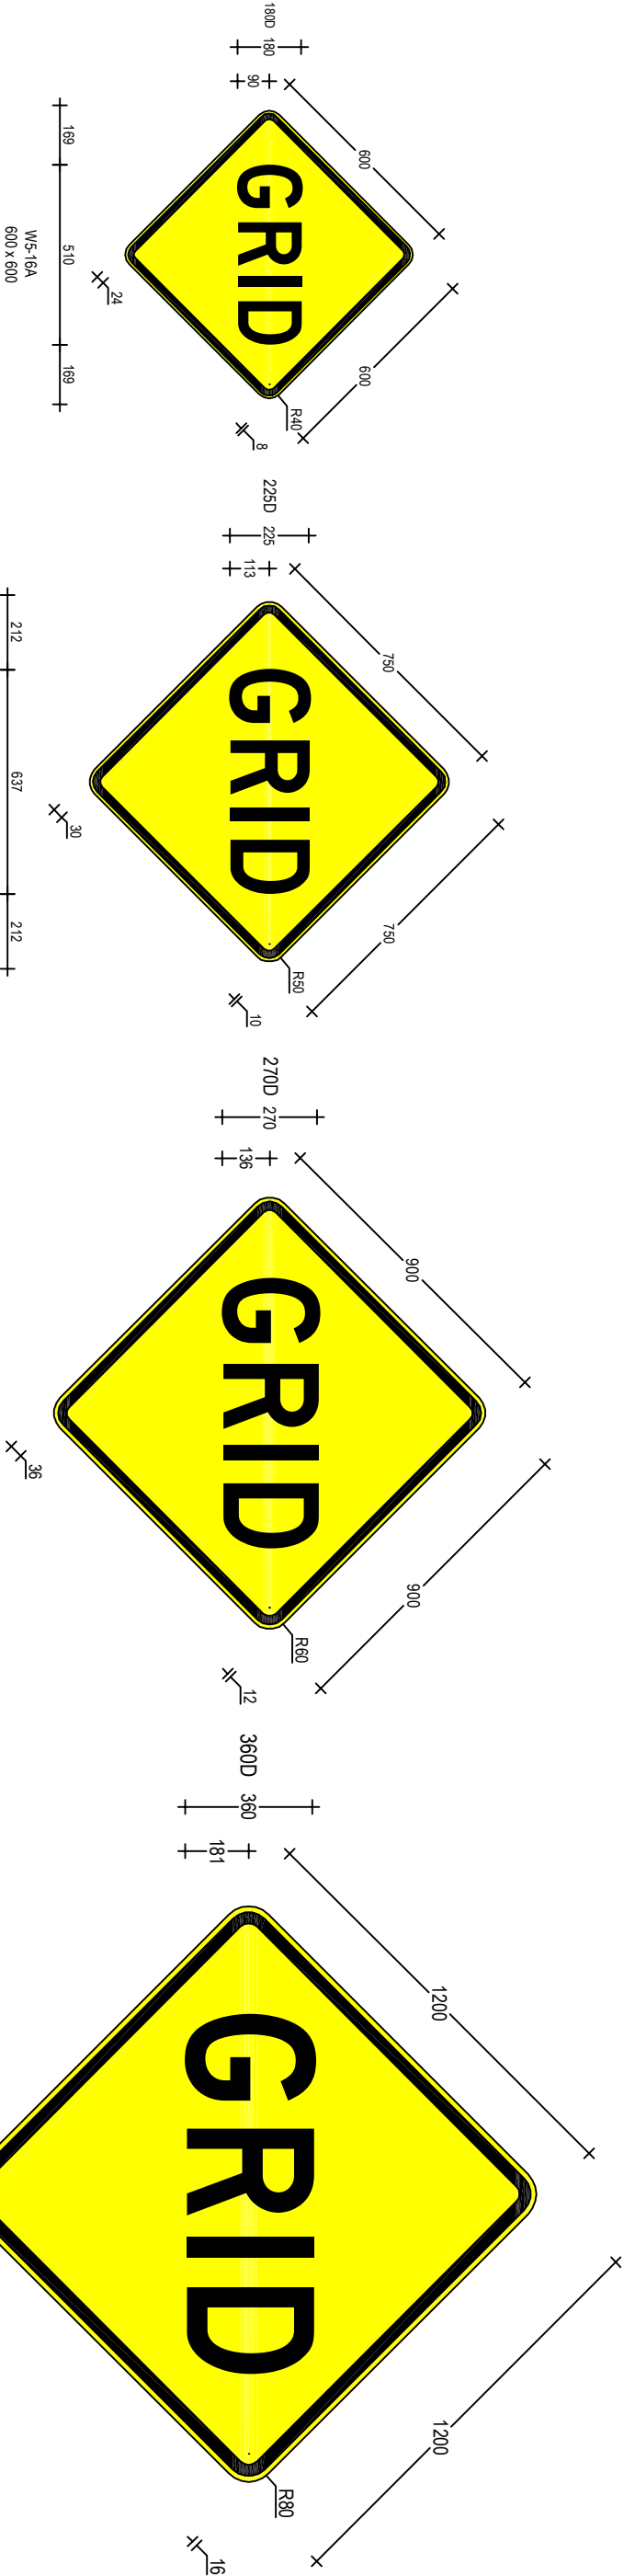

W5-16n(D)
1200 x 1200