


05101520253035404550mm ON A3 SIZE ORIGINAL

OR CODE	Scan to Check Document Version	REV	DATE	AMENDMENT / REVISION DESCRIPTION	APPROVAL	DRAWING FILE LOCATION / NAME: H:\SIGNS\TTT\DRAWINGS\PI\OTWARR\W5-18.DWG
		01	23-08-18	AS Fonts & material classification revised	P Oliver	
ALL DIMENSIONS ARE IN MILLIMETRES UNLESS OTHERWISE SPECIFIED						SIGN TO BE MANUFACTURED IN ACCORDANCE WITH RMS QA SPECIFICATION 3400
DESIGNED						SIGNED: M. Davies NAME: M. Davies DATE: 31-07-19 REVIEWED: J. Rozdos NAME: J. Rozdos DATE: 31-07-19
VERIFIED						SIGNED: P. Oliver NAME: P. Oliver TITLE: Manager, Guidance & Delineation DATE: 31-07-19
PREPARED BY						NSW GOVERNMENT Transport Roads & Maritime Services GUIDANCE AND DELINEATION UNIT TRAFFIC ENGINEERING SERVICES TECHNICAL AND PROJECT SERVICES
WARNING SIGN						W5-18 ROAD ENDS
SCALE: 1:20						EDMS No. XXXXXXXXXX SHEET No. 1 ISS 0

ACCEPTED FOR CONSTRUCTION

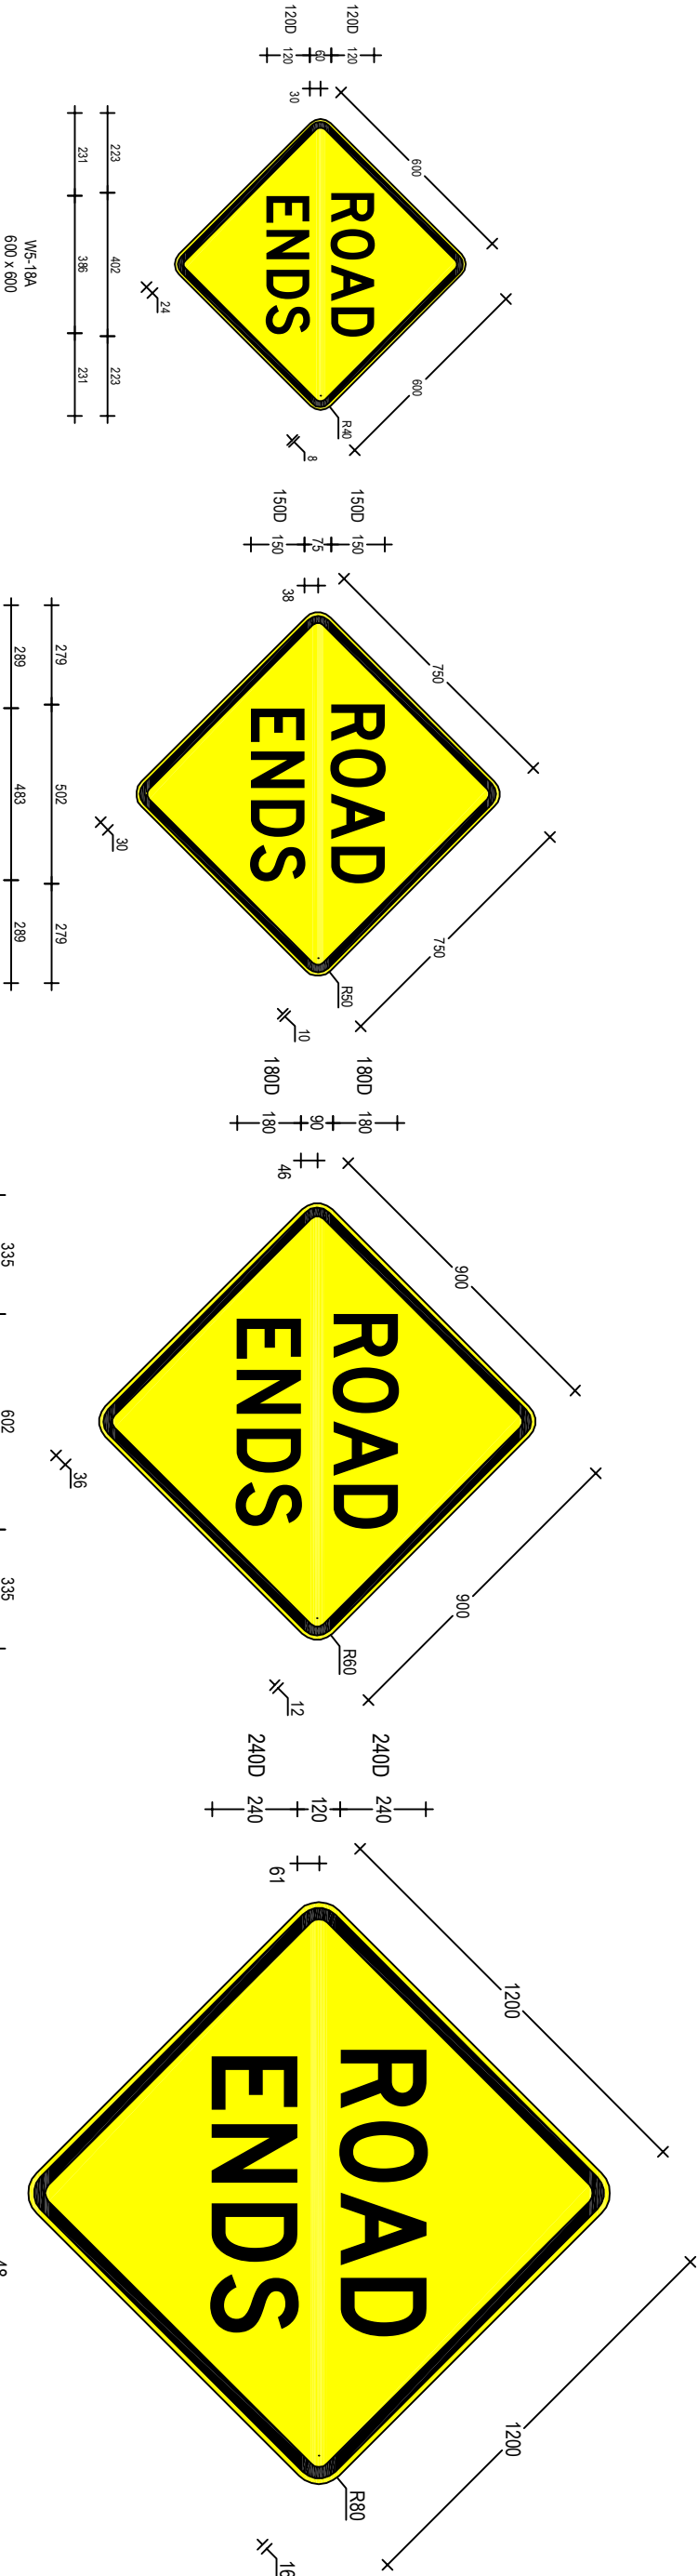

W5-18n(D)
1200 x 1200