



0510253035404550mm ON A3 SIZE ORIGINAL

OR CODE	Scan to Check Document Version	REV	DATE	AMENDMENT / REVISION DESCRIPTION	APPROVAL	DRAWING FILE LOCATION / NAME: H:\SIGNS\TTT\DRAWINGS\PL\OTWARR\W5-22N.DWG
		01	23-08-18	AS Fonts & material classification revised	P Oliver	
ALL DIMENSIONS ARE IN MILLIMETRES UNLESS OTHERWISE SPECIFIED						SIGN TO BE MANUFACTURED IN ACCORDANCE WITH RMS QA SPECIFICATION 3400
DESIGNED						VERIFIED
SIGNED: 						SIGNED: 
NAME: M. Davies						NAME: P. Oliver
DATE: 31-07-19						TITLE: Manager, Guidance & Delineation
REVIEWED						
SIGNED: 						
NAME: J. Rozdos						
DATE: 31-07-19						
PREPARED BY						SHEET 1 OF 1
GUIDANCE AND DELINEATION UNIT TRAFFIC ENGINEERING SERVICES TECHNICAL AND PROJECT SERVICES						
NSW GOVERNMENT Transport Roads & Maritime Services						WARNING SIGN W5-222N HUMP
SCALE: 1:10						EDMS No. XXXXXXXXXX
						SHEET No. 1
						ISS 0


ACCEPTED FOR CONSTRUCTION

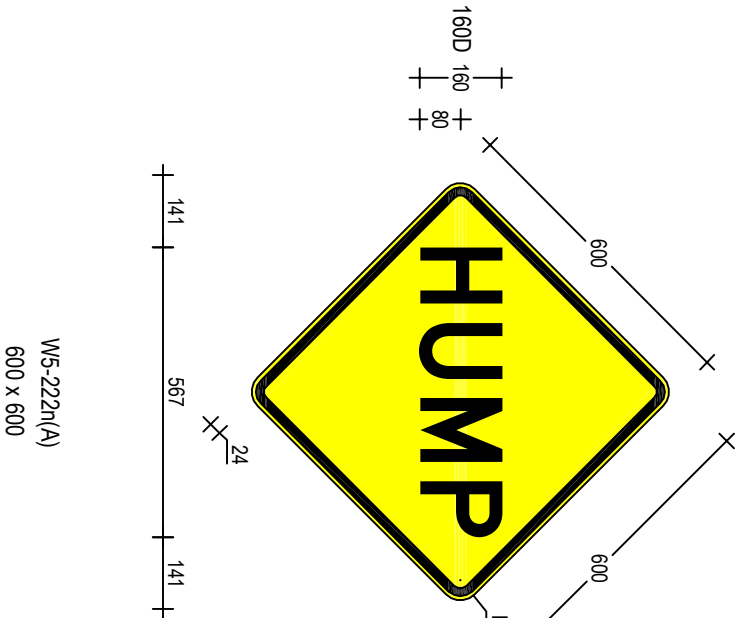

W5-222n(A)
600 x 600

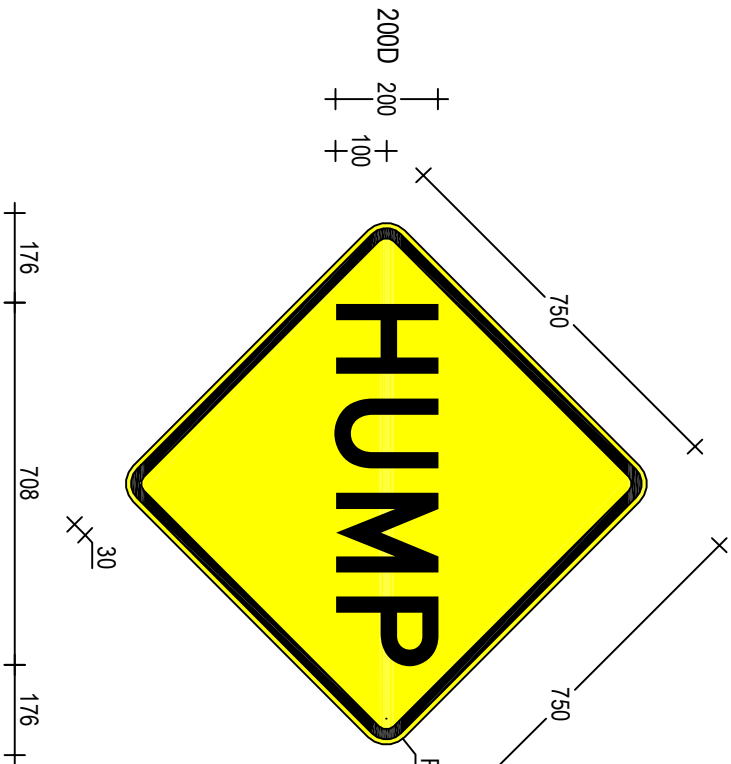

W5-222n(B)
750 x 750

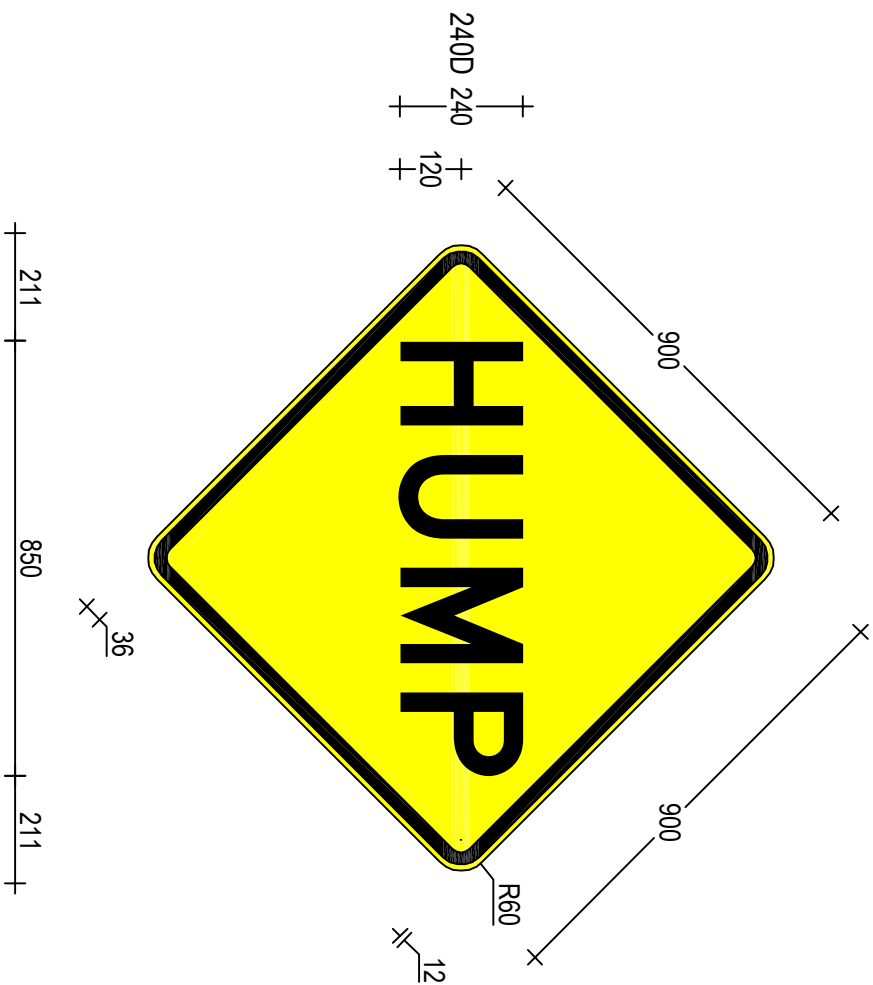

W5-222n(C)
900 x 900