



05101520253035404550mm ON A3 SIZE ORIGINAL

QR CODE	Scan to Check Document Version	REV	DATE	AMENDMENT / REVISION DESCRIPTION	APPROVAL	DRAWING FILE LOCATION / NAME: H:\SIGNS\TTT\DRAWINGS\PI\OTWARR\W5-235-1\DWG
		01	23-08-18	AS Fonts & material classification revised	P Oliver	
ALL DIMENSIONS ARE IN MILLIMETRES UNLESS OTHERWISE SPECIFIED						
SIGN TO BE MANUFACTURED IN ACCORDANCE WITH RMS QA SPECIFICATION 3400						
DESIGNED						
SIGNED: M Davies						
NAME: M Davies						
DATE: 31-07-19						
REVIEWED						
SIGNED: J Rozdos						
NAME: J Rozdos						
DATE: 31-07-19						
VERIFIED						
SIGNED: P Oliver						
NAME: P Oliver						
TITLE: Manager, Guidance & Delineation						
DATE: 31-07-19						
PREPARED BY						
GUIDANCE AND DELINEATION UNIT						
TRAFFIC ENGINEERING SERVICES						
TECHNICAL AND PROJECT SERVICES						
WARNING SIGN						
W5-235-1N						
LANES MERGE (Symbolic without centre barrier)						
SCALE: 1:15						
EDMS No. XXXXXXXXXX						
SHEET No. 1						
ISS						
0						
SHEET 1 OF 1						
A						


ACCEPTED FOR CONSTRUCTION

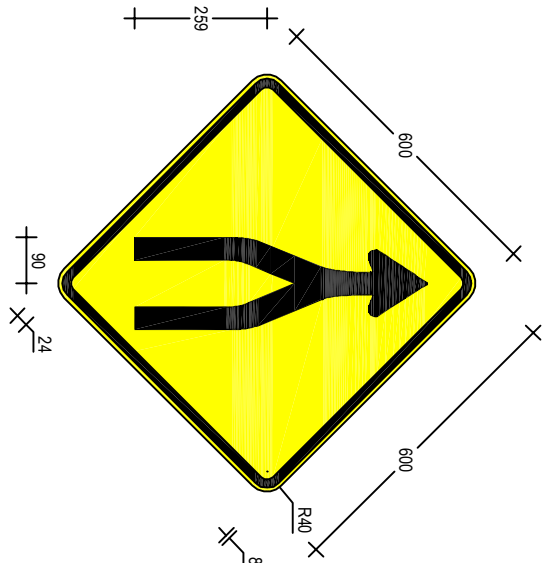


W5-235-1n(A)
600 x 600

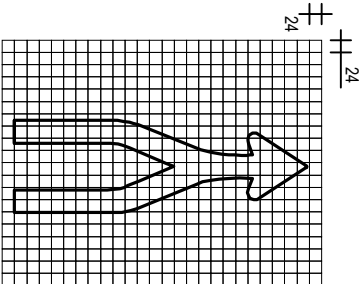


Symbol Detail

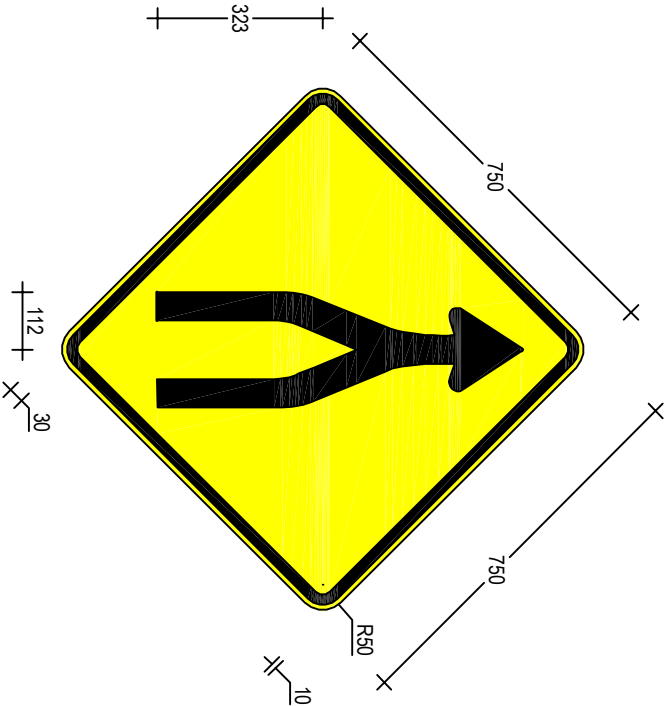


W5-235-1n(B)
750 x 750

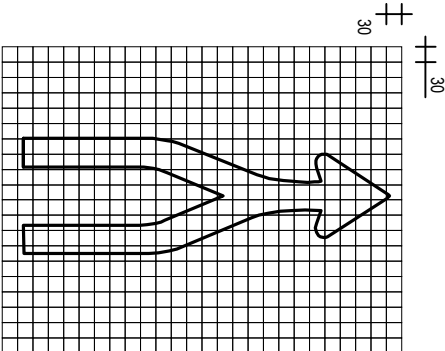

Symbol Detail

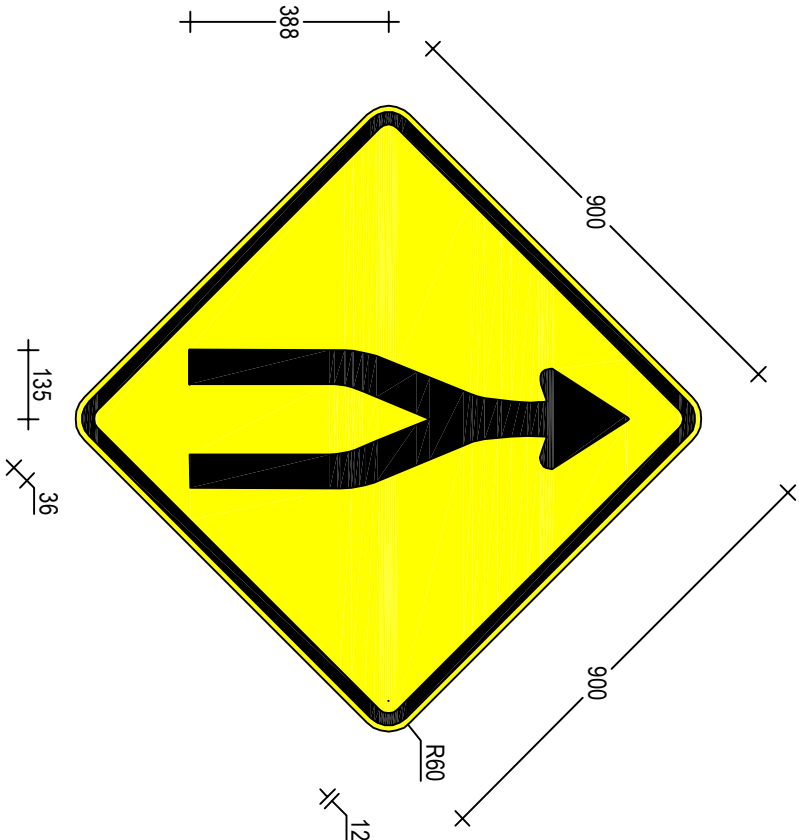

W5-235-1n(C)
1200 x 1200

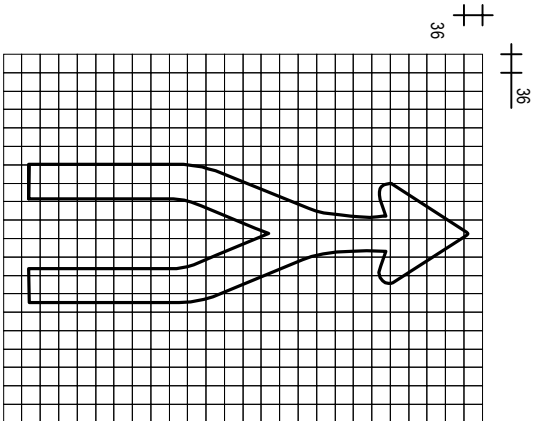

Symbol Detail