



0510253035404550mm ON A3 SIZE ORIGINAL

|         |  
|---------|--|--------------------------------|--|-----|----------|--------------------------------------------|----------|---|--|----------------------------------------------|--|---------------------------------------------------------------------|--|---|--|-----------------------------------------------------------------------|--|---------------------|--|-------------|--|-------|--|
| QR CODE |  | Scan to Check Document Version |  | REV | DATE     | AMENDMENT / REVISION DESCRIPTION           | APPROVAL | DRAWING FILE LOCATION / NAME: H:\SIGNS\TTT\DRAWINGS\PI\OTWARR\W5-235\DWG                                                                                 |  | DESIGNED                                     |  | VERIFIED                                                            |  | Transport NSW<br>Roads & Maritime Services                                                                     |  | WARNING SIGN<br>W5-235N<br>LANES MERGE (Symbolic with centre barrier) |  | EDMS No. XXXXXXXXXX |  | SHEET No. 1 |  | ISS 0 |  |
|         |  |                                |  | 01  | 23-08-18 | AS Fonts & material classification revised | P Oliver |   |  | SIGNED: M. Davies<br>NAME: 31-07-19<br>DATE: |  | SIGNED: P Oliver<br>NAME: 31-07-19<br>DATE:                         |  | PREPARED BY<br>GUIDANCE AND DELINEATION UNIT<br>TRAFFIC ENGINEERING SERVICES<br>TECHNICAL AND PROJECT SERVICES |  | SHEET 1 OF 1                                                          |  |                     |  |             |  |       |  |
|         |  |                                |  |     |          |                                            |          | MATERIALS: ALUMINIUM SIGN<br>BLACK SYMBOL AND BORDER<br>ON AS1906.1 CL.400 YELLOW REFLECTORISED GROUND<br>WITH AS1906.1 CL.400 RED REFLECTORISED BARRIER |  | SIGNED: J. Rozdos<br>NAME: 31-07-19<br>DATE: |  | TITLE: Manager, Guidance & Delineation<br>SIGNED: 31-07-19<br>DATE: |  |   |  | SCALE: 1:15                                                           |  |                     |  |             |  |       |  |
|         |  |                                |  |     |          |                                            |          | SIGN TO BE MANUFACTURED IN ACCORDANCE WITH RMS QA SPECIFICATION 3400                                                                                     |  |                                              |  |                                                                     |  |   |  |                                                                       |  |                     |  |             |  |       |  |
|         |  |                                |  |     |          |                                            |          | ALL DIMENSIONS ARE IN MILLIMETRES UNLESS OTHERWISE SPECIFIED                                                                                             |  |                                              |  |                                                                     |  |   |  |                                                                       |  |                     |  |             |  |       |  |
|         |  
ACCEPTED FOR CONSTRUCTION

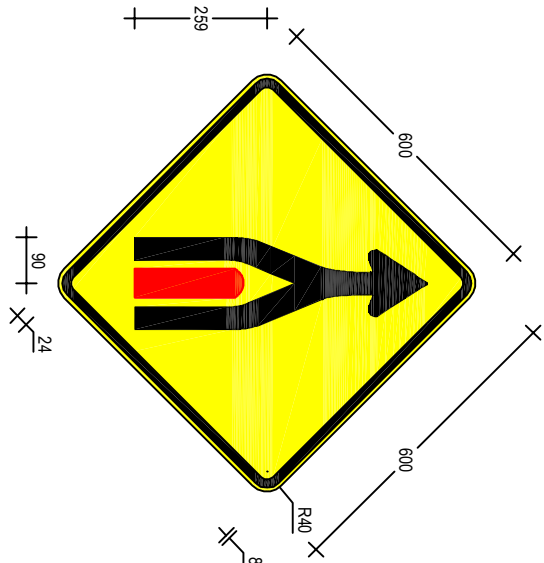


W5-235-1n(A)  
600 x 600

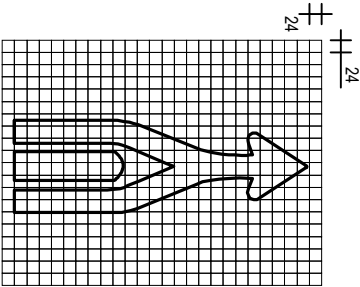


Symbol Detail

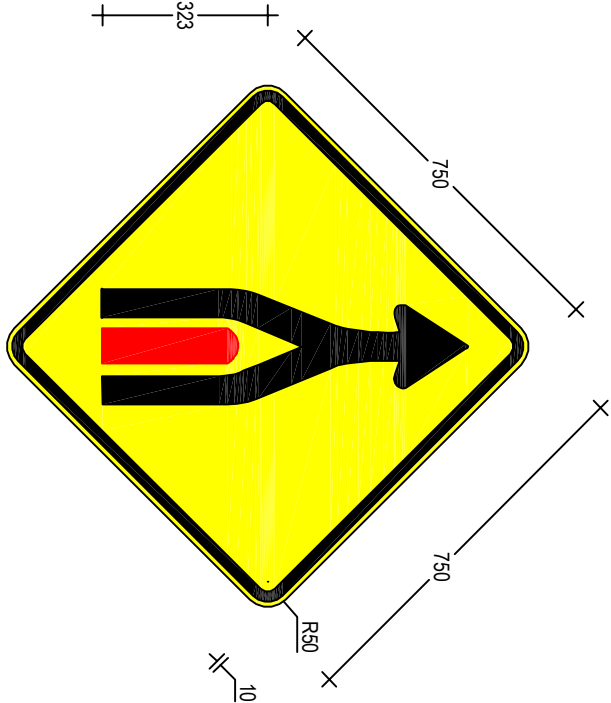


W5-235-1n(B)  
750 x 750

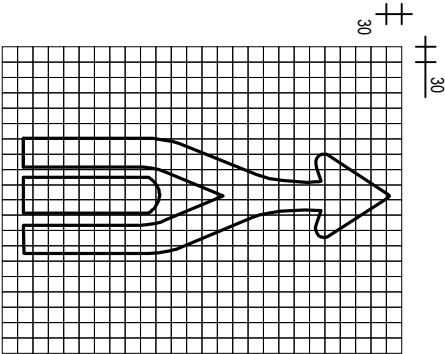

Symbol Detail

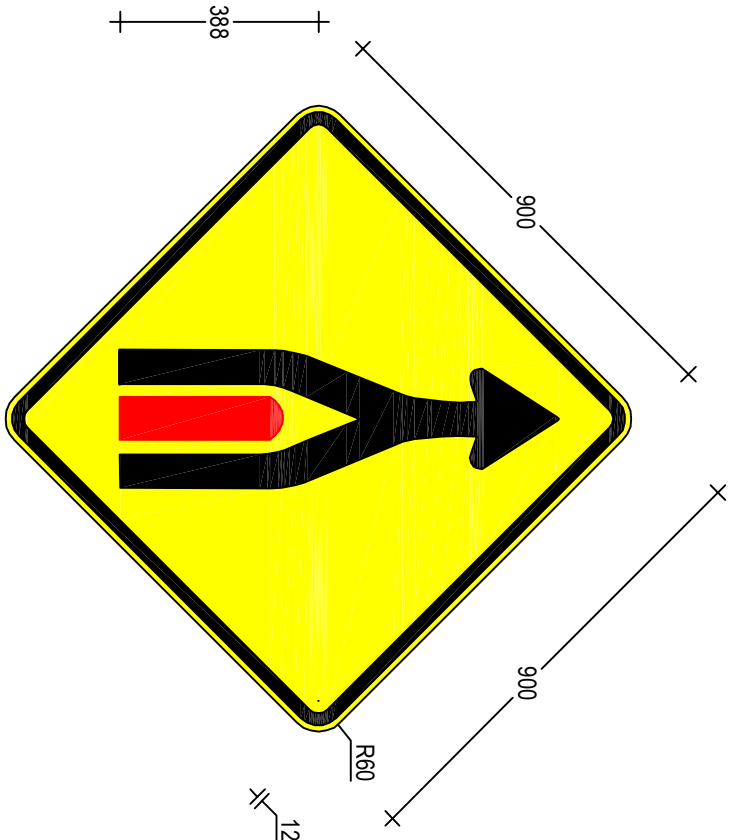

W5-235-1n(C)  
1200 x 1200

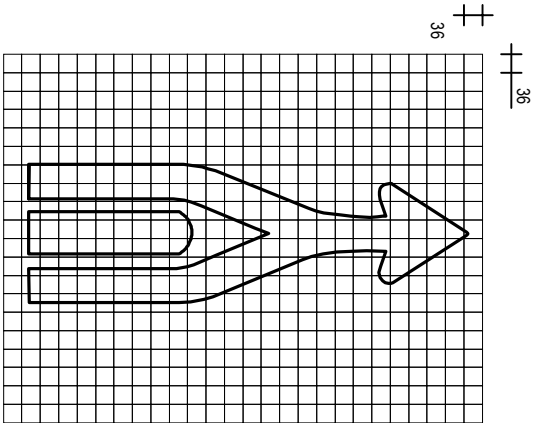

Symbol Detail