


0510253035404550mm ON A3 SIZE ORIGINAL

OR CODE	Scan to Check Document Version	REV	DATE	AMENDMENT / REVISION DESCRIPTION	APPROVAL	DRAWING FILE LOCATION / NAME	DESIGNED	VERIFIED	PREPARED BY	WARNING SIGN	EDMS No	SHEET No	ISS
		01	23-08-18	AS Fonts & material classification revised	P Oliver	W7-12-1N_L.DWG	SIGNED: M. Davies NAME: M. Davies DATE: 31-07-19 REVIEWED: J. Rozdos NAME: J. Rozdos DATE: 31-07-19	SIGNED: P. Oliver NAME: P. Oliver TITLE: Manager, Guidance & Delineation DATE: 31-07-19	NSW Government Transport Roads & Maritime Services GUIDANCE AND DELINEATION UNIT TRAFFIC ENGINEERING SERVICES TECHNICAL AND PROJECT SERVICES	W7-12-1N_L RAIL CROSSING ON SIDE ROAD (T-JUNCTION LEFT ANGLED XING)	XXXXXXX	1	0
ALL DIMENSIONS ARE IN MILLIMETRES UNLESS OTHERWISE SPECIFIED						SIGN TO BE MANUFACTURED IN ACCORDANCE WITH RMS QA SPECIFICATION 3400							

ACCEPTED FOR CONSTRUCTION

Symbol Detail

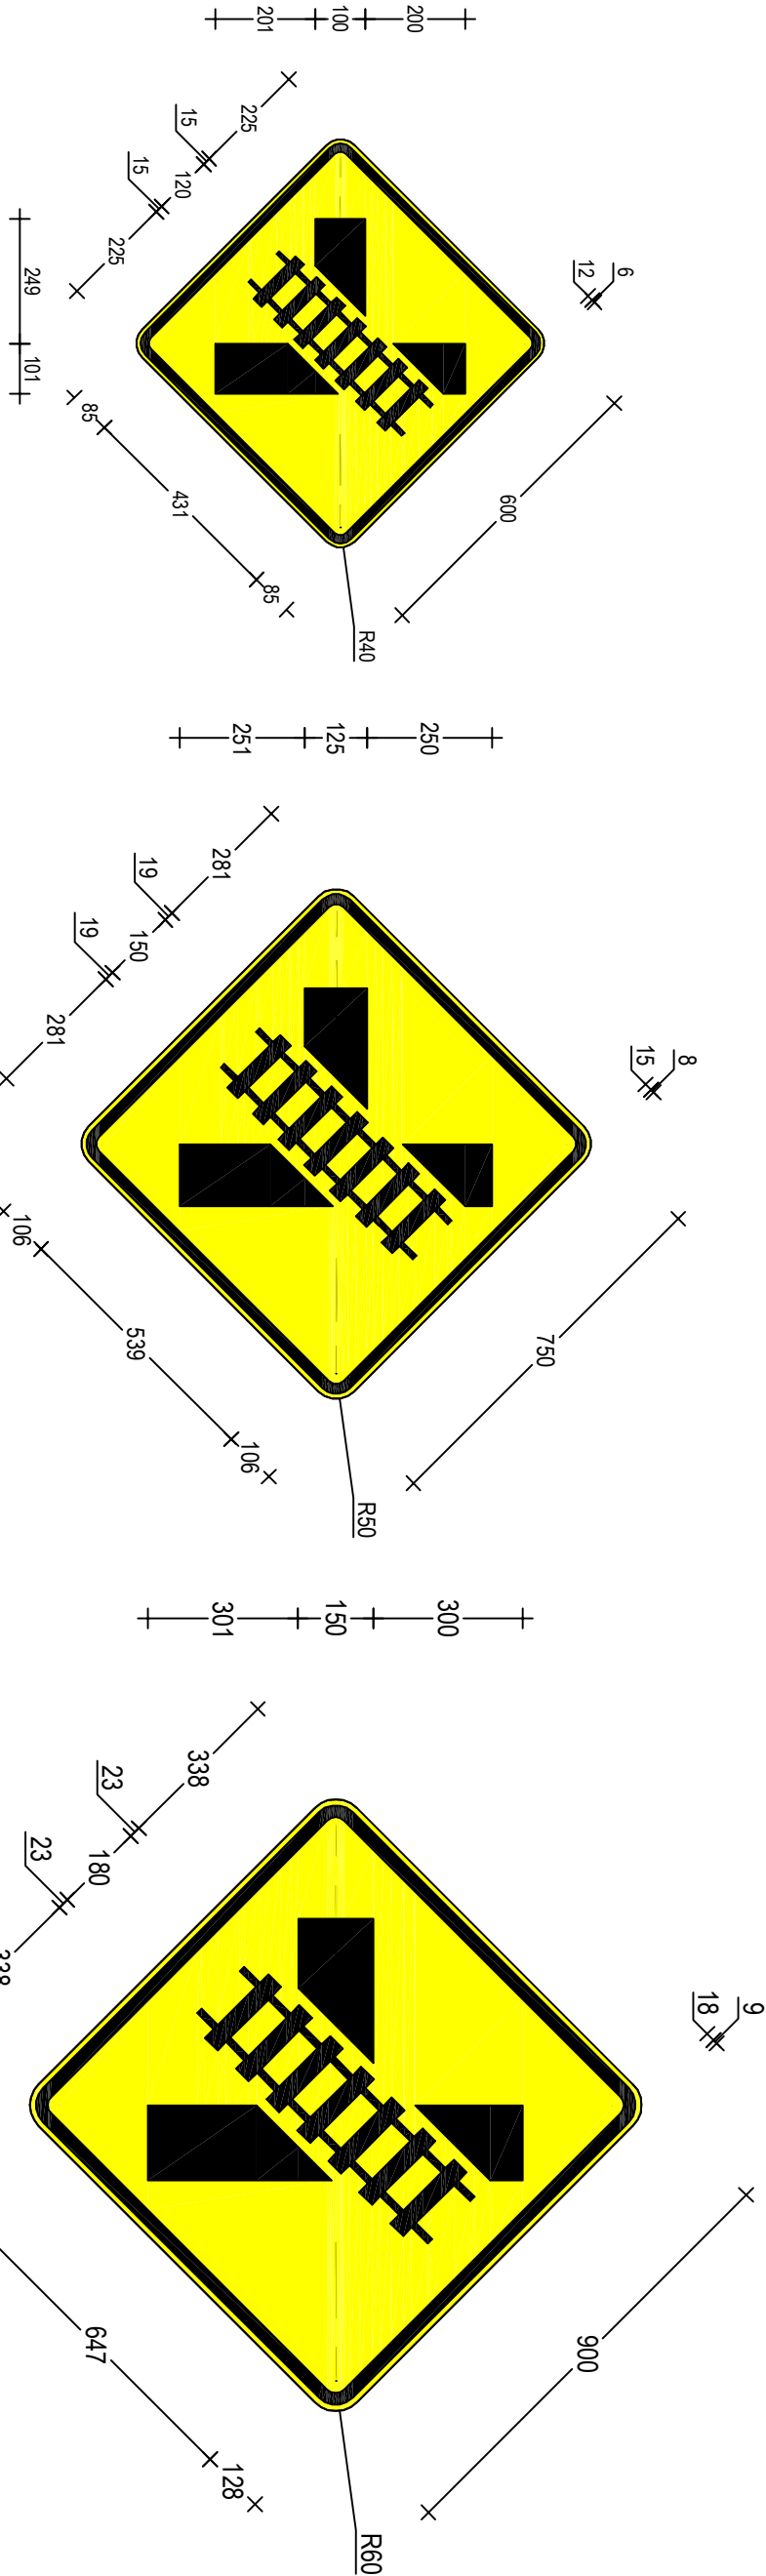

w7-12-1n_L(A)
600 x 600

w7-12-1n_L(B)
750 x 750

w7-12-1n_L(C)
900 x 900

Symbol Detail

Symbol Detail

