



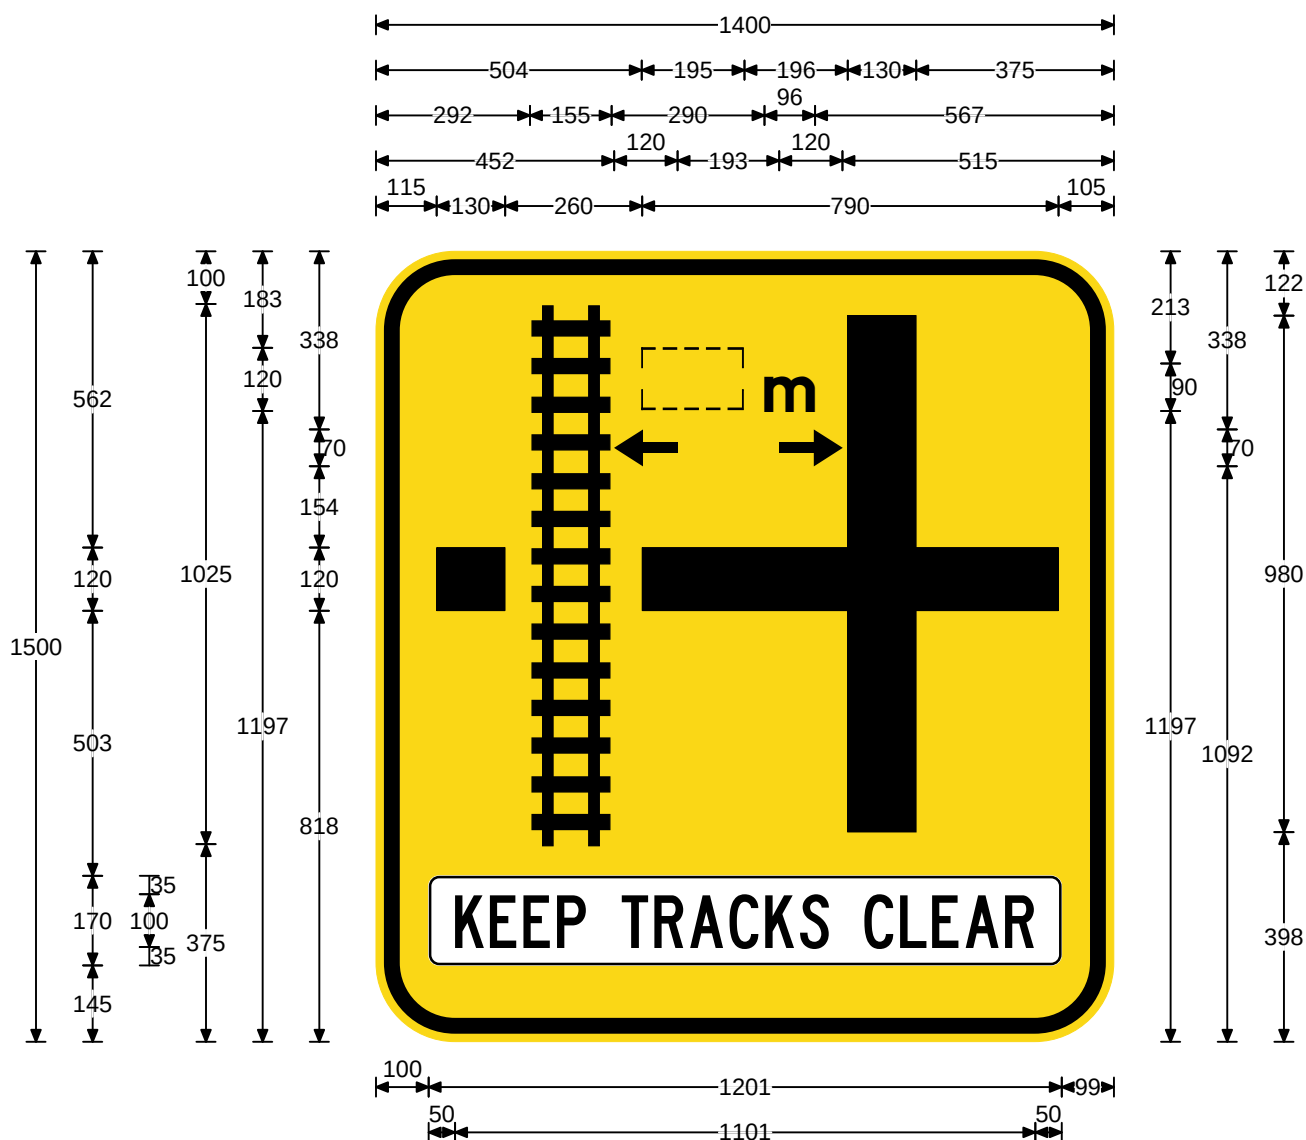

Specifications:
 Aluminium Sign
 Black lgd
 Cl.1 Yellow refl grd
 Keep Tracks Clear:- Black lgd/Cl.1 White refl grd


Size:	1500 x 1400	Date:	15/6/17
Area:	2.1 sq.m	Scale:	1:14.3
Border:	15 x 30	Drawn:	daviesm
Cnr Rad:	150	Checked:	
Patch CR:	0	File:	W7-13-2L
Prepared using TraSiCAD Product of QMR		Path:	H:\Signs\TTT\DRAWINGS\WARNING\TrasiCAD

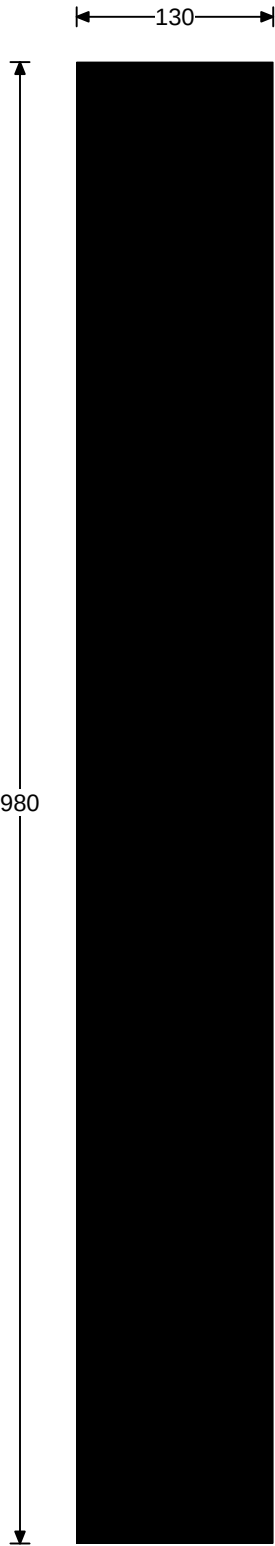

Legend Font Type Font Size

Patch Detail


Size:	980 x 130	Date:	15/6/17
Area:	0.13 sq.m	Scale:	1:5
Border:	0 x 0	Drawn:	daviesm
Cnr Rad:	0	Checked:	
Patch CR:	NA	File:	W7-13-2L
		Path:	H:\Signs\TTT\DRAWINGS\WARNING\TrasiCAD
Prepared using TraSiCAD Product of QMR			

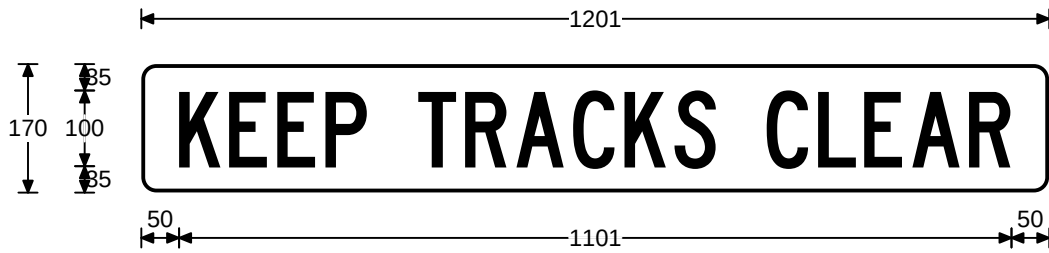

Legend	Font Type	Font Size
KEEP TRACKS CLEAR	AS1744 Series C Narrow	100

Patch Detail

Size:	170 x 1201	Date:	15/6/17
Area:	0.2 sq.m	Scale:	1:10
Border:	0 x 5	Drawn:	daviesm
Cnr Rad:	20	Checked:	
Patch CR:	NA	File:	W7-13-2L
		Path:	H:\Signs\TTT\DRAWINGS\WARNING\TrasiCAD
Prepared using TraSiCAD Product of QMR			

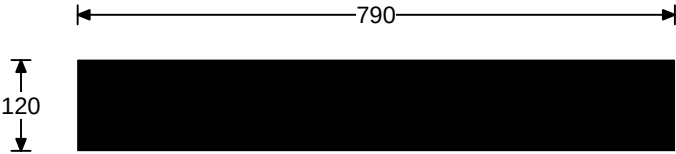

Legend Font Type Font Size

Patch Detail

Size:	120 x 790	Date:	15/6/17
Area:	0.09 sq.m	Scale:	1:10
Border:	0 x 0	Drawn:	daviesm
Cnr Rad:	0	Checked:	
Patch CR:	NA	File:	W7-13-2L
		Path:	H:\Signs\TTT\DRAWINGS\WARNING\TrasiCAD
Prepared using TraSiCAD Product of QMR			



Legend Font Type Font Size

Patch Detail

Size:	120 x 130	Date:	15/6/17
Area:	0.02 sq.m	Scale:	1:1
Border:	0 x 0	Drawn:	daviesm
Cnr Rad:	0	Checked:	
Patch CR:	NA	File:	W7-13-2L
		Path:	H:\Signs\TTT\DRAWINGS\WARNING\TrasiCAD
Prepared using TraSiCAD Product of QMR			